


TAB. XVII

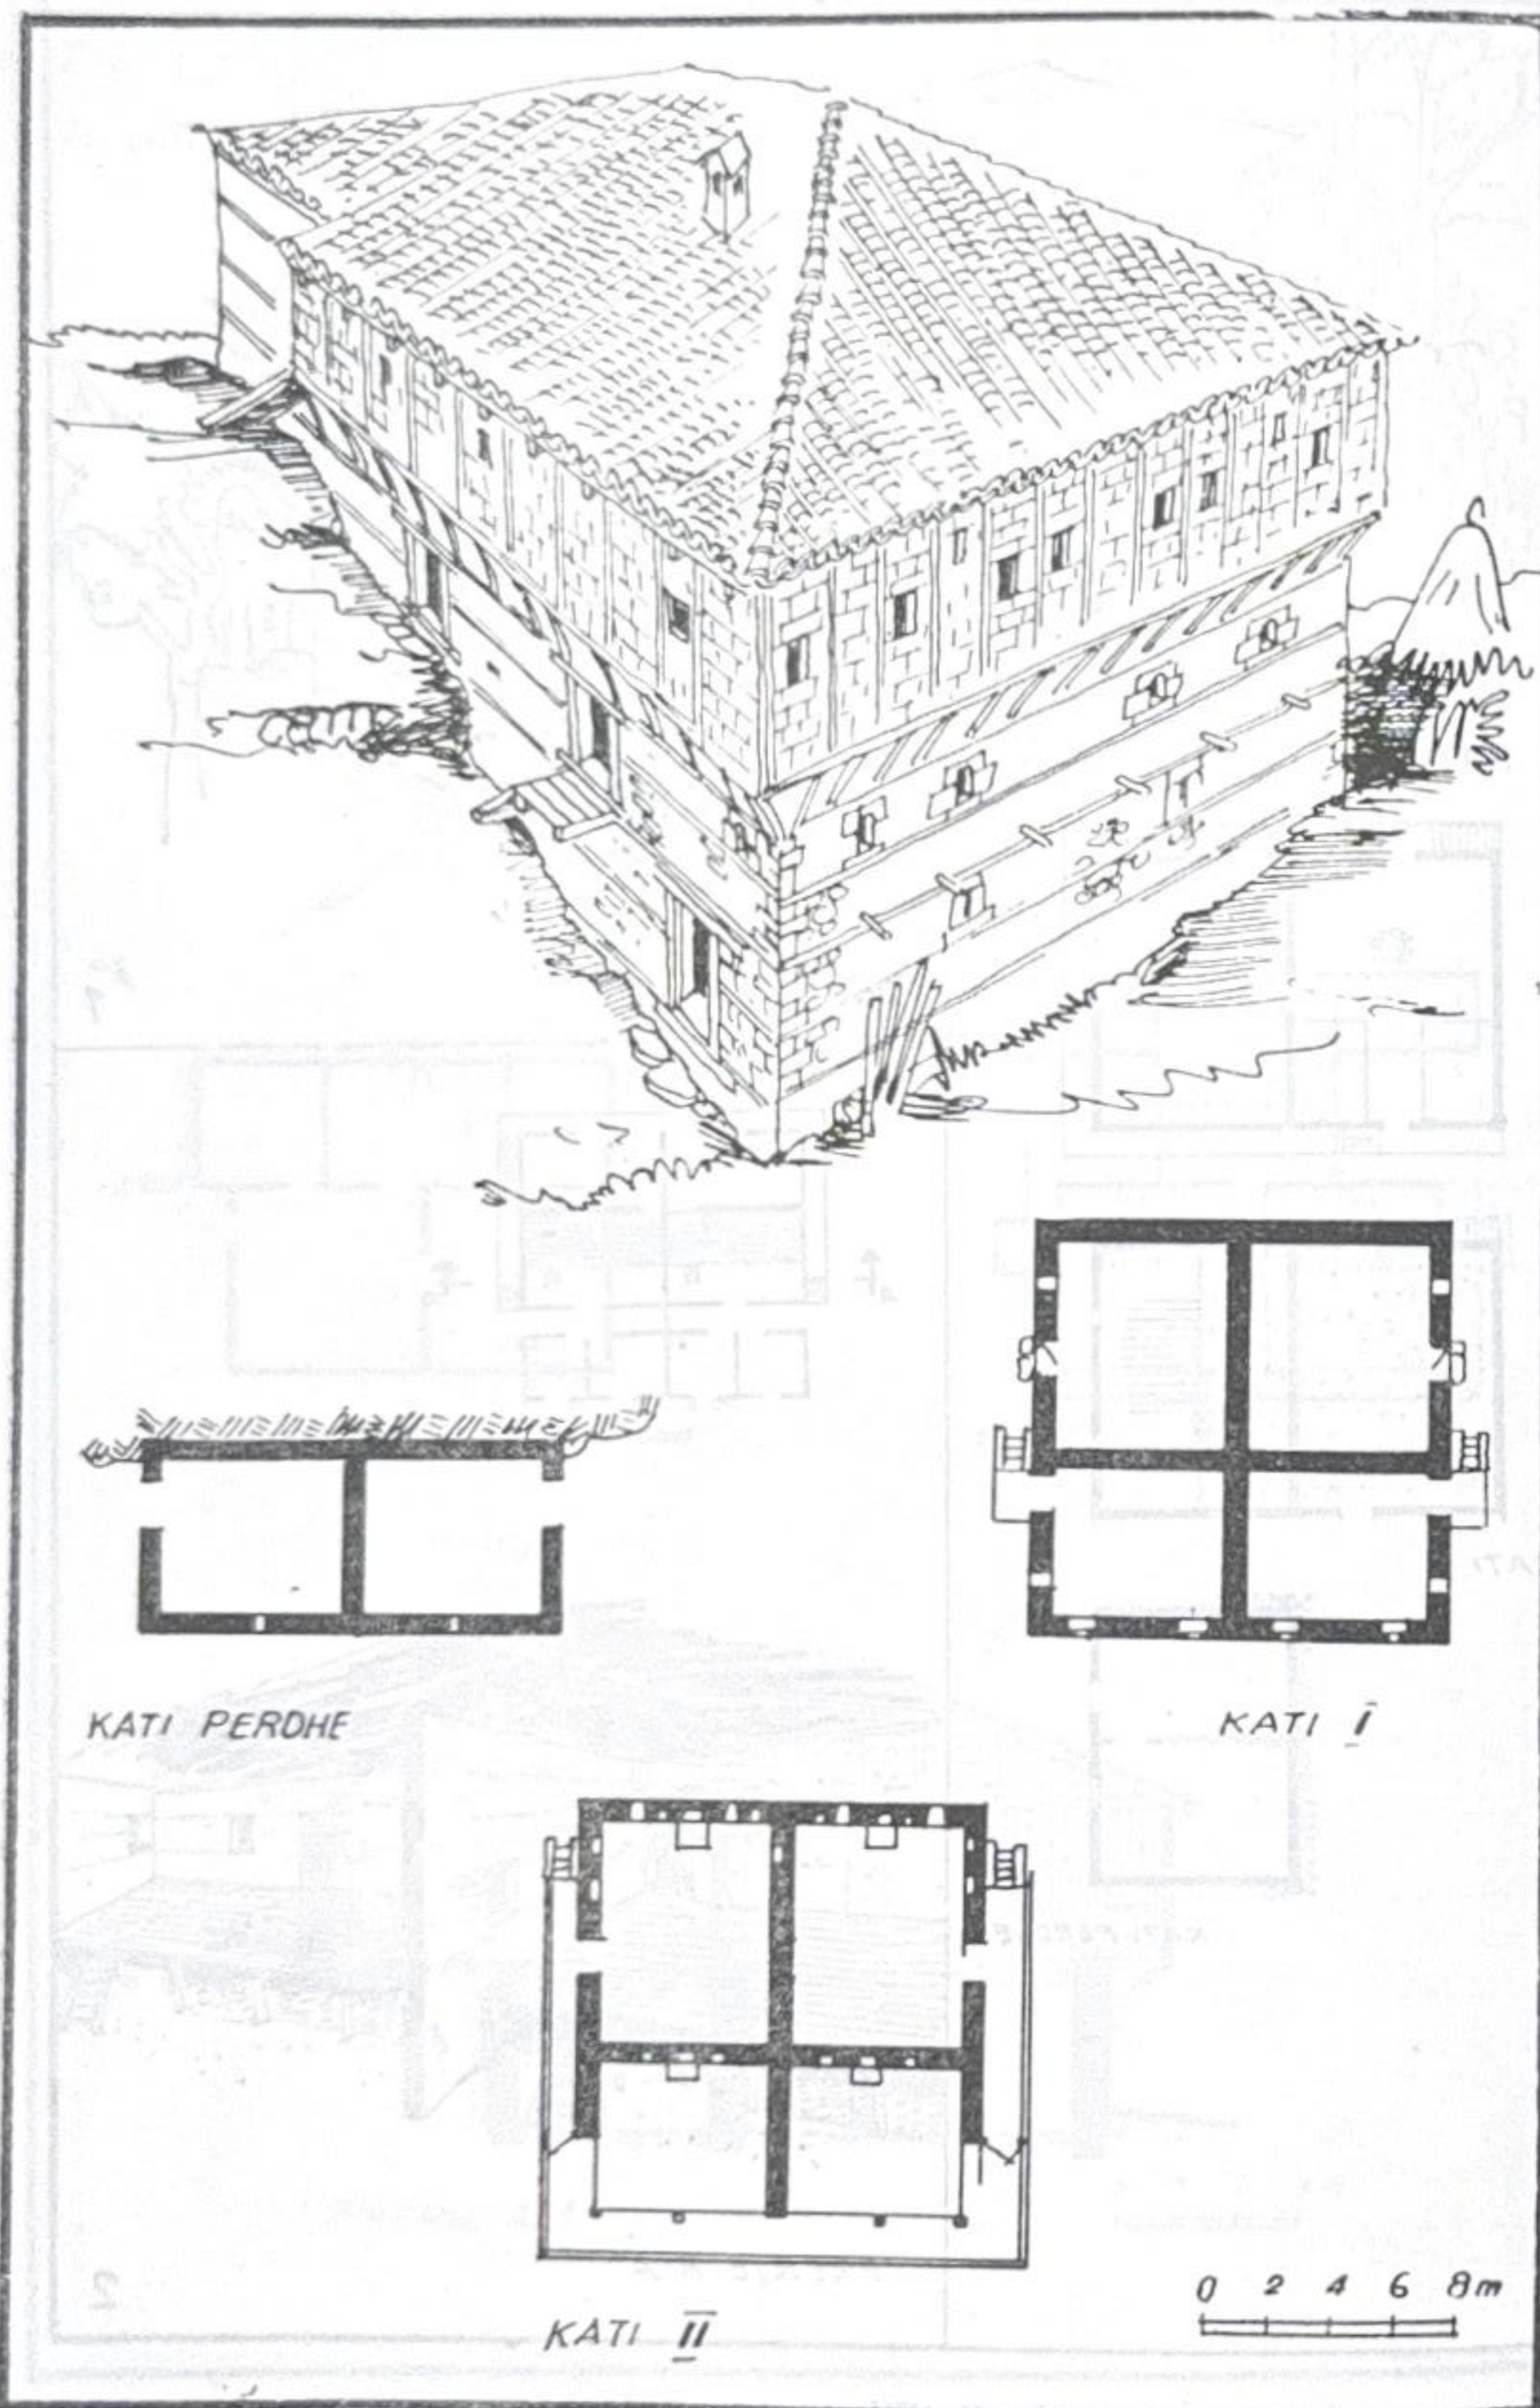

Banese në fshatin Floq (Çermenikë-Librazhd)

Pirro THOMO

TIPARET URBANISTIKE DHE ARKITEKTONIKE TË FSHATIT DARDHË — KORÇË*

Procesi i kalimit nga formacioni ekonomiko-shoqëror feudal në lindjen dhe zhvillimin e marrëdhënieve kapitaliste, në fshatin shqiptar pati një karakter tepër të ndërlikuar. Futja e marrëdhënieve të reja nuk u bë në mënyrë të njëtrajtshme, nuk pati të njëjtën shtrirje dhe nuk qe e njëkohshme në të gjitha krahinat. Shkallë-shkallë ato u shtrinë në marrëdhëniet ekonomike, në strukturën shoqërore, si dhe në mënyrën e jetesës. Të gjitha këto ndikuan dhe u pasqyruan edhe në fizionominë arkitektonike të fshatrave. Karakteri urbanistik dhe tiparet arkitektonike u nënshtrohen ndryshimeve në raport të drejtë me përhapjen e marrëdhënieve të reja.

Të rejat në arkitekturën fshatare u futën në mënyra të ndryshme. Në disa raste ato shfaqen në përmirësimet e skemës funksionale, në përpunimin e trajtimit arkitektonik të brendshëm e të jashtëm, në rritjen e repertorit teknik e teknologjik të ndërtimit, por, shpesh, duke mos u shkëputur tërësisht nga tipologjia tradicionale. Në raste të tjera konceptet e reja arkitektonike ecën më përpara. Ato preken edhe zgjidhjen kompozicionale të banesës, sipas një programi të ri, që pasqyrojnë kërkesat e reja të përdoruesve. U futën kështu tipa të rinj banese, të cilët tjetërsuan pjesërisht ose tërësisht aspektin arkitektonik të venbanimit.

Përfaqësues i procesit të fundit është edhe fshati Dardhë i rrethit të Korçës. Rëndësia e studimit të arkitekturës së këtij fshati nuk qëndron vetëm në evidentimin e pasurisë ndërtimore që ai trashëgoi, por edhe në faktin se përmban në vetvete rëndësinë e një shembulli tipik të një rruge zhvillimi të fshatit shqiptar.

*) Materiali është mbledhur gjatë ekspeditave në terren në vitet 1979 dhe 1983 me pjesëmarrjen e skicografëve Dh. Koti, H. Sava, dhe Gj. Martini. Informuesit kryesorë S. Thimio dhe A. Raci nga fshati Dardhë. Përpunimi i skicave nga Gj. Martini. Foto të autorit.

Dardha është një ndër vendbanimet e pakta të ngritura në një kuotë mjaft të lartë. Lartësia e saj mbi nivelin e detit i kalon të 1000 m. Gjeografikisht shtrihet në shpatin lindor të vargmalit të Moravës, në rrjedhjen e sipërme të lumit Devoll. Etnografikisht Dardha bën pjesë në krahinën e Devollit të Sipërm, e cila në disa aspekte të kulturës materiale dhe shpirtërore ndryshon nga fshatrat e Devollit të Poshtëm.

Historikisht fshati nuk është shumë i vjetër. Gojëdhëna mban si zanafillë të fshatit një vendqëndrim provizor blegtoral, stanet e të cilëve ngriheshin në skajin veriperëndimor të fshatit, ku ruhet toponimi «Stani në Dardhë». Që këtej, shton gojëdhëna, mori emrin fshati. Falë pozitës së mbrojtur, i strukur në thellësi të maleve, vendbanimi i ri i Dardhës filloi të popullohej me banorë të ardhur nga fshatrat përreth. Shkatërrimi i Nikolicës në shek. XVIII, e cila pësoi të njëjtin fat me simotrat e saj, qendrat e zhvilluara në trevën e Korçës, Voskopoja, Vithkuqi, Shipska e më tej Llënga, nga sulmet e bejlerëve dhe derebejve, i dha hov zhvillimit të Dardhës së mbrojtur¹. Shumë nga familjet dardhare mbahen me prejardhje nga Nikolica.

Zona e thellë malore, klima tepër e ashpër dhe terreni i thyer, nuk mund të siguronin kushte të favorshme për kultivimin e bujqësisë. Arat e punueshme ishin të shpërndara përreth fshatit. Ato kishin përmasa të vogla, buzë përrenjve, por fshatarët i përfitonin më tepër me taracim. gjurmët e të cilit shihen edhe sot. Kushte më të favorshme kishte rritja e bagëtive të imta, që formonin një mbështetje të mirë për ekonominë e familjes.

Vendi, nga ana tjetër, është shumë i pasur me pyje. Nxjerrja dhe përpunimi i lëndës drusore u bë shpejt mbështetje e sigurt ekonomike. Me këto zeje dardharët u bënë të njohur jashtë fshatit e vendit. Ata filluan të bëheshin të kërkueshëm për shfrytëzimin e pyjeve në vendet fqinje, në viset e Kosovës (Pejë), të Greqisë e të Turqisë. Kjo i dha shkas përhapjes në masë të emigrimit sezonal. Ashtu si dhe për mjeshtritë e tjera të ushtruara nga popullsia shqiptare, largimi i burrave fillonte në nëntor (Shën Mitër) dhe mbaronte në pranverë (Shën-Gjergj). Fitimi nga puna e krahut ishte mjaft i vogël, prandaj një rol të rëndësishëm në ekonominë e familjes luante ende ekonomia vendase e bazuar në prodhimin e paktë të bujqësisë dhe të ardhurat nga blegtoria.

Rritja e ndjeshme e rendimentit dhe e prodhimit të lëndës së drurit u bë nëpërmjet futjes në përdorim të sharrave të ujit. Ndërsa në fshat ato ishin të pakta, në viset tradicionale të mërgimit të dardharëve, sharrat u ngritën me shumicë. Sipas të dhënave të tërthorta, ngritja e sharrave të ujit filloi andej nga gjysma e dytë e shek. XVIII. Ato erdhën gradualisht duke u shtuar, përsosur dhe zmadhuar, duke u

kthyer në ndërmarrje të vogla prodhimi. Ndërtimi dhe administrimi i tyre nuk bëhej më në mënyrë individuale, por me «ortakëri», zakonisht nga bashkëfshatarë. Kështu p.sh. sharra e ndërtuar në Adalia të Anajanë ruajtur të dhëna të plota dhe fotografia e saj (Fig. 1), ishte pronë e katër bashkëfshatarëve. Sipas të dhënave gojore ajo prodhonte deri në 85.000 dërrasa katërmetërshe në vit.

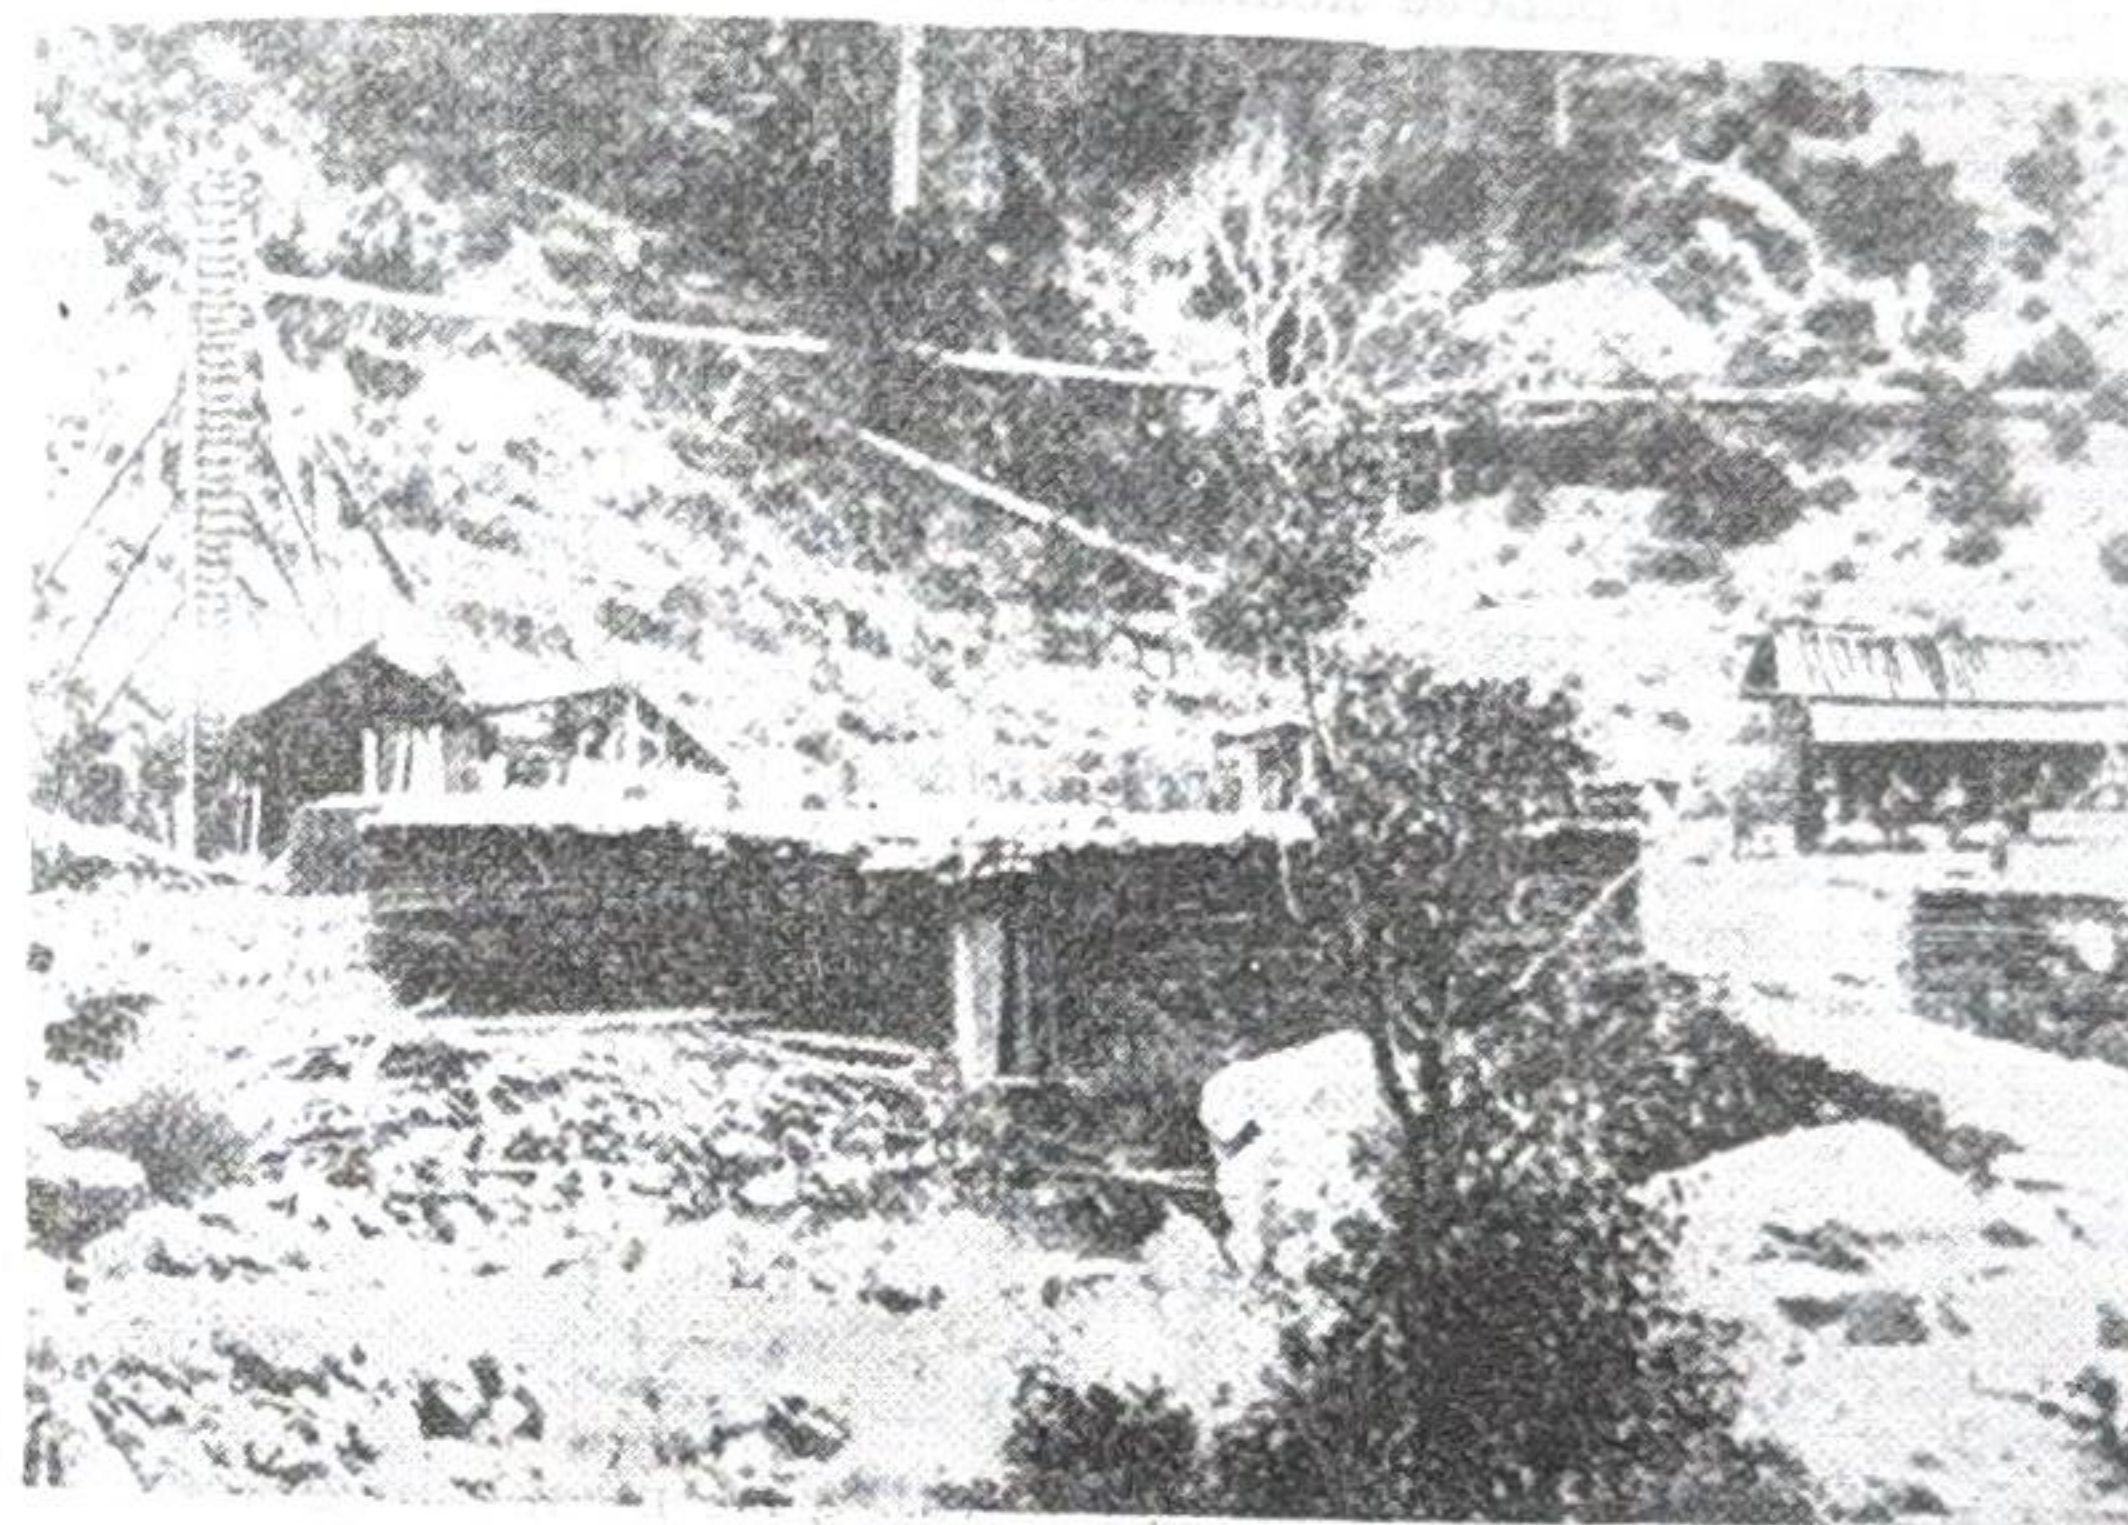


Fig. 1

Ndërtimi i sharrave u dha dorë dardharëve që, diku vetë e diku në bashkëpunim me pronarë vendas, të shtinin në dorë jo vetëm prodhimin e lëndës, por, më vonë dhe tregtinë e saj. Kjo bëri që disa familje ose individë të familjes të shpërnguleshin përfundimisht nga fshati. Megjithëse të ardhurat nga prodhimi i lëndës erdhën duke u shtuar, nuk mund të ishte një zgjidhje përfundimtare për ekonominë e fshatit, për më tepër që kjo zëjtari që fatlume vetëm për një numër të kufizuar familjesh. Krijimi i shteteve të pavarura ballkanike dhe konfliktet ndërmjet tyre, vënia dorë mbi shfrytëzimin e pyjeve nga shtetet dhe pronarët vendas u preu rrugën dhe u hoqi punën shumë krahëve të afta dardhare. Ekonomia e vendit ishte e pamjaftueshme për sigurimin e jetesës së masës së gjerë të fshatarësisë. Fundi i shek. XIX, fillimi i shekullit XX shënon një shtim të ri të valës së emigrimit për shitjen e krahut të punës, në fillim në vendet e Ballkanit (kryesisht në Rumani), e më vonë në SHBA dhe vendet e tjera të Amerikës.

Të ardhurat e nxjerra nga kurbeti u investuan kryesisht në ndërtimin e banesave, në pajisjet dhe mobilimin e tyre, si dhe në punimet

1) P. Pepo, Kontribut mbi historinë e tregut të Korçës e të Voskopojës gjatë sundimit otoman, në «Korça e Re», Korçë, 1964, fq. 180.

komunale: në shtrimin e rrugëve, në sjelljen e ujit, në ndërtimin e çezmave etj., ndërsa mbas kthimit në atdhe, në hapjen e punishteve dhe dyqaneve në fshat. Një hov të madh morën punimet komunale, sidomos në vitet 20-30 të shekullit tonë, me krijimin e shoqërive në fshatra. Në Dardhë u ngrit shoqëria «Shpresa». Një nga detyrat kryesore të këtyre shoqërive, përveç gjallërimit të jetës shoqërore në fshat, ishte dhe grumbullimi i ndihmave dhe mobilizimi i popullsisë për kryerjen e punëve komunale. Në kushtet e një prapambetjeje të përgjithshme ekonomike të vendit dhe të mungesës së plotë të investimeve nga ana e shtetit, sidomos në fshat, kjo ishte e vetmja rrugë për rregullimin e fshatrave. Kështu u zgjerua dhe u shtrua me kalldrëm rruga qendrore e fshatit, u ngritën disa ndërtesa shoqërore, si shkolla etj., u bënë projekte për shfrytëzimin e ujit mineral që buron në afërsi të fshatit etj.

Si rezultat i kësaj rruge zhvillimi, fshati i Dardhës në fillim të shek. XX paraqitej me një fizionomi urbanistike dhe arkitektonike të formuar dhe të përparuar për kohën. Të gjitha rrugët ishin të kalldrëmuara, fshati ishte i pajisur me një sistem të plotë ujësjellësi dhe me çezma të përhapura në të gjitha pikat, me ndërtesa të bukura e solide dhe dallohej për një jetë të gjallë, një rrjet të plotë tregtie e shërbimi. Në fshat funksiononin një numër i madh punishtesh të hapura në lokale të veçanta ose në shtëpi, ku ushtroheshin zejet kryesore: rrobaqepës, këpucarë, teneqexhinj, marangozë, sahatçinj, saraçë, kovaçë e deri fotografë. Funksiononin gjithashtu njësi tregtie (bakallë), furra, kasapë, ëmbëltore, hane e hotele.

I gjithë zhvillimi historik i fshatit Dardhë mund të ndahet në tri periudha kryesore me karaktere të ndryshme ekonomiko-shoqërore dhe me tipare të dallueshme arkitektoniko-urbanistike. Periudha e parë shkon nga themelimi i fshatit deri në mesin e shek. XIX, periudha e dytë përfshin gjysmën e dytë të shek. XIX, ndërsa e treta dhjetvjeçarët e parë të shek. XX.

KARAKTERI URBANISTIK

Fizionomia urbanistike e Dardhës erdhi duke u formuar e përsosur shkallë-shkallë dhe ne sot kemi një tablo të plotë të saj, gjendjen që arriti në dhjetëvjeçarët e parë të shekullit tonë.

Për ndërtimin e fshatit është zgjedhur pjerrësia e një shpati, e orientuar nga lindja, pra që rrihet mirë nga dielli dhe është e mbrojtur nga rrymat e ftohta të erërave. Shpati zbret jo tepër butë mbi përroin e Dardhës, afërsisht i Devollit, i cili e kufizon fshatin nga ana jugore dhe lindore. Fshati është i shtrirë gjatë gjithë shpatit, me konfiguracion gjatësor, me një shtrirje tërthore më të madhe nga ana veriore (Tab. I). Ai është mjaft i mbledhur, me ndërtesa pranë njëra-tjetrës (Fig. 2). Kështu është formuar një ndarje ose shkëputje e zonës së banuar dhe asaj bujqësore dhe instalimeve të saj. Siç e kemi vënë në dukje më sipër, arat ishin të shpërndara përreth fshatit. Brenda fshatit pranë shtëpive kishte parcela të vogla që përdoreshin si kopshte. Në pjesën fundore të fshatit ishin ndërtuar disa lëmenj, por këta

ishin të paktë. Zona tradicionale e lëmenjve ndodhej në një lartësi përkundrajt fshatit, në krahun e majtë të përroit.

Ende sot ka mbetur toponimi «Të lëmenjtë». Gjatë përroit ishin të rreshtuar 9-10 mullinj drithi, pronë e familjeve të veçanta, të cilat merreshin kryesisht me këtë mjeshtëri, ose e kishin si ekonomi ndihmëse. Me ujërat e këtij përroi funksiononin dhe dërstilat e batanet. Sot ka mbetur vetëm toponimi dhe kujtesa e të moshuarve si dëshmitarë e kësaj zeje. Në pjesën e sipërme të përroit ishte ndërtuar një sharre uji.

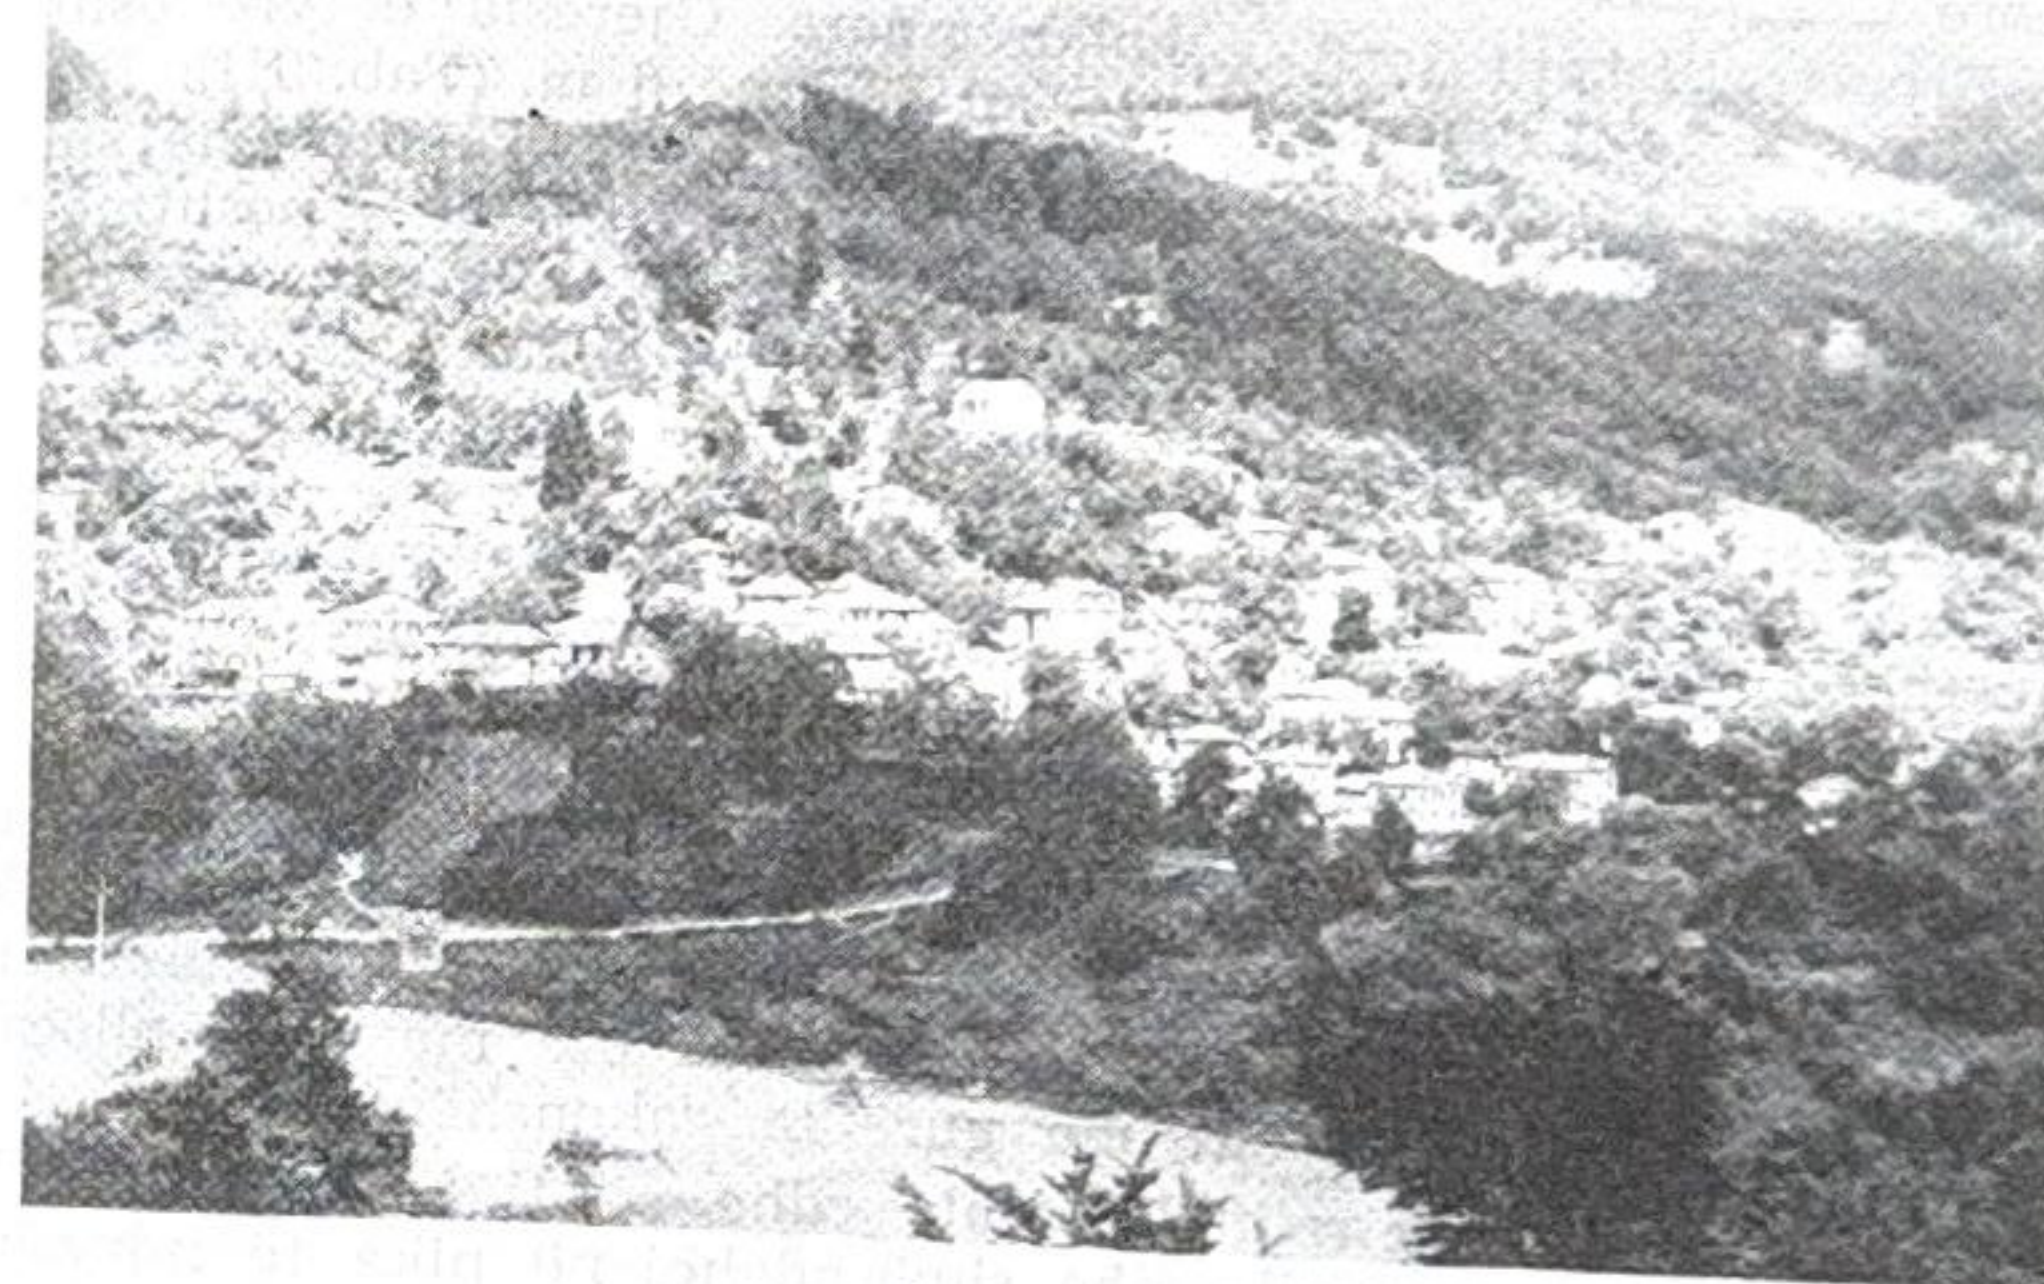


Fig. 2

Në zonën e banuar nuk vihej re ndonjë ndarje e prerë lagjesh ose ndonjë qendër e theksuar kompozicionale. Megjithatë vërehej një parapëlqim për vendosjen e ndërtimeve me funksion të përba-shkët. Ishte krijuar kështu një zonë me përqëndrim ndërtimesh të tilla në krye të fshatit, në një pozitë zotëruese, në afërsi të vendqëndrimit të hershëm të blegtorëve, «te stanet», që, sipas gojëdhënës, ka qenë zanafilla e fshatit. Aty ishte ndërtuar kisha, një han i vjetër, më vonë, gjatë këtij shekulli, një hotel-restorant, shkolla, ndërtesa e komunës, etj. Me hapjen e rrugës automobilistike që lidhte Dardhën me Korçën, në dhjetëvjeçarët e parë të shek. XX dhe të frekuentimit më të dendur të fshatit si qendër klimaterike, u ndërtuan hotele e kafene dhe në të hyrë të fshatit, nga ana veri-perëndimore. Gjithashtu aty ishin përqëndruar disa dyqane e punishte zejtarësh.

Por ndërtimet e këtij karakteri nuk ngriheshin vetëm në këtë zonë. Ato ishin shpërndarë në të gjithë fshatin. Zejtaritë ushtroheshin në

ndërtime të veçanta ose brenda banesës. Disa banesa kishin për këtë qëllim ambiente që përdorshin si dyqane, e me lidhje të drejtpërdrejta me rrugën. Kështu dora-dorës, nga gjysma e dytë e shek. XIX, filloi të merrte rëndësi dhe rruga e poshtme e fshatit, ku ishin të grupuara disa dyqane kryesore e punishte (Tab. II).

Fshati përshkohet nga tri rrugë gjatësore, që ndjekin nivelet e terrenit. Në skajin jugor ato bashkohen, duke krijuar një unazë që e qarkon të gjithë fshatin. Pjesa jugore ka një rrjet rrugor disi më të çrregullt. Në pjesën qendrore kalon një rrugë tërthore, e cila ngjitet me gjarpërime dhe lidh rrugët gjatësore. Rrugica të tjera më të ngushta degëzohen nga rrugët kryesore dhe lidhin mbarë njësitë ndërtimore të fshatit.

Rrugët e fshatit janë të kalldrëmuara. Gjerësia e tyre është e ndryshme, duke u luhatur nga 2.5 m. deri në 6 m. (Tab. III). Rrugët kufizohen nga banesat, muret rrethuese të oborreve ndërsa në shumë vende, nga muret mbajtëse, të cilat ngrihen në pjesët e poshtme për të mbajtur rrugën dhe në të sipërmen si mbështetje e terrenit të pjerrët. Disa herë lartësia e mureve mbajtëse shkon deri 4-5 m. Në këto raste ato ndërtohen me pjerrësi dhe me shkallëzime. Profili i rrugëve ose ndërtimi i tyre është i ndryshëm, në varësi nga terreni, pjerrësia dhe, së fundi, në varësi nga koha e ndërtimit. Profilet më të përdorshme kanë qënë ato me kunetën e largimit të ujit në mes të rrugës. Ky tip zakonisht është zbatuar në rrugicat e ngushta dhe në rrugët e vjetra. Një tip më i përparuar kalldrëmi, i përdorur në rrugët e gjëra dhe ato të shtruara më vonë, është me kurriz në pjesën qendrore, ndërsa largimi i ujërave atmosferikë bëhet nga dy kuneta anësore në të dy skajet e rrugës. Kurrizi i rrugës është trasuar me gurë të mëdhenj lumi, kunetat me plloça ose me gurë plloçakë, ndërsa mbushja e kalldrëmit me gurë të zakonshëm lumi.

Një shpërndarje të rregullt kishte edhe rrjeti i ujësjellësit. Uji sillej me tubacione qeramike dhe shpërndahej në pika të ndryshme të fshatit. Çezmat janë të ndërtuara në kryqëzimin e rrugëve, si dhe gjatë rrugëve kryesore, në pika të hapura në muret mbajtëse. Shumë nga çezmat dallohen nga përkujdesja në trajtimin arkitektonik. Disa ishin të mbuluara (Fig. 3), grykat e çezmave përpunoheshin me gurë të gdhendur në formë lugu (Fig. 4), ndërsa poshtë tyre ishin vendosur koritat ose govatat prej druri ose guri, ku pinin ujë kafshët dhe laheshin rrobat.

Njësitë kryesore ndërtimore të fshatit janë banesat me ndërtimet e tyre ndihmëse. Banesat janë të rrethuara me oborre zakonisht të vogla, të cilat kanë karakter të ndryshëm në periudha të ndryshme. Në periudhat e hershme rezervat kryesore ekonomike dhe bagëtitë e familjes ruheshin në ambiente të përfshira brenda volumit të banesës. Në oborr ngriheshin plevicat, ashefet dhe furra e pjekjes. Në parcelën përreth banesës kultivoheshin pemë dhe perime. Nga banesat e periudhave më të vonshme largohen bagëtitë dhe strehohen në plevicat, të cilat ngriheshin pranë ose dhe larg banesës. Plevicat zakonisht ndërtoheshin dykatëshe: kati përdhe shfrytëzohej për mbajtjen e bagëtive,

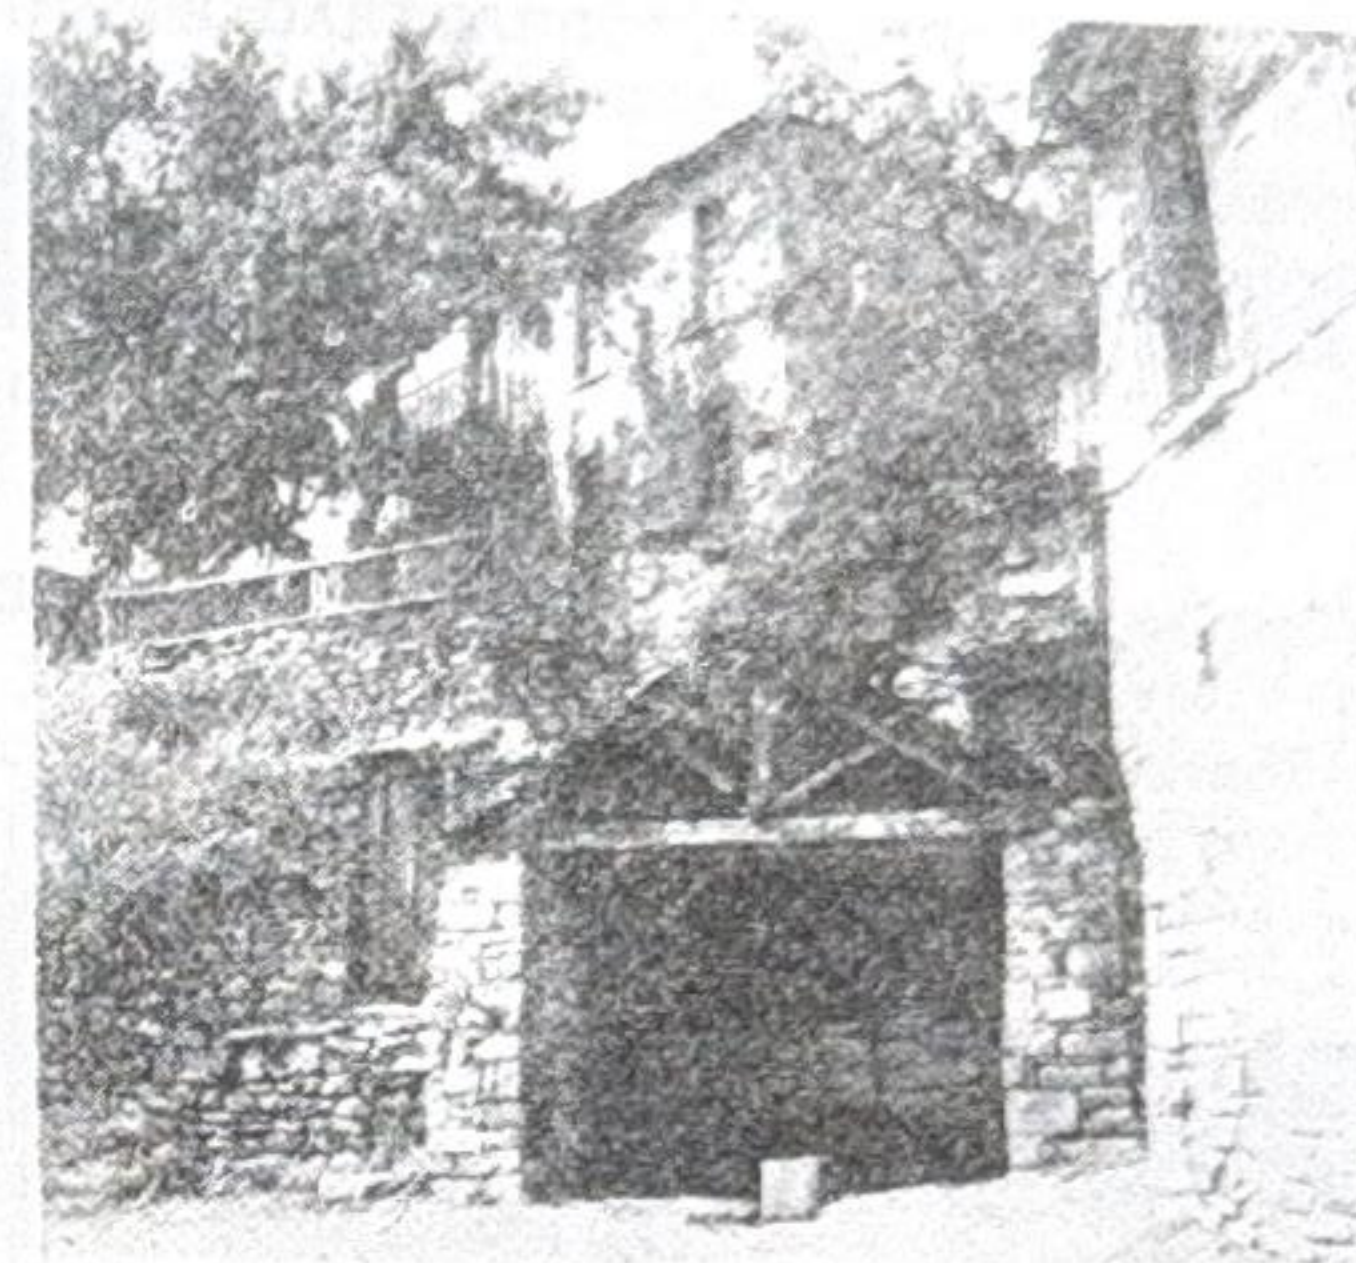


Fig. 3

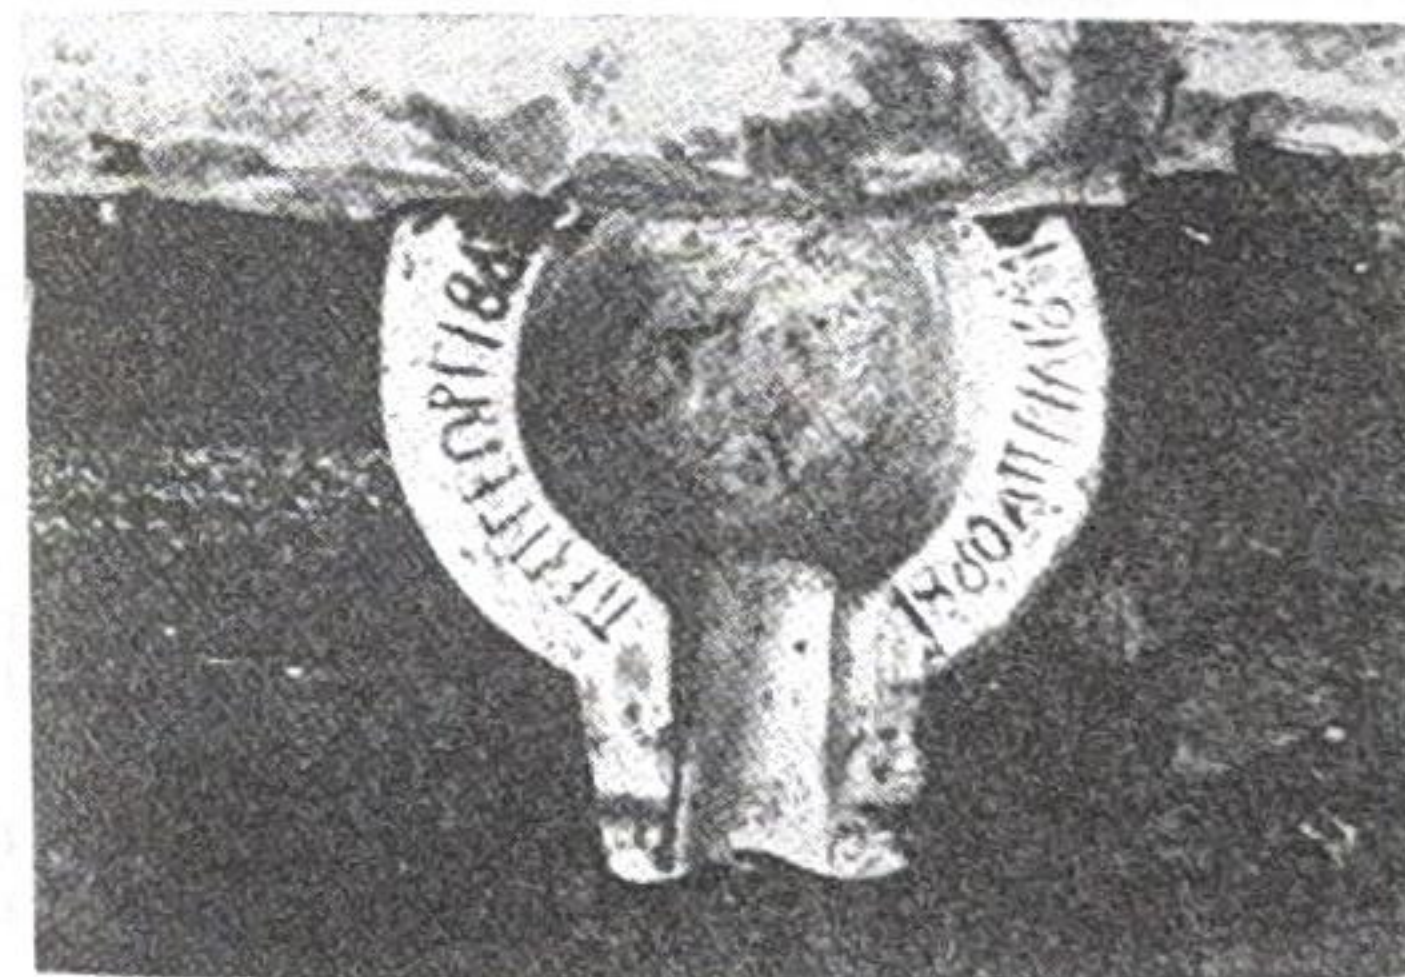


Fig. 4

ndërsa i dyti për depozitimin e barit e të kashtës. Me ndërtimin e banesave të reja, të vjetrat u përdorën gjerësisht për plevica.

Periudhat më të reja sollën ndryshime të ndjeshme dhe në fizionominë e përgjithshme urbanistike të fshatit. Ndërsa banesat e vjetra zakonisht ishin të tërhequra nga rruga ose dilnin me një faqe anësore në rrugë, duke pasur ballin kryesor të orientuar nga oborri, banesat e reja dalin shpesh në rrugë, marrin pjesë në formimin arkitektonik dhe e gjallërojnë së tepërmi atë. (Fig. 5, 6, 7).

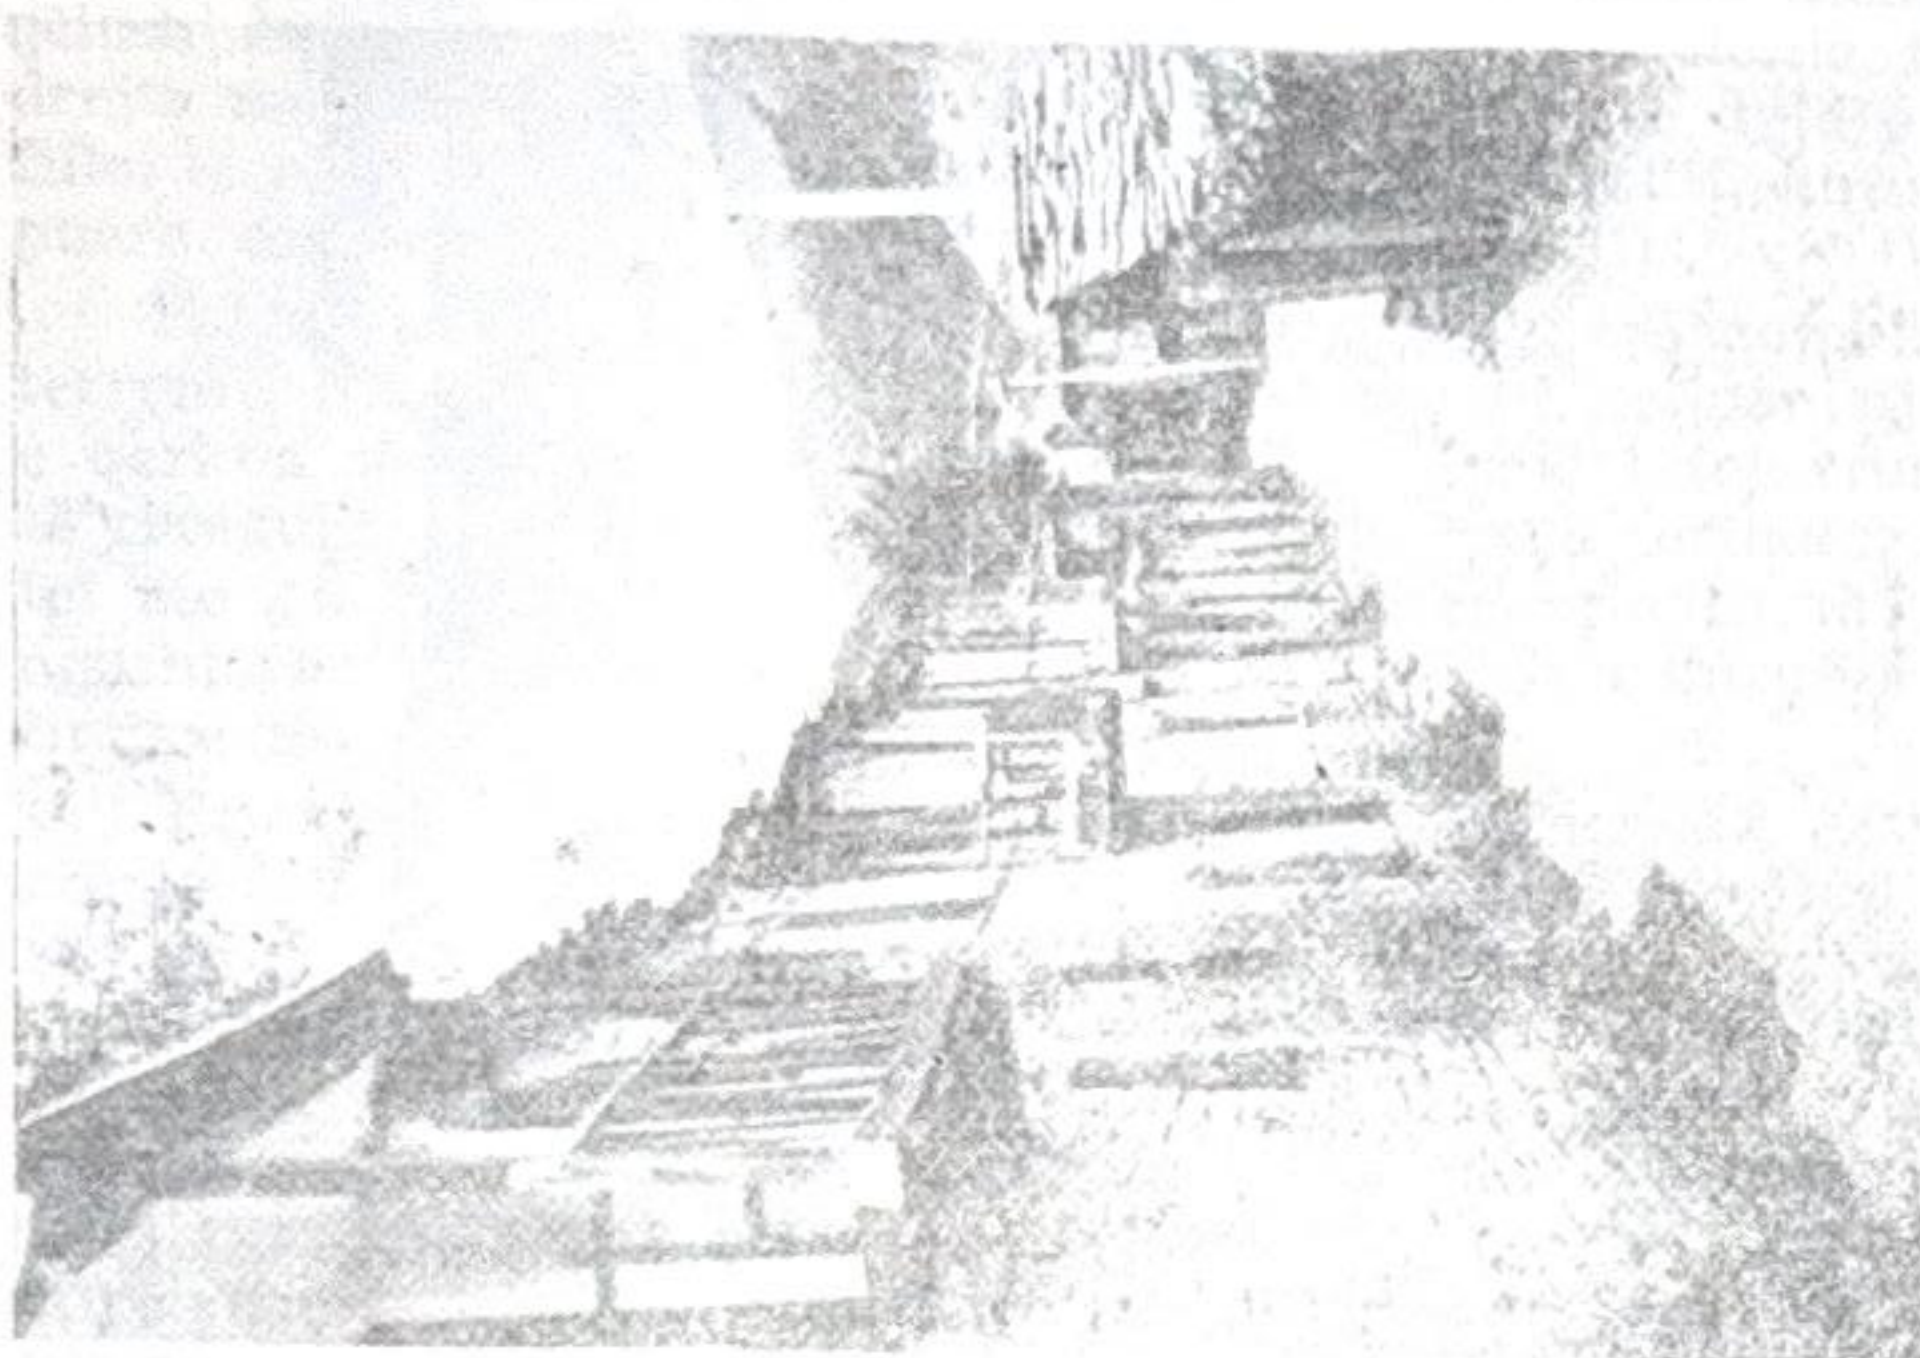


Fig. 6

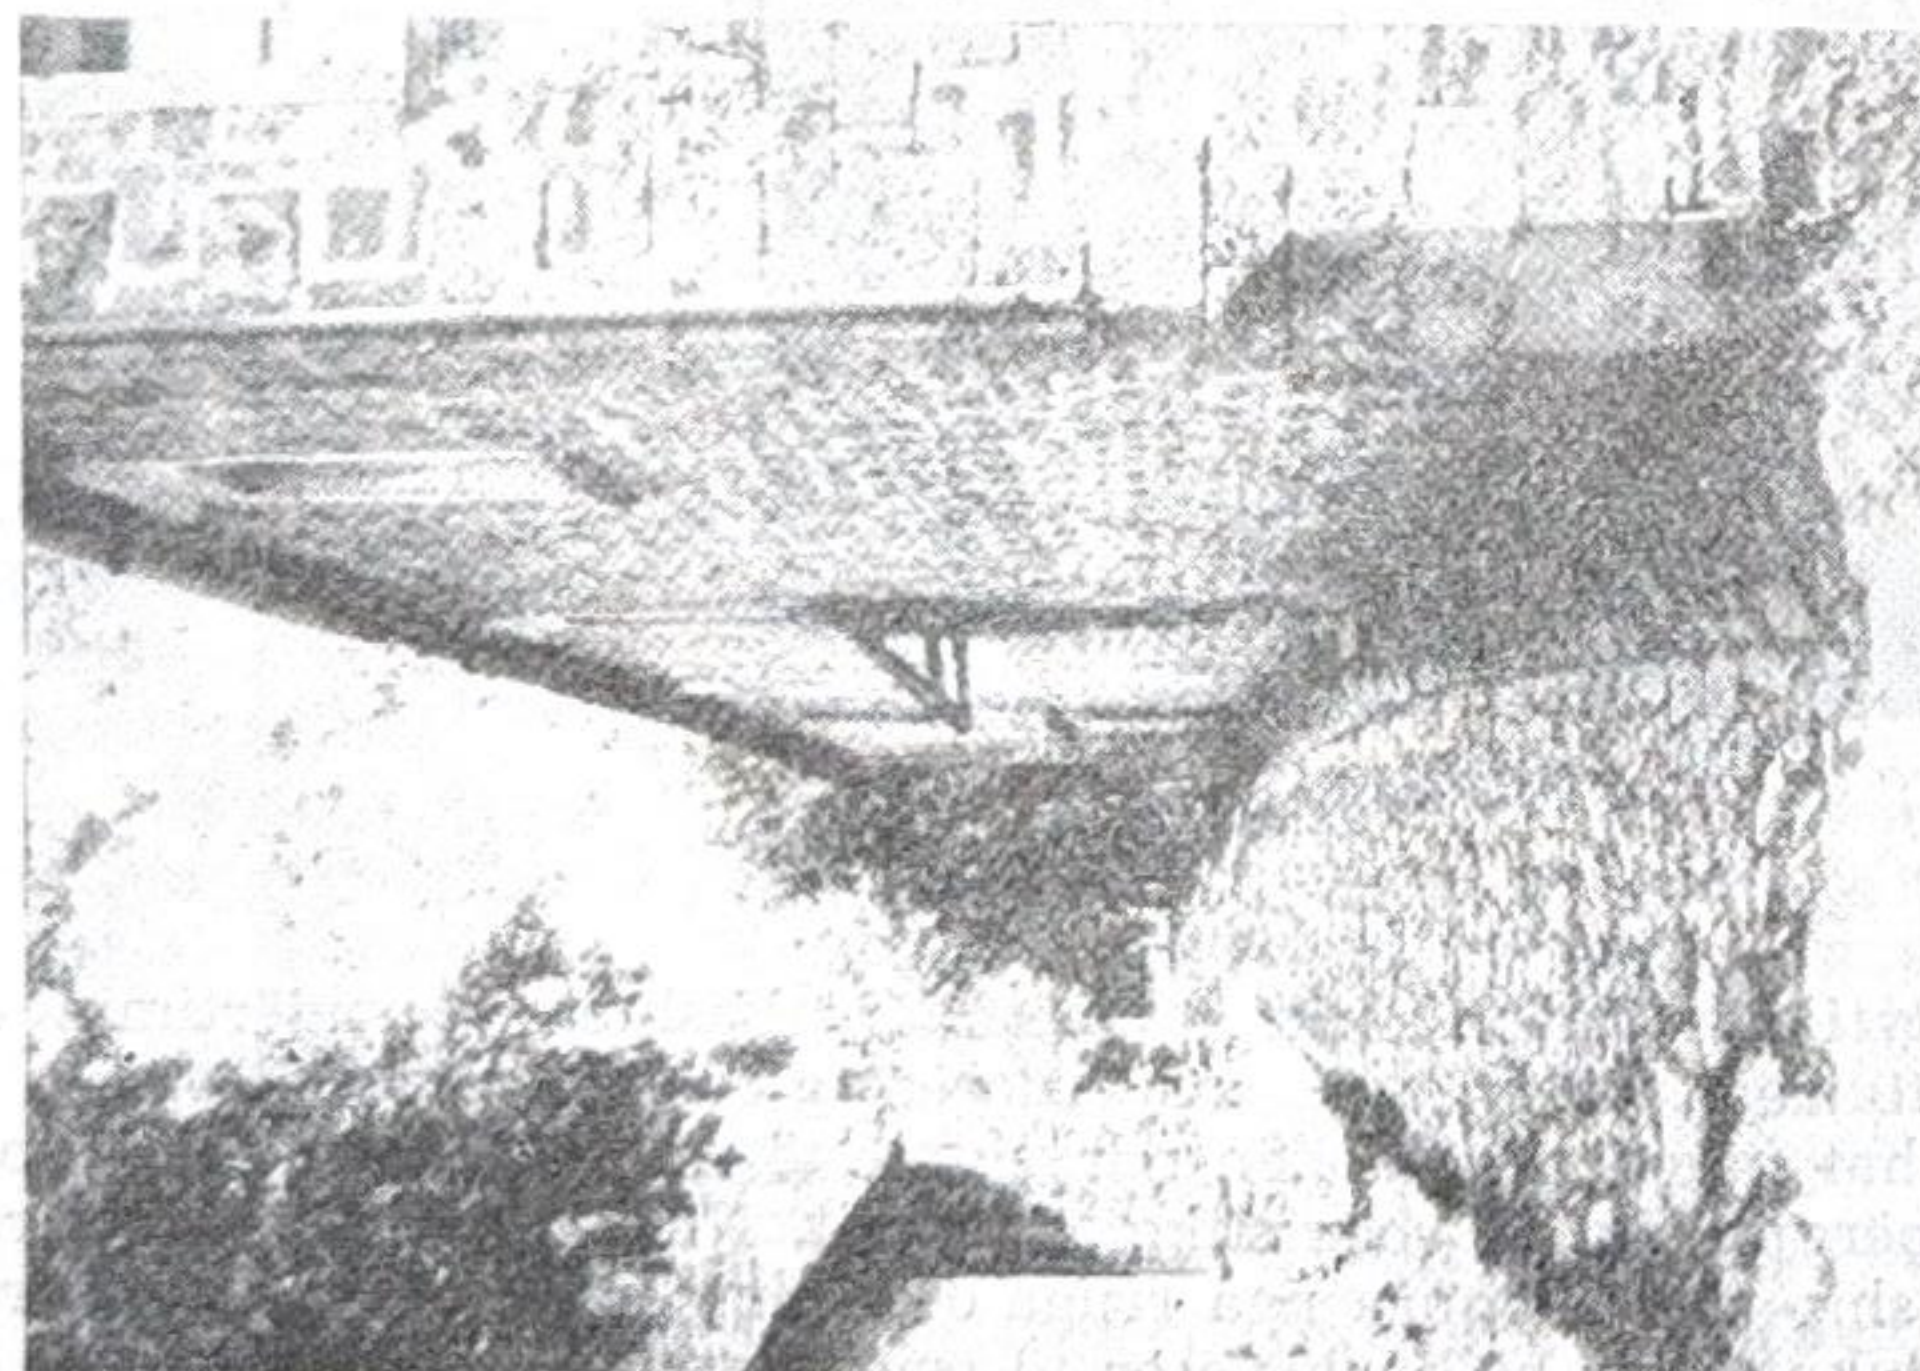


Fig. 5

TIPOLOGJIA E BANESËS DARDHARE

Ndërsa për urbanistikën e fshatit, për shkak të ndërtimeve dhe të përmirësimeve të herëpashershme, është e vështirë të përcaktohet fizionomia sipas periudhave të zhvillimit të fshatit, tipologjia e banesës e pasqyron shumë qartë këtë zhvillim. (Tab. IV).

BANESAT E PERIUdhës së parë

Një tablo deri diku e plotë për ndërtimet e kësaj periudhe mund të krijohej nga disa ndërtesa të mbetura ende në këmbë, ruajtja e të cilave u favorizua shumë nga përdorimi i tyre deri vonë si plevica.

Megjithëse në shumicën e rasteve ato nuk ruhen të plota, mund të zbulohen tiparet kryesore arkitektonike, si të kompozimit planimetriko-volumor, ashtu edhe të trajtimit të brendshëm e të jashtëm.

Banesa nr. 1 (Tab. V).

Nga banesa e vjetër ruhet një pjesë, por gjurmët e mbetura e bëjnë të mundur rikonstrukcionin e kompozimit fillestar. Banesa ka qenë me gjysmëkat përpjendikular, me dy ambiente të banuara. (Fig. 8). Nga këto, ambienti ballor, që ka nën vetë ahurin e bagëtive, shërbente si korridor dhe quhej «shtrat». Ai paraprinte dhomën e ndenjes, përdhese, e cila quhej «kënd» dhe kryente funksionet e gatimit, të ndjenjës dhe të fjetjes. Shtrati me hyrje nga jashtë, ka një faqe muri të ndërtuar me dërrasa, në mes të së cilës është hapur një dritare e madhe, e mbrojtur nga një skarë druri dekorative. Në murin ballor është hapur edhe një dritare tjetër e vogël, me mbulesë në for-

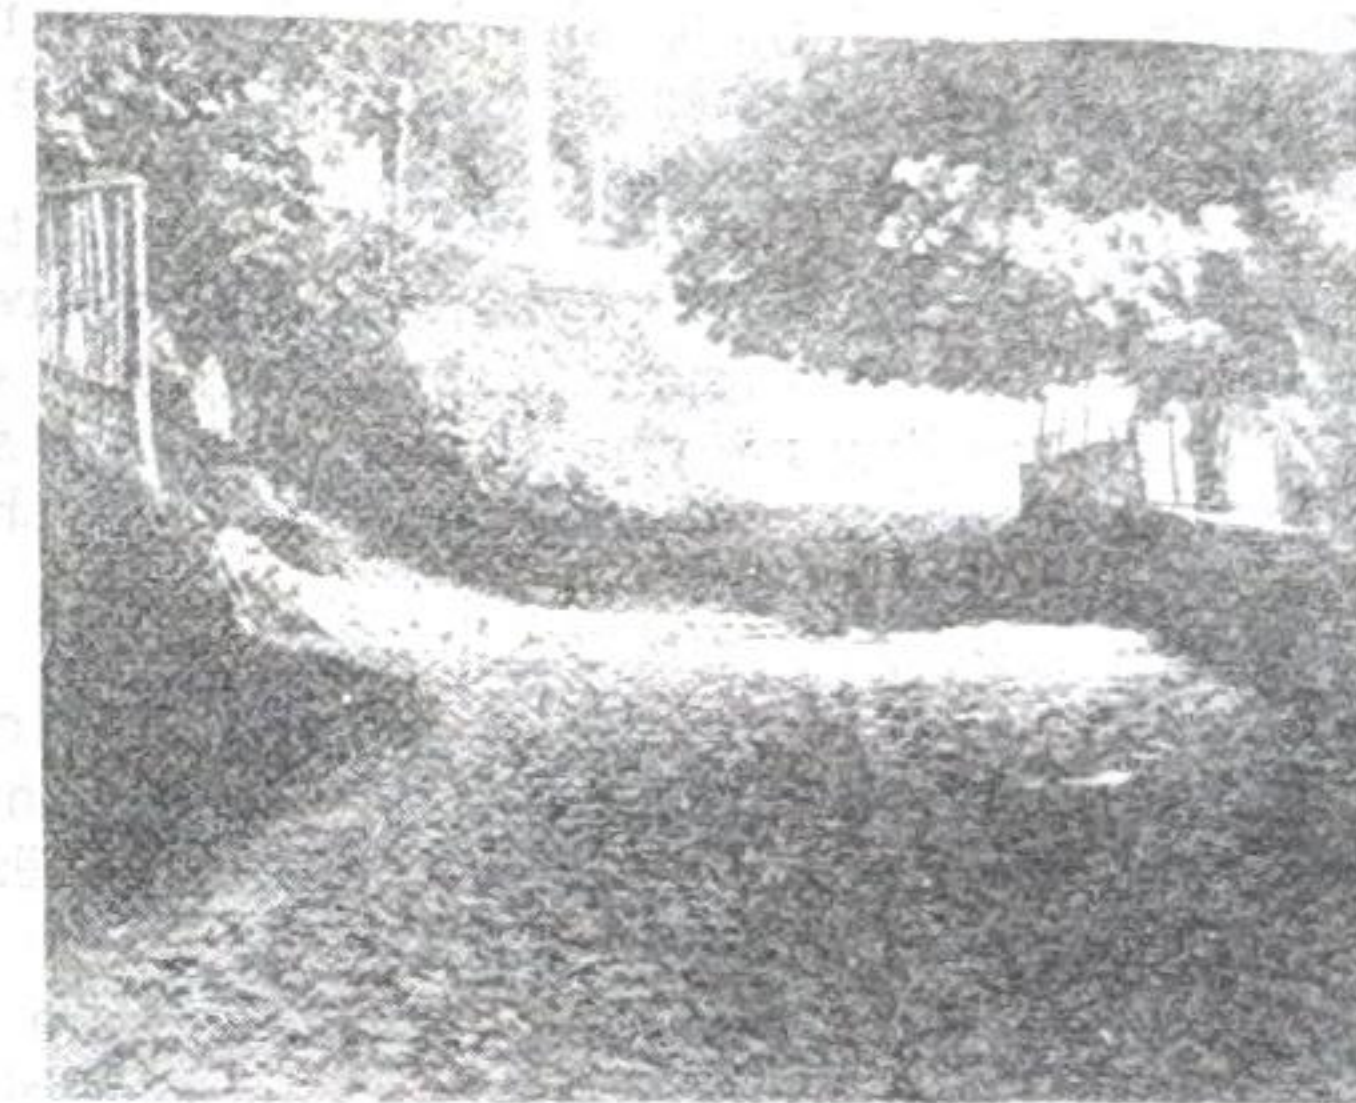


Fig. 7

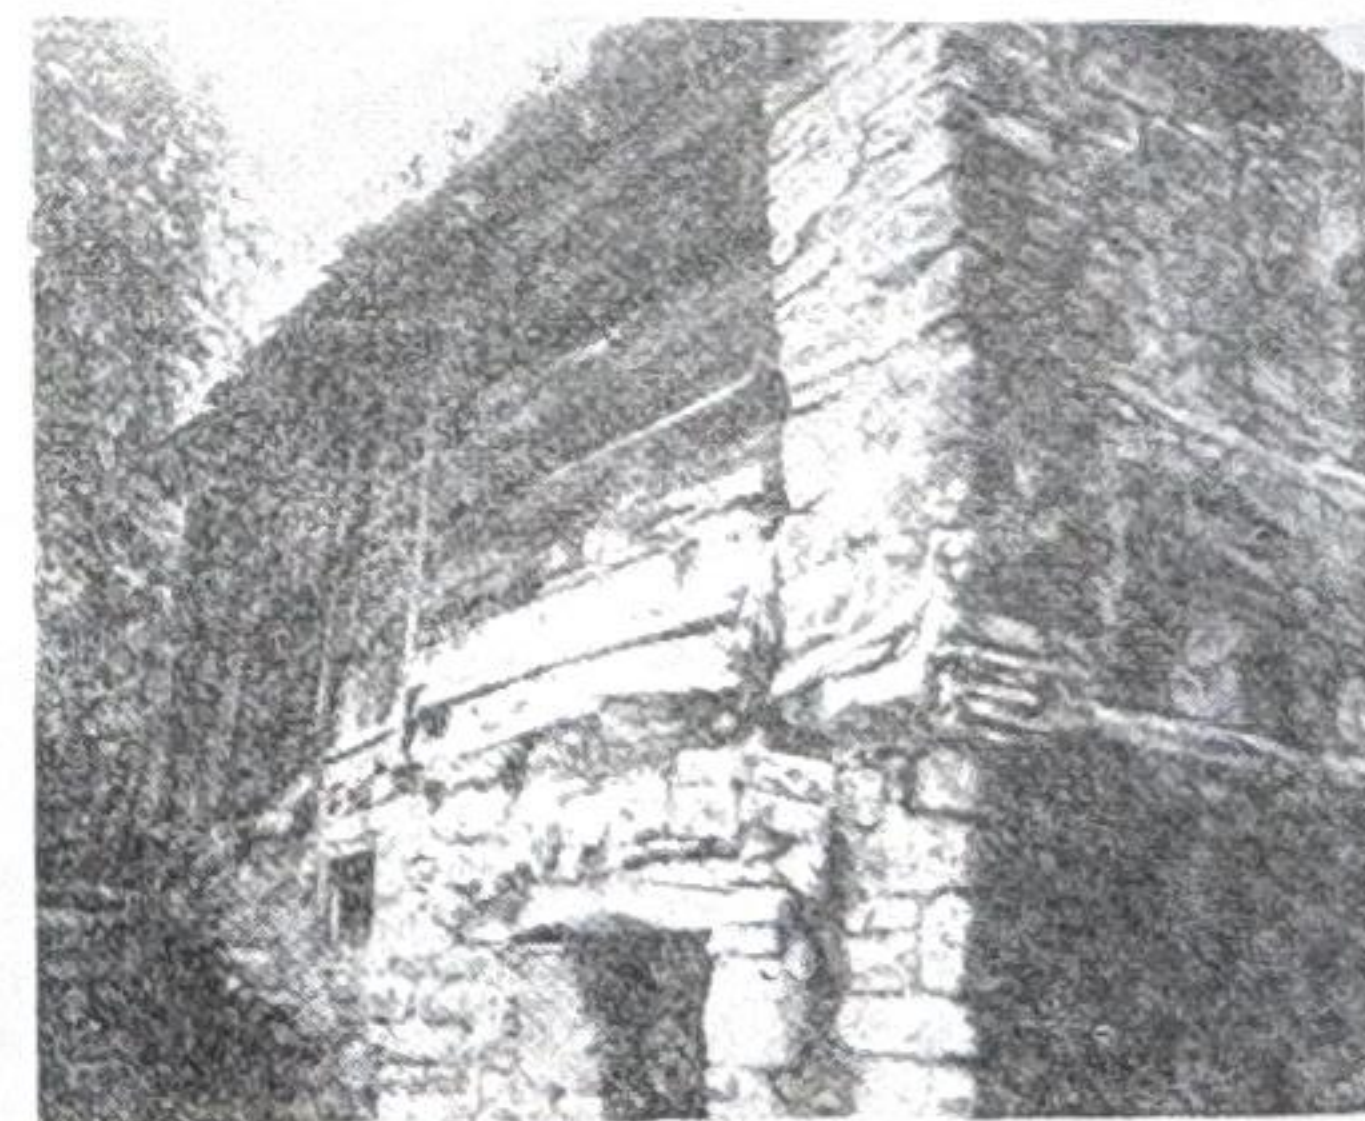


Fig. 8

më harku, e mbrojtur edhe kjo nga skarë druri. Sot ruhet vetëm pjesa dykatëshe që përmban shtratin dhe ahurin.

Banesa nr. 2. (Tab. VI). Përbëhet nga disa njësi të veçanta, të ndërtuara në kohë të ndryshme. Nga njësia e parë ka mbetur në gjendjen fillestare, me gjithë elementet e saj formuese të brendshme e të jashtme, vetëm pjesa e parë që përmban shtratin dhe ahurin. Në shtrat është ndarë një kthinë e vogël, që shërbente si dhomë pritjeje. Ajo është e shtruar me dyshe me dërrase dhe e pajisur me tavan. Oxhaku ndërmjet dy dritareve shënon ballin kryesor të dhomës. Faqja tjetër e jashtme, që sheh në oborr, është ndërtuar me skelet druri të mbushur me gurë shmerçi (lloj guri i lehtë poroz). Aty janë hapur dy dritare të mëdha, të mbrojtur me kafaze druri në formë rrjete kuadratike. Në korridorin e ngushtë dalin shkallët që e lidhin me ahurin nga brenda dhe hyrja e veçantë nga jashtë. Trajtimi i kësaj pjese shquhet për përpunimin dekorativ të elementeve të drurit, strehës së çatisë, shtyllave të skeletit, kafazit të dritareve, dollapëve të brendshëm etj.

Ambienti i dytë në vazhdim u është nënshtruar ndryshimeve të mëvonshme, të cilat kanë prekur krejt murin ballor, çatinë e tavanin, çuke tjetërsuar kështu trajtimin e brendshëm e të jashtëm, por duke ruajtur në vija të përgjithshme skemën planimetrike. Ai ka shërbyer si dhomë ndenjeje ose kënd. Dyshe me dërrase dhe të ngjeshur.

Pjesa tjetër, e cila bashkohet në një qoshe me të parën, duke formuar një kënd të drejtë, ruan një skemë të thjeshtë. Ajo është dykatëshe me nga dy ambiente: hajati i mbyllur dhe ahuri në katin përdhe dhe shtrati e këndi në katin e sipërm. E gjithë faqja që sheh nga oborri është ndërtuar me skelet druri e mbushur me shmerç.

Një skemë e tillë kompozicionale me forma të ndryshme bëhet mbizotëruese në banesat e vjetra të Dardhës. Ajo takohet e thjeshtë, si banesa e mësipërme, ose e përsëritur dy herë duke formuar banesa

vëllazërishte. Ajo merr kështu një zhvillim të mëtejshëm, duke pasur dy ambiente banimi, ose përmirësohet duke shtuar një dhomë të ndarë në shtratin e banesës.

Në banesën nr. 3 kemi të bashkëngjitura dy njësi të thjeshta dykatëshe, të ndara nga muri tërthor dhe simetrike karshi tij. (Tab. VII, fig. 9). Çdo njësi ka hyrje të veçantë në hajatet e mbyllura që paraprijnë hauret të ven-

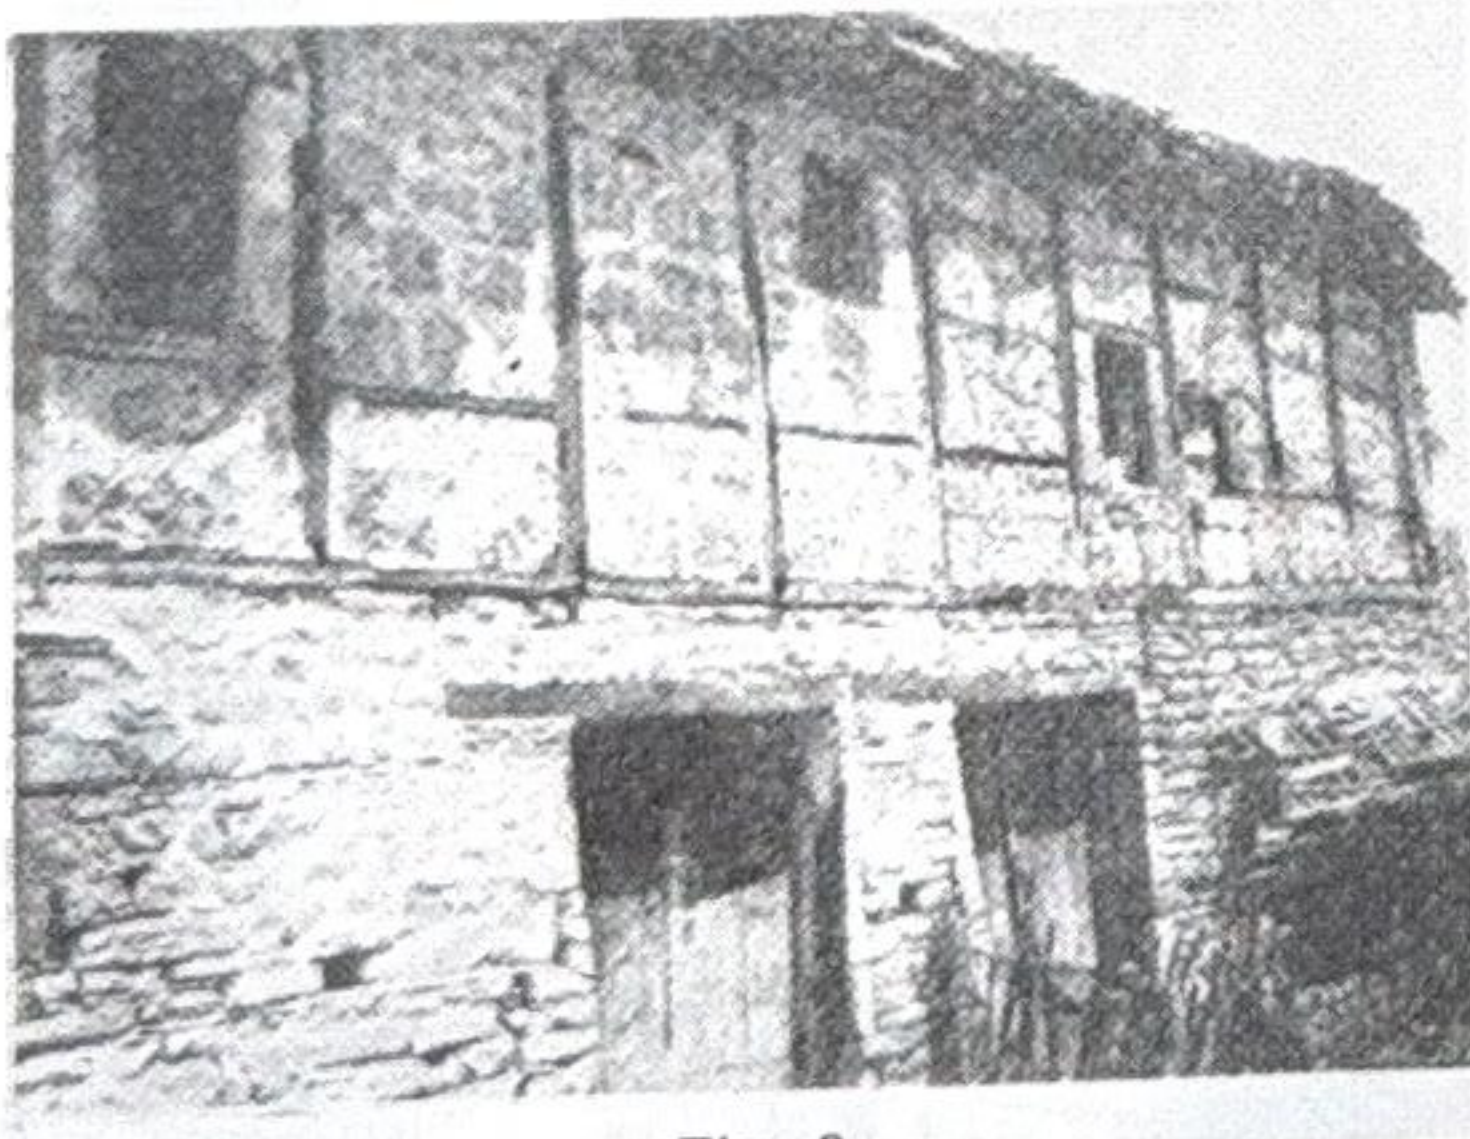


Fig. 9

dosura në pjesën e prapme të katit përdhe. Të njëjtën skemë planimetrike ka edhe kati i sipërm i shtratit në ballë të banesës dhe këndet mbrapa tyre. Shkallët e veçanta për çdo njësi janë të vendosura në hajatet dhe përfundojnë në shtratet, hapësira e të cilave mbyllet me qepen. Siç ndodh zakonisht në banesat vëllazërisht dhomat kanë komunikim ndërmjet tyre. Muri ballor i katit të dytë është i ndërtuar me skelet druri, mbushur me gurë shmerçi, ku janë hapur dritaret, të mbrojtura me kafaze druri. Në fund të shtratit të njësisë së djathtë ngrihet një platformë rreth 20 cm për të formuar aty një kënd ndenjeje. Këndet kanë përmasa të mëdha, janë të shtruar me dhe të ngjeshur dhe të pajisura me oxhakë të mëdhenj me tambur dërrase.

Në një kohë me të vonë janë bërë disa ndryshime: në hajatin e katit përdhe është ndarë një ashef, ndërsa në shtratet e katit të dytë dy kthina të vogla fjetjeje. Në gjendjen e sotme ruhet vetëm një pjesë e kësaj banese.

Një fazë më të zhvilluar paraqet **banesa nr 4** (Tab. VIII). Kati i sipërm përbëhet nga shtrati i cili shtrihet gjatë gjithë ballit dhe dy ambienteve të rrethuara, gjatë saj: këndit dhe odës. Për ndarjen e dy ambienteve shërbejnë hambarët, duke lënë edhe një derë komunikimi. Shtrati ka një pjesë të muraturës të ndërtuar me skelet. Në katin përdhe një portë e vetme të çon në hajatin e mbyllur, i cili ndërlihet me dy hauret në pjesën fundore.

Përmirësime të zgjidhjes funksionale të skemës kompozicionale, të thjeshtë dykthineshe, kemi atëherë kur në shtratin e katit të sipërm ndahet një dhomë e vogël, e cila përdoret si dhomë pritjeje.

Një shembull i kësaj faze zhvillimi është **banesa nr. 5**. (Tab. IX). Ajo përbëhet prej dy njësish të bashkëngjitura, nga të cilat ka mbetur e plotë vetëm një njësi, e cila përdoret sot si plevicë. (Fig. 10). Në katin përdhe hyrja



Fig. 10

ja përfundon në një korridor të ngushtë, ku janë vendosur shkallët prej druri për në katin e dytë. Korridori ndërlihet me dy ambiente: me ashefin përbri, që del në pamjen ballore, dhe me ahurin në pjesën fundore. Në katin e sipërm pjesa ballore, që në banesat e para zihej nga shtrati, këtu formohet nga korridori i ngushtë ndërlihet dhe oda e miqve. Këndi ka ruajtur vendin e vjetër në kompozim, d.m.th. në pjesën fundore të banesës. Me mur të hollë është ndërtuar vetëm faqja ballore e korridorit, në të cilën janë hapur dy

dritare që mbyllen me kapak dërrase. Përmirësimi i skemës kompozicionale të banesës ka sjellë dhe ndryshime në trajtimin e brendshëm të ambienteve. Ndërsa këndi mbetet si në banesat e para, d.m.th. pa tavan dhe me dysHEME të shtruar me dhe të ngjeshur, me oxhak të madh me tambur dërrase, ndërmjet dritareve e nikeve, dhoma e miqve i ka më të përpunuara elementet e brendësisë.

NJESITË DHE ELEMENTET PËRBËRËSE TË BANESES

Megjithëse shembujt e mësipërm të sjellë për ilustrim përfaqësojnë variante të një zgjidhjeje të caktuar kompozicionale, ato trajtojnë një rrugë zhvillimi të tipologjisë së banesës së vjetër dardhare. Tipizimi është një dukuri më e qëndrueshme për sa u përket elementeve të veçanta formuese të banesës, si trajtimi i jashtëm arkitektonik, pajisjet e brendshme, teknika e materialet e ndërtimit, përpunimi dekorativ i elementeve arkitektonike e dekorative etj.

Zhvillimi i vrullshëm i fshatit në periudhën pasuese, braktisja e banesave të vjetra, ose kthimi i tyre në plevica, ka bërë që sot të mos kemi mundësi të krijojmë një tablo të saktë të oborrit dhe të jetesës që kryhej në banesat e vjetra dardhare. Kështu që do të mjaftohemi me një përfytyrim të përafërt mbi këto aspekte, duke u nisur nga funksioni i ambienteve dhe nga disa prej pajisjeve të tyre të mbetura.

Pranë banesës nr. 1 ruhet ende një furrë e vjetër pjekjeje. Dëshmitë gojore na njoftojnë se furra të tilla kishte çdo familje, e cila ishte e detyruar të siguronte vetë bukën. Kjo traditë vazhdoi deri vonë, edhe mbas ndërtimit të furrave kolektive në fund të shekullit të kaluar ose në fillim të shekullit tonë, me përdorim të kufizuar: pjekje tavash, kuleçësh, lakrorësh etj. Furrat ngriheshin në oborr, jashtë volumit të banesës. Ato ishin të thjeshta dhe ndërtoheshin zakonisht nga vetë njerëzit e shtëpisë. (Tab. X/1). Hapësira e pjekjes ishte rrethore në plan dhe mbulohej me kësulë sferike, të ndërtuar me copa tjegullash. Në ballë lihej dritarja për futjen e tavës, ndërsa në mbulesë vrima për daljen e tymrave dhe nxehtësisë së tepërt, të cilat mbas ndezjes të plotë vuloseshin me baltë. Zjarri ndizej në dysHEMENË e furrës dhe mbasi formohej prushi dhe nxehej furra, futej buka ose tava për t'u pjekur.

Shfrytëzimi i katit përdhe për strehimin e bagëtive dëshmon se cila familje i mbante ato në shtëpi. Në Dardhë nuk njihej shtegtimi stinor i bagëtive. Në oborr mund të ketë pasur ndonjë plevicë për sigurimin e barit dhe të kashtës. Rezervat ushqimore të familjes janë mbajtur brenda banesës, në hambarët e drithit e të miellit, siç i shohim ende në banesën nr. 4 (Tab. X/2).

Ambientet e banimit të banesës së vjetër dardhare, të përqëndruara në katin e dytë ishin kështu të pakta. Ambienti kryesor, këndi ose dhoma e përditshme, ku gatuhej, hahej dhe flihej, kishte përmasa të mëdha, Zakonisht ato ishin pa tavan, ndërsa dysHEMEJA shtrohej me dhe të ngjeshur. Një shtresë e tillë krijonte një izolim të mirë nga erërat që vinin nga hauri në katin përdhe, kishte njëkohësisht

dhe veti të mira termoizoluese. Faqja në oxhak shënonte ballin e dhomës. Në qëndër ndërtuhej oxhaku, thuajse për të gjitha banesat e kësaj periudhe. Ato janë të pajisura me kanal tymi dhe me tymtar. (Tab. XI/1). Tym i thithej nga një tambur i gjerë cilindrik, i ndërtuar me dërrasa të punara dhe që përfundonte në pjesën e poshtme me një linjë të valëzuar. Në të dy krahët oxhaku shoqërohet nga kamaret karakteristike, të hapura ose të mbyllura dhe dritaret ose dollapët. Në muret e tjera janë hapur kamare e dollapë të tjerë. Zakonisht sipërfaqet e mureve janë të zhveshura, por në disa raste ato thyhen me fashatura dërrase, që qarkojnë pjesën e sipërme, me sergjena (polica) mbi to, për vendosjen e orendive të shtëpisë. Prania e hambarëve të mëdhenj, që zënë një faqe të tërë muri dhe me përpunimin e tyre të pasur, pasurojnë trajtimin zakonisht të thjeshtë të këndeve (banesa nr. 5).

Në krahasim me këndet, shtratet janë akoma më të thjeshta. Ato shërbejnë si sipërfaqe komunikimi, por përdoren gjithashtu edhe për kryerjen e punëve të ndryshme të ekonomisë shtëpiake, për përpunimin dhe tharjen e produkteve bujqësore, si dhe për ndenje gjatë stinëve të ngrohta. Mbyllja e hapësirës së shkallëve me kapak rriste mundësinë e shfrytëzimit të sipërfaqes.

Shtratet përgjithësisht ishin pa tavan dhe të shtruar me dysHEME dërrase, ndërsa në mure janë hapur kamare e dollapë. Shtrati ndahet nga këndi me mure të trasha guri që shkojnë deri në pjesën e sipërme të çatisë, në formë kallkani. Shpesh dera e këndit sigurohet me shul të futur në mur. Në murin ndarës lihen dritare që, përveç ndriçimit të këndit, krijojnë një lidhje më të drejtpërdrejtë ndërmjet dy ambienteve, ndërsa, në disa raste, sipërfaqja e murit qarkohet në pjesën e sipërme me fashatura dërrase, që kornizojnë gjithashtu dyert, dritaret e dollapët. Muratura e hollë e ballit të këndit, e ndërtuar me skelet druri dhe me gurë shmerçi, jep mundësinë e hapjes së dritareve të mëdha, që e bën më komod qëndrimin dhe punën në ambient, si dhe e gjallëron së tepërmi trajtimin e jashtëm të banesës.

Në banesat me skemë më të zhvilluar, dhoma e miqve, që përftohet nga ngushtimi i hapësirës së shtratit, fiton një përpunim të ri. Ajo është e shtruar me dysHEME dërrase. Mungesa e haureve në katin përdhe, e nën to, e bën të panevojshme shtresën izoluese me baltë. Tavanët bëhen me dërrasa ose me suva. Dhomat e miqve janë të pajisura me oxhakë, struktura edhe forma e të cilëve, janë të ndryshme nga ato të këndeve. Këta oxhakët janë më të vegjël, me tamburë prizmatikë, që vijnë duke u mbledhur nga sipër, të ndërtuar me strukturë çatmaje dhe të mbrojtur nga një shtresë suvaje me baltë të lyer me gëlqere. (Tab. XI/2).

Dekoracioni i brendshëm në banesat e vjetra dardhare ishte i kursyer. Ai përqëndrohej kryesisht në ato pak elemente druri të përdorur sidomos në oxhakë, dyer, dritare, kapakë, tavanë etj. Përgjithësisht ato janë të punuara me dërrasa të zdruguara dhe herë-herë të gdhendura me profile të ndryshme. Spikasin në mënyrë të veçantë dollapët e murit me kanata të gdhendura, kryesisht me motive bimore.

Teknika e ndërtimit, me materiale rrethanore, është e një cilësie të lartë. Muratura ndërtohej me gurë të lidhur me baltë dhe përforcohej me breza druri. Qoshet punoheshin me gurë të latuar, por dhe faqja e jashtme e muraturës ka prirje për një radhim të rregullt të gurëve. Faqja ballore e këndeve ndërtohet me skelet druri të mbushur me gurë shmërçi. Skeleti formohet nga shtylla vertikale druri, të përforcuara vende-vende me binarë horizontalë. Shtyllat përfundojnë me jastëkë druri, që në disa raste janë të gdhendur.

Çatia mbulohet me plloça guri. Ajo i zgjat flegelat e saj duke formuar një strehë të gjërë, e cila e mbron muraturën nga agjentët atmosferikë. Strehët më të përdorshme janë dyfishe të zbuluara. Radha e parë formohet nga zgjatimi i trerëve horizontalë të tavanit, ndërsa e dyta, nga zgjatja e binarëve të çatisë. Bishtat e strehës janë të gdhendura, ndërsa sipër tyre kalon një tra i dhëmbëzuar në pjesën që duket. (Tab. XII/1).



Fig. 11

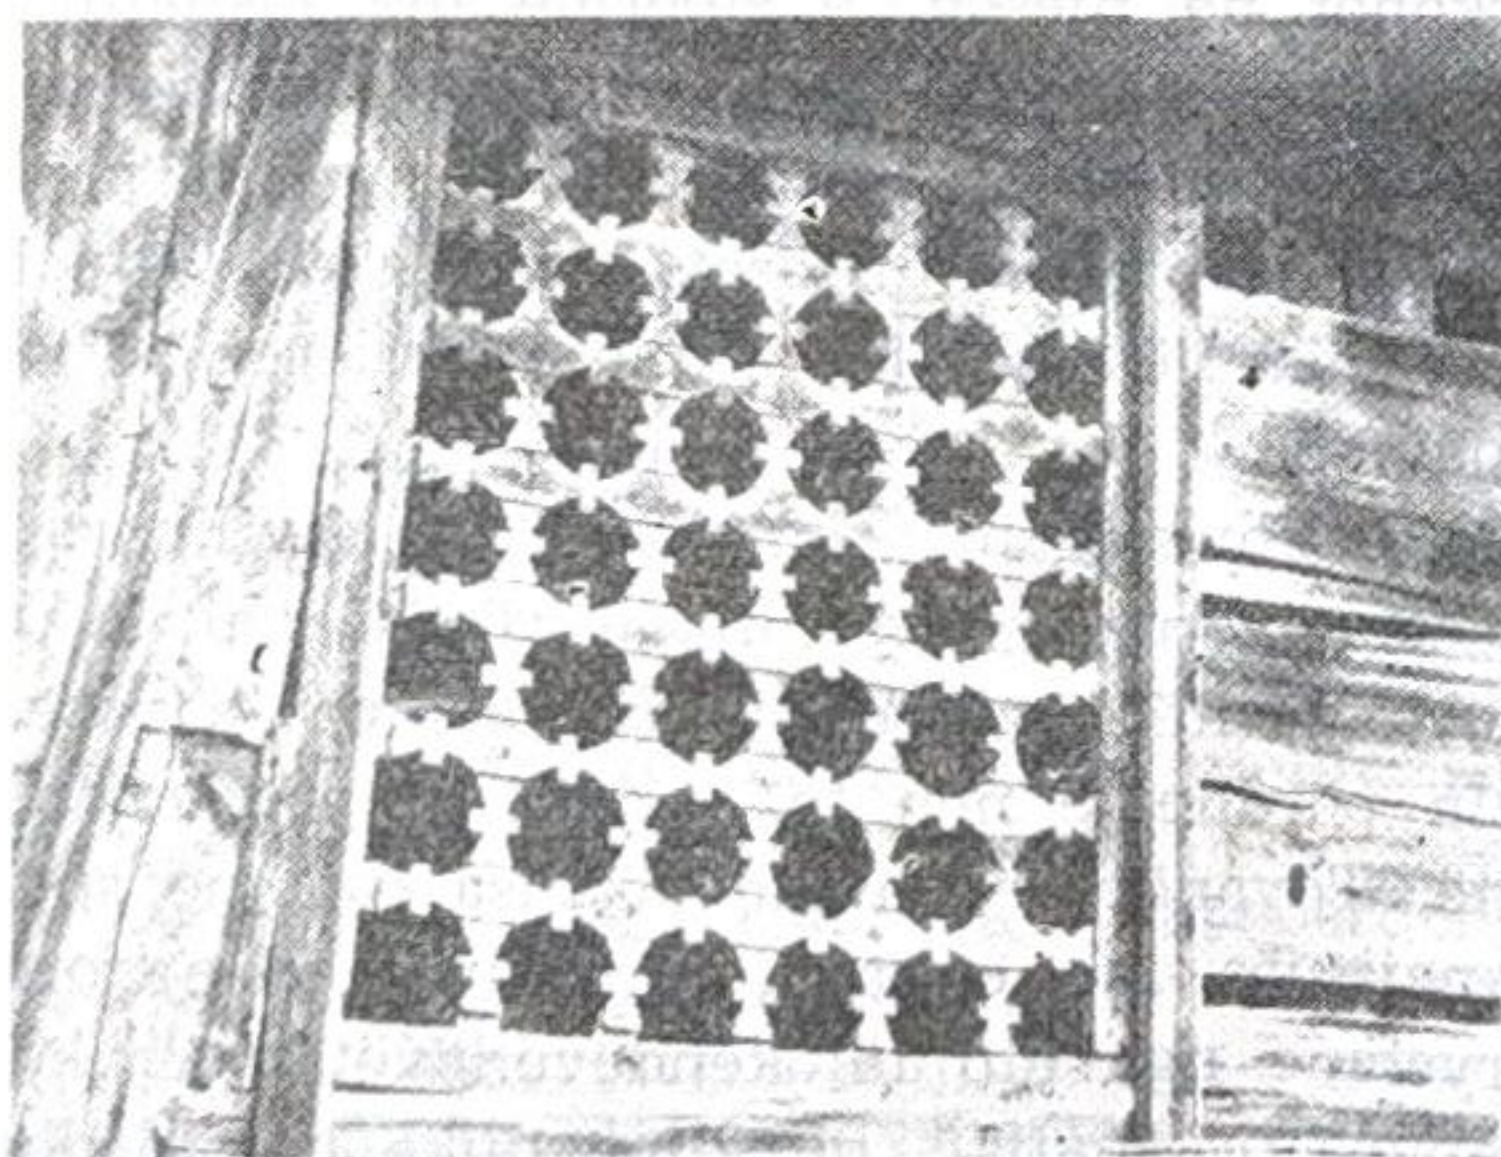


Fig. 12

Elemente shprehëse të përkujdesjes dekorative janë edhe dritaret. (Tab. XII/2). Format e tyre janë dy llojesh: me mbulesë të harkuar dhe të rrafshët. Ato nuk kanë kanatë xhami, por mbyllen me kapakë druri, ndërsa nga jashtë mbrohen me kafazë druri. Këto të fundit janë të shumëllojshme. Më të thjeshtat përbëhen nga binarë druri gjatë gjithë lartësisë ose mbrojnë vetëm pjesën e poshtme të hapësirës së dritares. Në raste të tjera binarët gdhendën (Fig. 11). Në dritaret më të mëdha zbatohet veshja e gjithë hapësirës me skara druri. Ato formohen nga kryqëzimi me kllaposje i dërrasave të gdhendura, duke formuar një rrjet me sythe rrethorë, (Fig. 12, 13) ose me shufra të holla të futura tek njëra-tjetra, që formojnë një rrjet kuadratik. Këto të fundit zakonisht përdoren në dritaret e shtretërve. Edhe te dyert ndjehet përkujdesja dekorative, e cila arrihet thjesht, thuajse në mënyrë spontane. Ato punohen me dërrasa të zdruguara, duke lënë të duken kokët e mëdha të gozhdëve të kovaçit, me të cilat mbërthehen me parvazët, si dhe elementet e tjera metalike, menteshat dhe trokitëset metalike në dyert e jashtme. (Fig. 14).

Siç shihet, trajtimi arkitektonik, ndonëse i përmbajtur, nuk mbetet i varfër. Balli i katit të sipërm, i ndërtuar me skelet druri dhe me shmërç, e lehtëson masën e plotë të muraturës së gurtë, diferencon volumet e kateve, le të nënkuptohen funksionet e ndryshme dhe krijon një karakter të lirshëm e të lehtë, i cili theksohet dhe nga përpunimi i elementeve arkitektonike e konstruktive, dritareve, strehëve, shtyllave të drurit etj.



Fig. 13

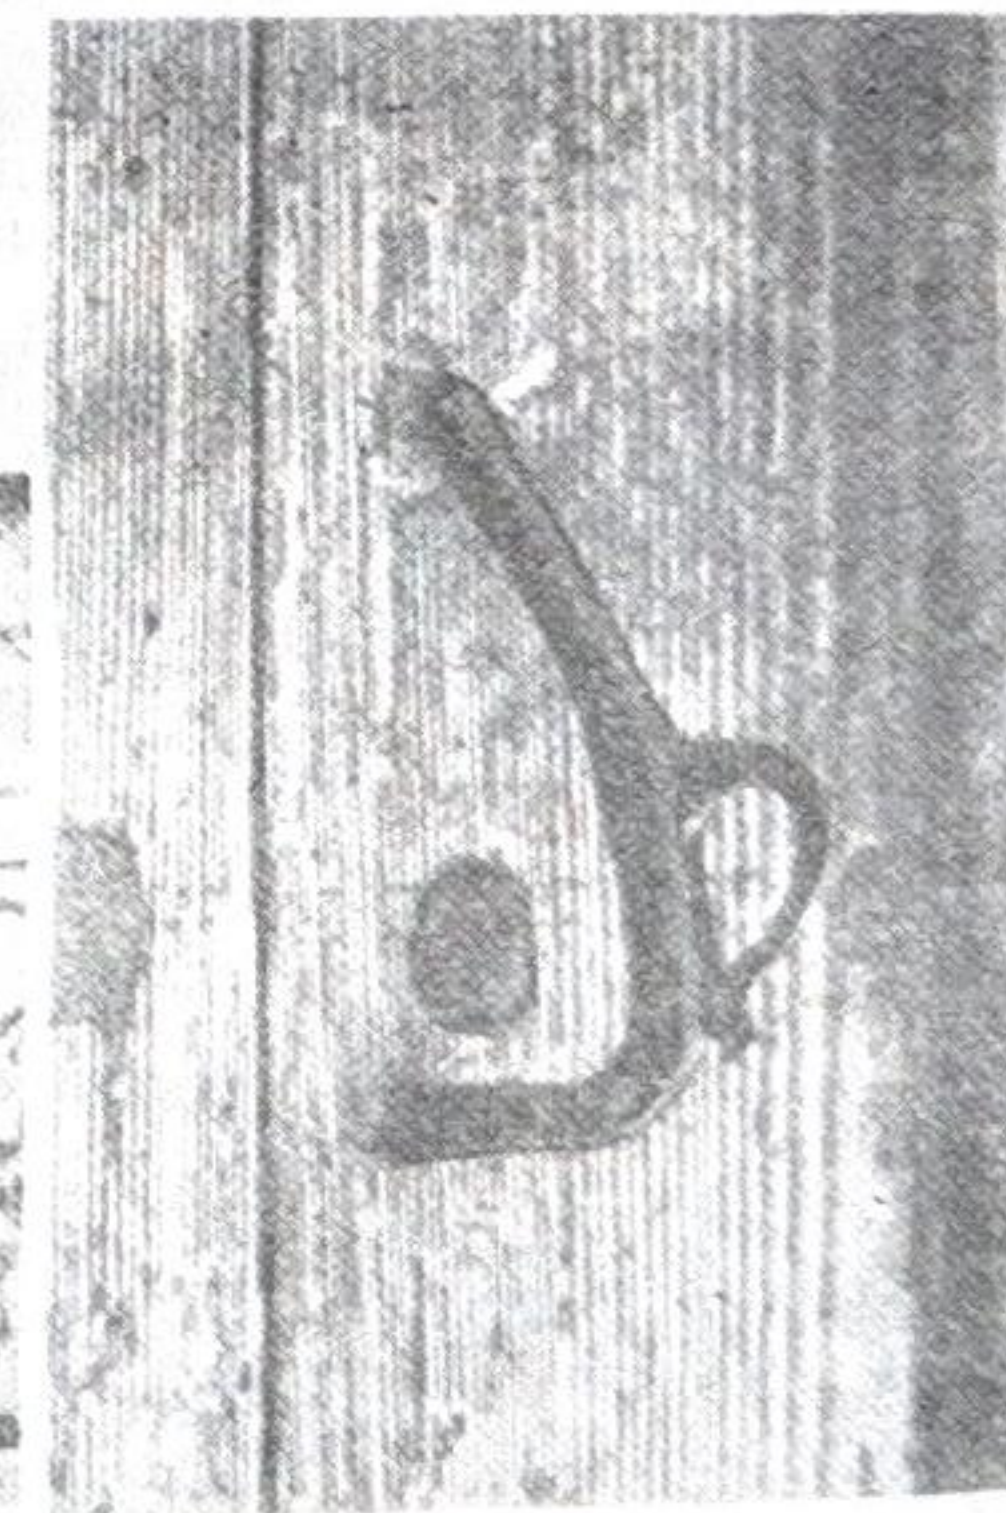


Fig. 14

BANESAT E PERIUDHËS SË DYTË.

Një numër i mirë i banesave janë të datuara, gjë që na lejon të ndjekim me saktësi zhvillimin e tipareve arkitektonike të kësaj periudhe. Uniformitetit dhe zhvillimit relativisht të ngadalshëm të banesës paraardhëse, tani i zenë vendin procese të vrullshme zhvillimi si në tipologji, ashtu edhe në trajtimin arkitektonik, dekorativ dhe teknikë ndërtimi.

Në dhjetëvjeçarët e parë të kësaj periudhe shkëputja nga format e vjetra është ende e ndrojtur. Në banesat e kësaj etape fillestare ruhen mjaft elemente, madje edhe skema kompozicionale të vjetra, ndonëse me një trajtim të ri arkitektonik dhe të zbatuara me një teknikë ndërtimit të re.

Banasa nr. 6 — E ndërtuar në vitin 1860, paraqet një zhvillim të mëtejshëm të skemës së

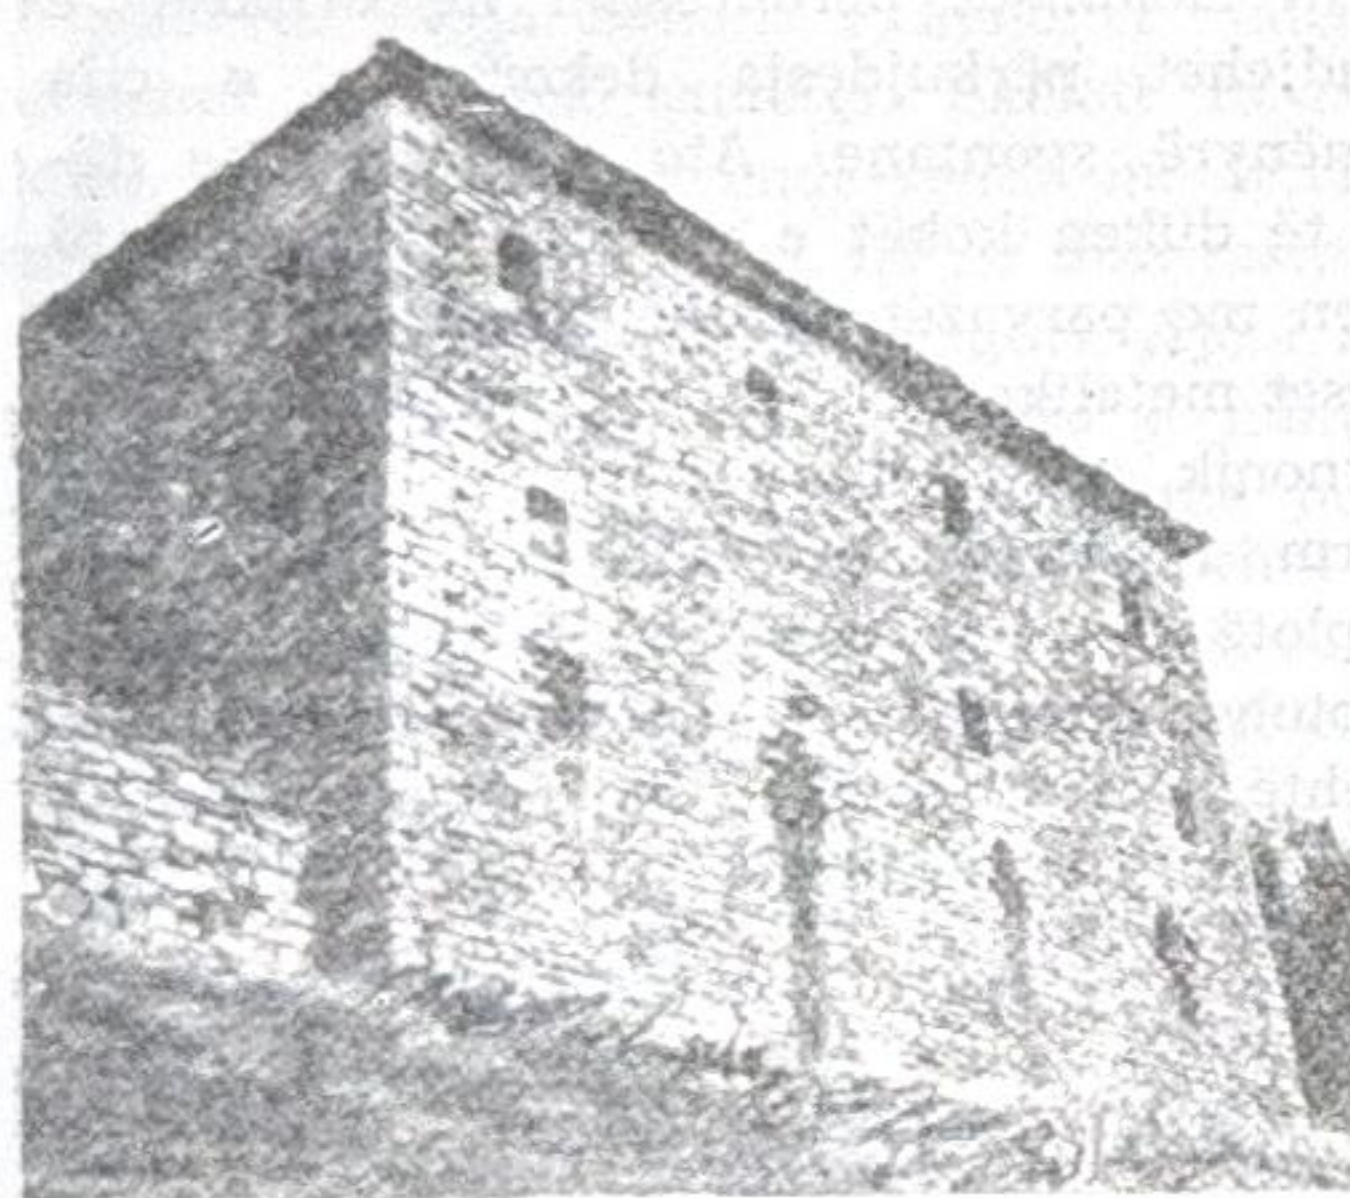


Fig. 15

kompozicionale. (Tab. XIII). Ngrihet në skajin veriperëndimor të fshatit, në një terren mjaft të pjerrët, që ka kushtëzuar ndërtimin e saj të shkallëzuar: njëkatëshe në pjesën e poshtme dhe dykatëshe në pjesën e sipërme. Hyrja kryesore nga pjesa e sipërme, nëpërmjet një tremeje të hapur në katin e dytë, përfundon me një korridor të ngushtë, që ndërlidh katër mjedise banimi me përmasa të mëdha. Katet e poshtme shërbenin si katoje dhe haure.

Përmasat e mëdha, lartësia e madhe, sidomos në krahun e poshtëm, dritaret e vogla dhe muratura e gurtë, e pathyer me elemente arkitektonike e dekorative, që kanë krijuar një vëllim të mbyllur, janë karakteristikat e trajtimit të jashtëm. (Fig. 15).

Një vëllim arkitektonik të njëjtë ka edhe **banesa nr. 7**, e datuar në vitin 1867, në afërsi të së parës, që së bashku, nga kjo anë krijojnë një pamje imponuese në hyrje të fshatit. (Fig. 16). E ndërtu-



Fig. 16

ar në terren të pjerrët, banesa del me 4 kate në anën e poshtme dhe tre kate në të sipërmen. (Tab. XIV/1). Përbëhet prej dy njësisë të bashkëngjitura dhe simetrike ndaj murit ndarës tërthor, secila me hyrje të veçantë. Skema planimetrike përsëritet me besnikëri atë të banesës së zhvilluar të periudhës paraardhëse. Hyrjet në katin e dytë përfundojnë në korridoret e ngushta që komunikojnë me dy ambiente të përdorura si dhoma ndenjeje dhe gatimi. Ato përmbajnë bllokun fundor, i cili përbëhet nga hyrjet për në dhomë, hambaret e drithit e të miellit, së bashku me magjen dhe musandrat. Me shkallë të thjeshta druri, hapësira e të cilave mbulohet me kapak, zbritet nga çdo dhomë e katit të parë në qilaret, të cilët përdoren për depozitimin e drurëve dhe zahireve. Qilarët kanë edhe hyrje të veçanta nga jashtë. Ato komunikojnë ndërmjet tyre, janë të shtruara me plloça guri dhe kanë ndriçim të pakët. Poshtë tyre, nga ana e pjerrësisë së terrenit, janë hapur edhe dy qilare të tjera, të errëta dhe të freskëta, që lozin rolin e «frigoriferëve» natyralë për ruajtjen për një kohë të gjatë të produkteve ushqimore.

Kati i sipërm i banesës përdoret kryesisht për pritje. Ai ka të njëjtën skemë me katin e dytë. Dhoma e madhe është e pajisur me oxhak, dritare të mëdha e dollapë muri, ndërsa pjesa e sipërme e murit fundor është e veshur me një fashaturë dërrase, sipër të cilës janë vendosur sergjenë (polica), që shërbejnë për varjen e rrobave. Dhoma e vogël përbri korridorit ka trajtim më të thjeshtë, ndonëse ka të njëjtët elementë si të dhomës së madhe. Nga korridori dilet në ballkonet që dalin mbi hyrjet e banesës.

Përveç skemës planimetrike banesa ruan edhe shumë elemente, si oxhakët e musandrat me hambarët, të përpunuara në të njëjtën mënyrë si në shembujt e vjetër. (Tab. XIV/2). Në elemente të tjera fillon një trajtim i ri. Dritaret dhe dollapët e murit janë të qarkuara me fashatura dërrase, nga të cilat ajo e kreut është më e gjerë dhe përfundon me një kornizë të profiluar. Trajtimi i tyre, fashaturat që qarkojnë sipërfaqet e mureve, shkallët që lidhin katet e banuara etj. na kujtojnë pajimin e brendive të dhomave të Korçës dhe të qyteteve të tjera të kësaj periudhe. Përmirësime u sollën në teknikën e ndërtimit dhe, në mënyrë të veçantë, në zgjidhjen funksionale. Bagëtitë nuk strehohen më në volumin e banesës, por në plevicën jashtë shtëpisë, e cila dikur ka qenë banesa e vjetër e familjes.

Por ndërkohë, njëkohësisht me përdorimin e skemave kompozicionale të vjetra vihen re përpjekje për futjen e një tipologjie të re. Këto përpjekje janë ende të paformuara në **banesën nr. 8**, e ndërtuar në vitin 1861. Këtu prirja për zbatimin e një skeme të re planimetrike është e veshur me elemente të trajtimit të vjetër, si p.sh., balli i katit të sipërm i ndërtuar me mur të hollë prej shmërçi. (Tab. XV. Fig. 17).

Banasa nr. 9, e ndërtuar në vitin 1864 paraqet jo vetëm një zgjidhje të re, por dhe të zhvilluar kompozicionale. (Tab. XVI). Banasa përshkohet tej për tej, në pjesën qendrore, nga një korridor gjatësor, me hyrje në të dy skajet e tij. Në të dy krahët e korridorit janë vendosur dy ambiente. Në katin përdhe, ato përdoren si ashef, qilare, ndërsa i katërti, me hyrje të veçantë nga jashtë, si haur. Në katin e dytë të katërt ambientet kanë trajtim thuajse të njëjtë. Ato janë të shtruara me dysHEME dërrase, kanë tavane të suvatuara dhe janë të pajisura me oxhakë. Traj-

timi i jashtëm ka tipare të ngjashme me banesat e mësipërme: ai është tepër i kursyer, me elemente të pakta arkitektonike, me një formë



Fig. 17

prizmatike, ku mbizotëron masa e mbyllur e muraturës së gurtë. (Fig. 18).

Shkallë-shkallë, kristalizohet dhe fiton përhapje të gjerë tipi i ri i banesës. **Banesa nr. 10**, e datuar në vitin 1867, përfaqëson një variant të thjeshtë të tipit të ri (Tab. XVII). Ajo është dykatëshe, me një skemë simetrike, ku theksohet në mënyrë të veçantë pjesa qendrore, në këtë rast e dalë jashtë (Fig. 19). Salloni qendror ose siç thirret në popull «tremja», e shtruar me plloça guri, ka në çdo krah një ambient.



Fig. 18



Fig. 19

Njëri përdoret si kuzhinë ose «sobë», ndërsa i dyti si qilar. Soba është e shtruar me dërrasa, e pajisur me oxhak, ndërmjet dy dritareve që dalin në ballë dhe me musandër në pjesën fundore, në formë kthine të ndarë nga hapësira e dhomës.

Në katin e dytë anash sallonit ose «sallës» është vendosur dhoma e ndenjse, «këndi» dhe «oda». Këndi është i shtruar me baltë të ngjeshur, pa tavan dhe i pajisur me oxhak. Oda, e cila shërbente edhe si dhomë pritjeje, ka dysheme dërrase e tavan suvaje, ndërsa në pjesën fundore musandra. Në pjesën ballore të sallës, poshtë dritareve që shohin në oborr, ngrihet një minder ose kënde për ndenje. Balli i sallës është ndërtuar me mur të hollë shmerçi.

Skema simetrike me theksin qendror, e njohur dhe e përhapur gjerësisht në qytetin e Korçës dhe në fshatra të tjera të rrethit, gjatë kësaj periudhe u bë në Dardhë tipi më mbizotërues, duke arritur në fund të shekullit të kaluar realizime arkitektonike të shënuara.

Banesa nr. 11, e ndërtuar në vitin 1883, ka një kompozim të zhvilluar. (Fig. 20). Ajo është dykatëshe, por meqë është ndërtuar në terren të pjerrët, krahu i djathtë del trekatësh. Ambientet e përfutuara në këtë mënyrë janë përdorur si dyqane. Ndërtimi i banesave me dyqane



Fig. 20

është një dukuri e përhapur në Dardhë, e filluar të paktën që në vitin 1871, kur kemi banesën më të vjetër të datuar, me dyqane në gjithë katin përdhe. (Fig. 20).

Banesa ka pjesën qendrore të futur, ku është vendosur hyrja, e mbrojtur nga vazhdimi i çatisë. Në çdo anë të korridoreve qendrore dalin nga dy ambiente. Me përpunimin e kujdesshëm, volumin dhe ngritjen në lartësi (trekatëshe nga ana e rrugës), ajo spikat në grumbullin e banesave përreth.

Banesa nr. 12, e ndërtuar në vitin 1883, është një shembull tjetër i zhvilluar. (Fig. 21). Ajo ngrihet trekatëshe në terren të pjerrët dhe ka nga një ambient në çdo krah të korridoreve qendrore. Kati përdhe, pjesërisht i futur në truall, përdoret për qilar, në katin e dytë janë dhomat e ndenjes, ndërsa në të tretin dhoma e pritjes dhe një dhomë gjumi. Pjesa qendrore është e futur në dy katet e poshtme, e mbuluar me qemer cilindrik, që mban muraturën e katit të tretë dhe një ballkon të dalë, i cili përkryen edhe më tepër theksimin qendror të banesës.



Fig. 21

Krahas skemës kompozicionale, gjatë periudhës së dytë, një zhvillim të mëtejshëm merr teknika e ndërtimit dhe ndryshon koncepti dekorativ. Muratura ndërtohet me gurë, brezat e drurit, edhe kur përdoren, nuk janë të dukshëm në sipërfaqen e jashtme të muraturës. Si lidhës përdoret balta në pjesën e brendshme të muraturës, ndërsa fugaturat mbrohen nga një shtresë llaçi gëlqereje. Në banesat e zhvilluara përdoret gjerësisht llaçi i gëlqeres si lidhës i muraturës. Elementet e drunjtë zhduken krejtësisht në pamjet e jashtme. Një vend gjithnjë e më të madh ze përdorimi i detajeve prej guri të gdhendur, me të cilët vishen shpatullat e dyerve të dritareve dhe ndërtohen mbulesat e harkuara të tyre. Shpesh këto të fundit lozin rolin e harqeve shkarkuese, nën të cilët vendosen arkitrarrë druri ose mbushje me muraturë, për të krijuar një konfiguracion të rrafshët të hapësirave.

Përpunimi dekorativ përqendrohet në gdhendjet në relief. Ato zbatohen kryesisht në mbimbulesat e portave dhe në qoshet e muraturës. Motivet më të përdorshme janë të nxjerra nga bota shtazore, si shqiponja, demi, qeni etj., por nuk mungojnë edhe portretet njerëzore dhe motivet bimore. Një motiv tjetër i pëlqyer është ai i diellit dhe i hënës. Në banesën nr. 12 motivi i diellit është konceptuar si një portret njeriu përballë, i rrethuar me rreze, ndërsa i hënës në formën e harkut të hënës me profil njerëzor, i qarkuar me rreze më të shkurtra. (Tab. XVIII).

BANESAT E PERIUDHËS SË TRETË

Tipologjia e re e banesës, e fiksuar gjatë periudhës së dytë, pati qëndrueshmëri dhe vazhdoi të ruhet edhe gjatë periudhës së tretë. Por, meqenëse tiparet e saj kryesore ishin tashmë të formuara, në periudhën e tretë ajo iu nënshtrua përpunimeve të formës dhe të teknikës, duke na dhënë një numër variantesh nga më të ndryshmet. (Tab. XIX). Në bazë të përpunimit arkitektonik qëndron gjithnjë theksimi i pjesës qendrore. Zhvillimi planimetrik mund të jetë simetrik, me ambiente të vendosura në të dy krahët e korridorit qendror, ose kjo skemë thyhet me daljen e një krahu përpara, duke fituar formën e shkronjës L. Skema kompozicionale mund të jetë e thjeshtë ose e përbërë, nga një ambient deri në tre të tillë të vendosur në çdo krah të korridorit qendror, ndërsa numri i kateve luhetet nga një në dy, shpesh duke pasur dhe bodrume ose qilare që dalin mbi nivelin e truallit. Pjesa qendrore formulohet e futur, e dalë ose e rrafshët dhe e gjallëruar me erkera ose ballkone të hapur, të rrethuara me parapete hekuri të punuar. Një nivel të lartë arrin teknika e punimit me elemente të shumta guri të gdhendur. Brenditë e dhomave çlirohen edhe nga orëditë e pakta fikse dhe oxhakët dhe pajisen tashmë me mobilje e stufa. Banesat e reja të Dardhës fitojnë kështu një aspekt gjithnjë e më të afërt me banesat qytetare.

Shtresimi i ndërtimeve të Dardhës, tiparet arkitektonike të tyre ecuria e zhvillimit dhe e zëvendësimit të tipeve të banesës, janë një pasqyrë besnike e gjithë etapave që përshkoi historia e fshatit.

Duke e filluar jetën si një vendbanim i përkohshëm blegtor, ndonëse në kushte të disfavourshme ekonomike, por me një mbrojtje të mirë natyrore, i struktur thellë në male, larg shfrytëzimit feudal, kushte që çmoheshin në periudha pasigurie nga fshatarësia e lirë, ai mundi të çajë rrugë drejt zhvillimit dhe të fuqizohet nga periudha në periudhë.

Ndërtimet e periudhës së parë dëshmojnë për një stad ende të ulët zhvillimi. Ato i përgjigjen një programi të varfër. Strehimi i bagëtive brenda ndërtesës, numri i paktë i ambienteve të banimit, përmasat e tyre të mëdha dhe shfrytëzimi i tyre me disa funksione, nevoja për ambiente pune të përditshme kushtëzuan parapëlqimin për tipa banesash me një skemë të thjeshtë, të njohur dhe të përhapur gjerësisht edhe në krahina të tjera të vendit, por me formulim arkitektonik specifik. Pasuria me pyje e zonës dhe aftësia e dardharëve në përpunimin e lëndës së drurit ishin të vetmet mundësi që mund të përdorehin në përpunimin dekorativ të banesës.

Periudha e dytë, që përfshin gjysmën e dytë të shek. XIX, shënon një kthesë në zhvillimin e fshatit. Proceset e reja që po ndodhnin në jetën ekonomike të vendit fillojnë të ndjehen qysh herët në Dardhë, e cila fitoi një karakter të ri ekonomiko-shoqëror. Dardha u bë një qendër e rëndësishme e prodhimit dhe e shërbimit zejtar dhe e shkëmbimit të mallrave si një stacion i afërt, ku fshatrat përreth plotësonin kërkesat

e tyre imediate, pa pasur nevojë të zbrisnin në tregjet e qyteteve të zonës (Korçë, Kostur etj.). Në fshat funksiononin një numër i madh zejtarësh, dyqanesh e banesash. Fshati kishte fituar njëkohësisht një shtrirje të gjerë, ishte rritur popullsia e tij, e cila në vitet 1880-90 arrinte deri më 1454 frymë². Ai ishte pra një nga fshatrat më të mëdhenj të gjithë rrethit të Korçës dhe kishte një fizionomi urbanistike të formuar, si një vendbanim i mbledhur, i ngjeshur me ndërtime, me rrjet rrugor të shtrirë në gjithë fshatin dhe një furnizim të rregullt me ujë të pijshëm, siç dëshmojnë datat e çezmave (1876, 1880 etj.).

Karakteri i ri i fshatit i bënte të papranueshme banesat e vjetra dhe shkallë-shkallë po fitonte në terren përhapja e tipave të rinj të banesës. Banesa e re dallohet nga e vjetra dhe nga gjerësia e programit, nga përmirësimet e zgjidhjes funksionale dhe nga karakteri i ri i trajtimit arkitektoniko-dekorativ, që plotëson më mirë kërkesat për një jetë komode e më të qytetëruar. Kështu dhe fshati i Dardhës u përfshi në proceset e rëndësishme që u ndjenë në mbarë arkitekturën popullore dhe që karakterizohen nga futja e tipave të rinj të banesave dhe prirjet e theksuara konvergjente, më të spikatur kjo në Shqipërinë e Jugut. Banesa të ngjashme me ato të periudhës së dytë të Dardhës, pavarësisht nga shkalla e përpunimit arkitektonik dekorativ, takohen gjatë kësaj periudhe dhe në fshatra të tjera të trevës së Korçës, por dhe të krahinave të tjera të vendit.

Shekulli XX e gjeti fshatin me një fizionomi arkitektoniko-urbanistike të formuar, kështu që ai nuk pati barrën e shndërrimit dhe të formimit të një karakteri të ri, që e kishte mbajtur periudha e dytë. Megjithatë periudha e tretë solli përmirësime të dukshme të këtij karakteri dhe e pasuroi më tepër atë, duke e sjellë në gjendjen që e gjejmë sot dhe duke i përforcuar tiparet qytetare.

Në ditët tona, me fuqizimin e qendrave të tjera me kushte më të favorshme ekonomike e të çliruara nga ndrydhja e shfrytëzimit bejloro-çifligar, me përhapjen uniforme dhe të rregullt në çdo fshat të shërbimeve e të tregtisë dhe të sistemit arsimor, kulturor e shëndetësor, fshati i Dardhës e humbi rëndësinë e dikurshme në jetën ekonomike dhe shoqërore të krahinës. Falë klimës dhe bukurive natyrore ai u kthye në një qendër të frekuentueshme kurative pushimi. Krahas ndërtimeve të reja moderne, të ngritura vitet e fundit për pushimin e punonjësve, shfrytëzohen edhe disa nga banesat e vjetra, që, me ndërtimin dhe ambientet komode, e kryejnë më së miri këtë funksion të ri.

2) Karmici — *Gjeografia e Korçës dhe e rrethit*, Selanik, 1888, f. 40. (Përkthim në Arkivin e Inst. të Historisë)

THE URBAN AND ARCHITECTONIC CHARACTERISTICS OF THE VILLAGE OF DARDHA — KORÇA DISTRICT

The village of Dardha has an interest for the student not only because of its architectonic values, but also because it represents a typical way of development of the Albanian village during a period that is characterized by the emergence and spread of the capitalist relations.

As a result of the historical road of development, the constructions in Dardha are divided into three main periods. The first period begins from the founding of the settlement (about the 17th century) to the middle of the 19th century. During this period, Dardha had the character of a secure settlement, nested among the mountains, populated by families that had come from neighbouring villages. Its inhabitants were engaged mainly in livestock-raising but they would pick up seasonal work as sawers, chiefly outside the village. The buildings of this period respond to a limited range of requests. The main typological characteristics of the dwelling was determined by the need for keeping the livestock within the dwelling, the limited living milieus, their large sizes and their multi-functional character.

The second period, from the second half of the 19th century, marks a turning-point in the development of the countryside. Dardha became an important centre of production and craftsmanship. In the village there were a great number of craftsmen, shops and inns. The population increased, the village extended and had an irrigation network over the entire area, and was regularly supplied with drinking water. The new requirements conditioned the introduction of a new type of dwelling which was distinguished from the previous one by the extension of its programme, the improvement of the functional solution and the new type of the architectonic-decorative treatment.

In the 20th century, that is, the third period of its development, the village had an established architectonic-urban physiognomy. Nevertheless, this period brought about other improvements and further enriched its character.

In our times, despite the rising power of other centres of the region, the village of Dardha played its former economic and social importance. With its climate and beautiful natural scenery, it has been turned into a curative and resort centre.



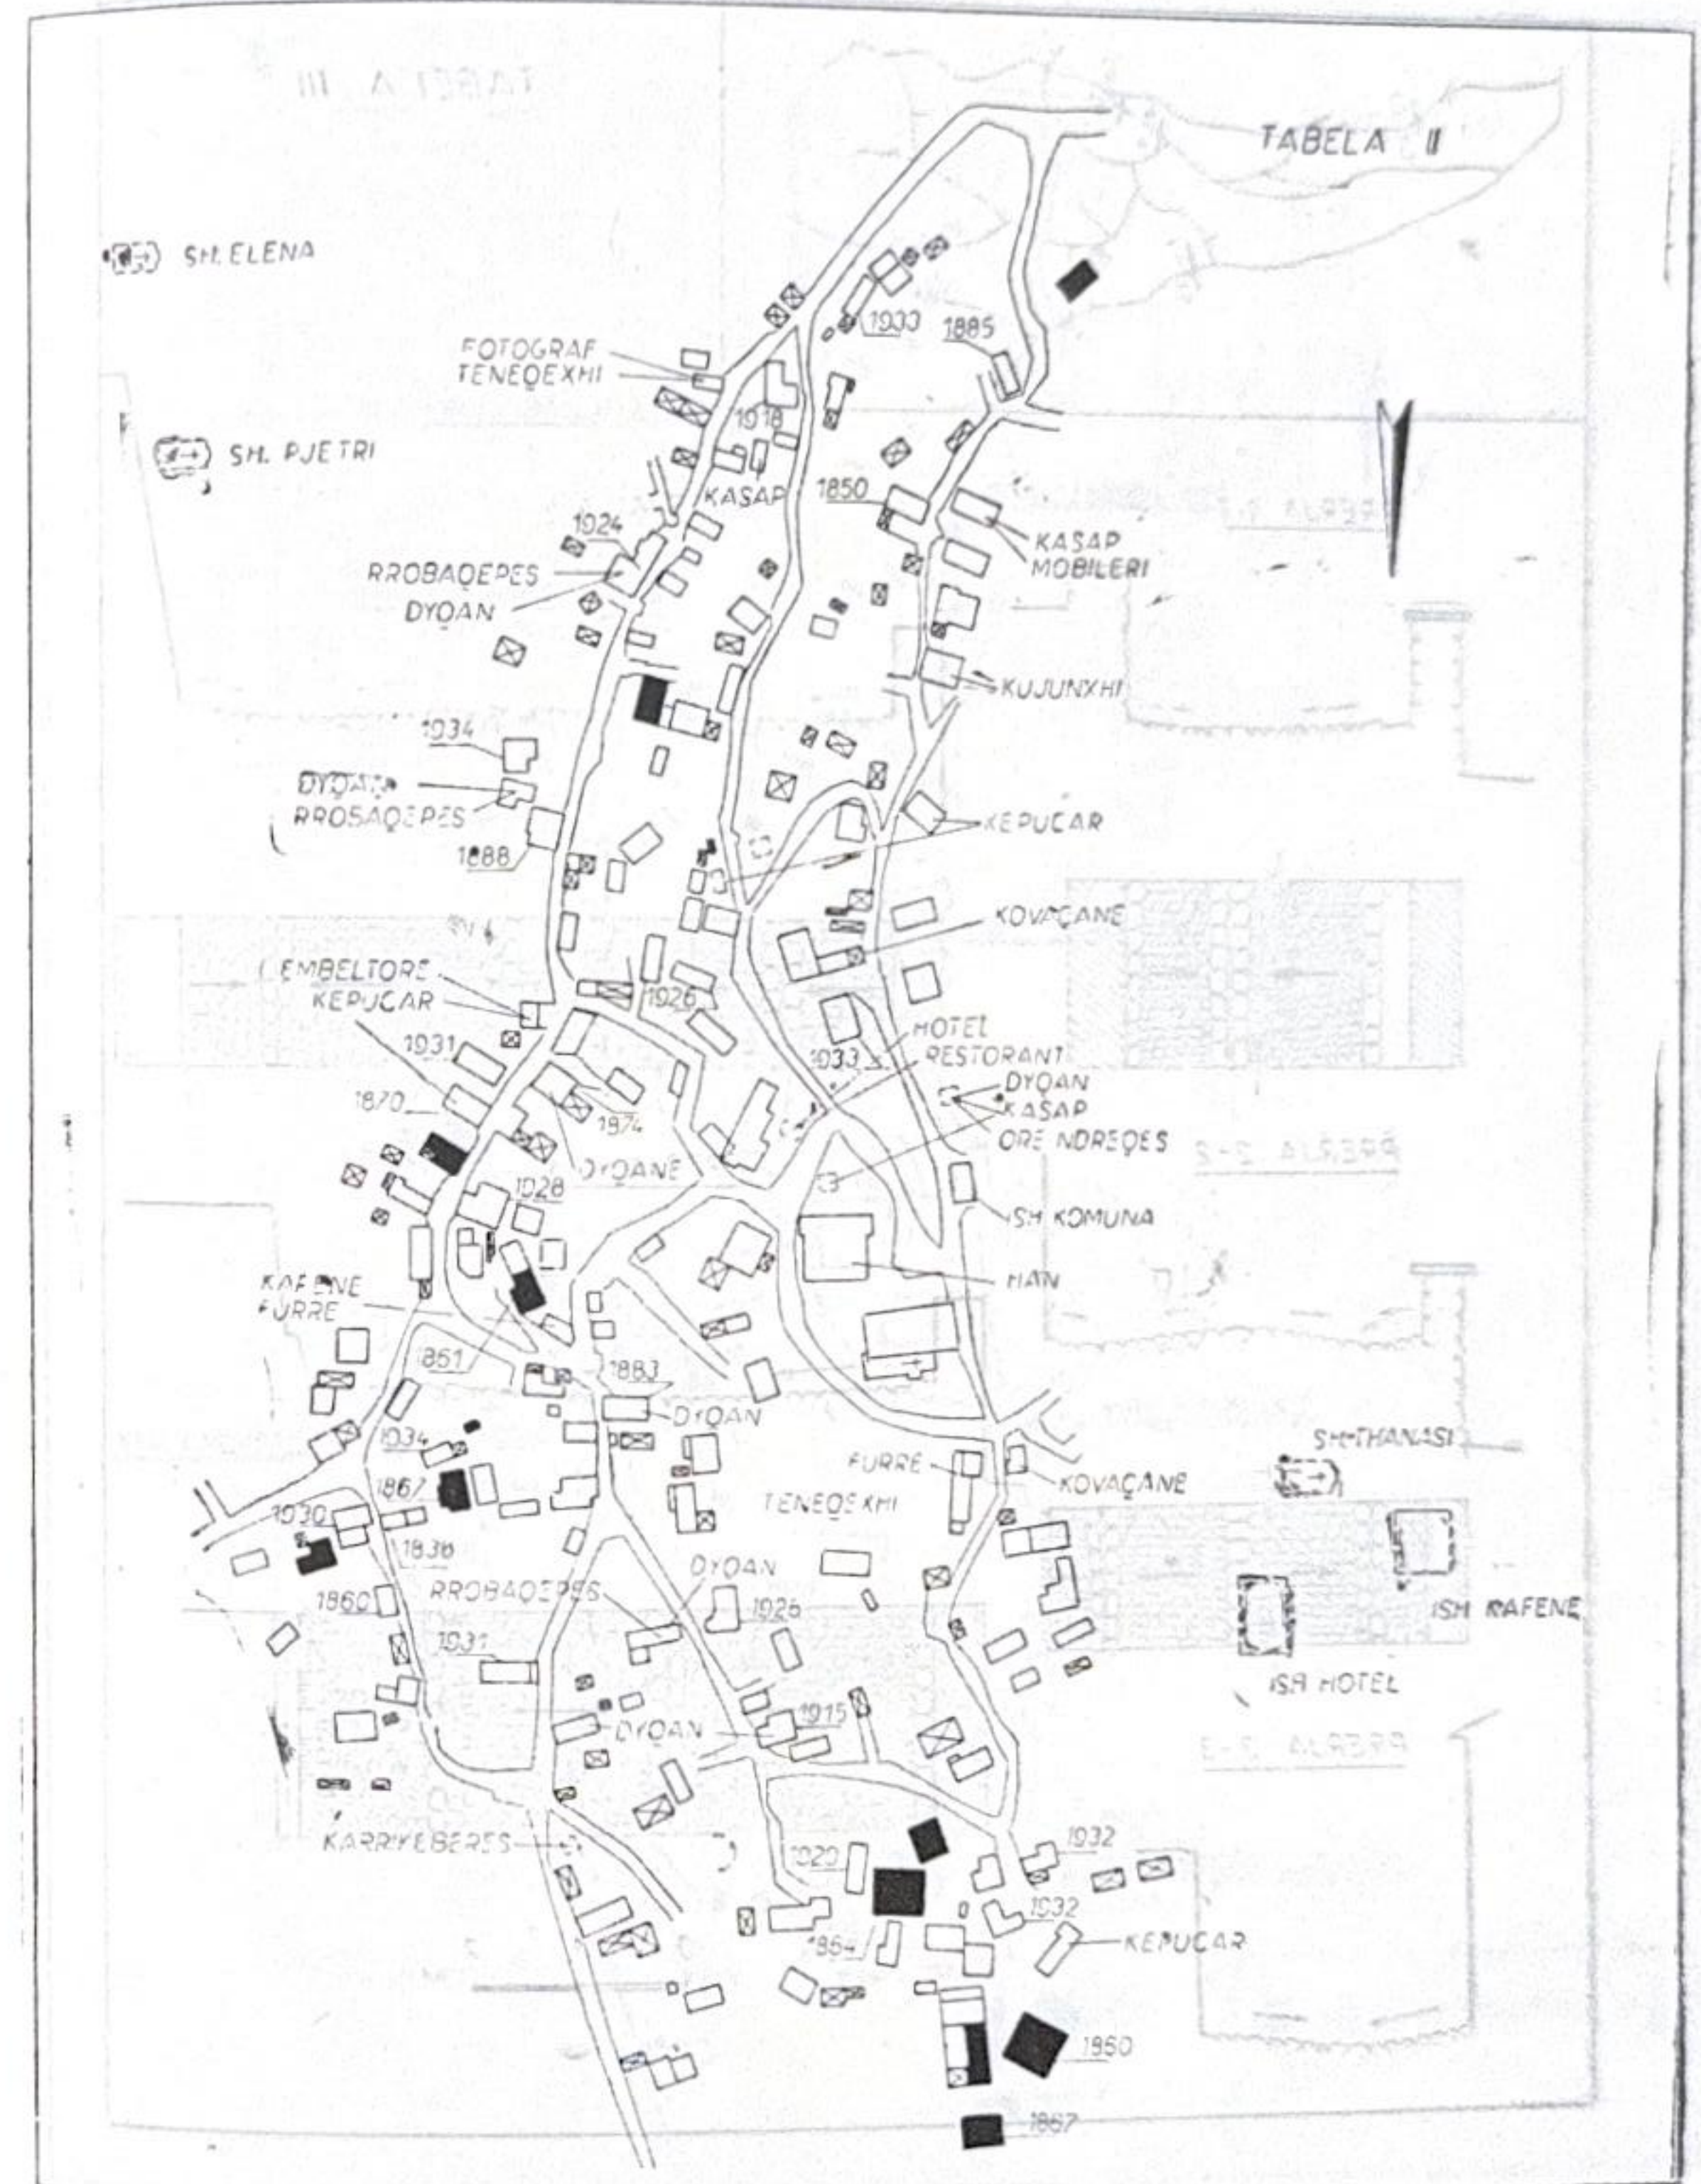
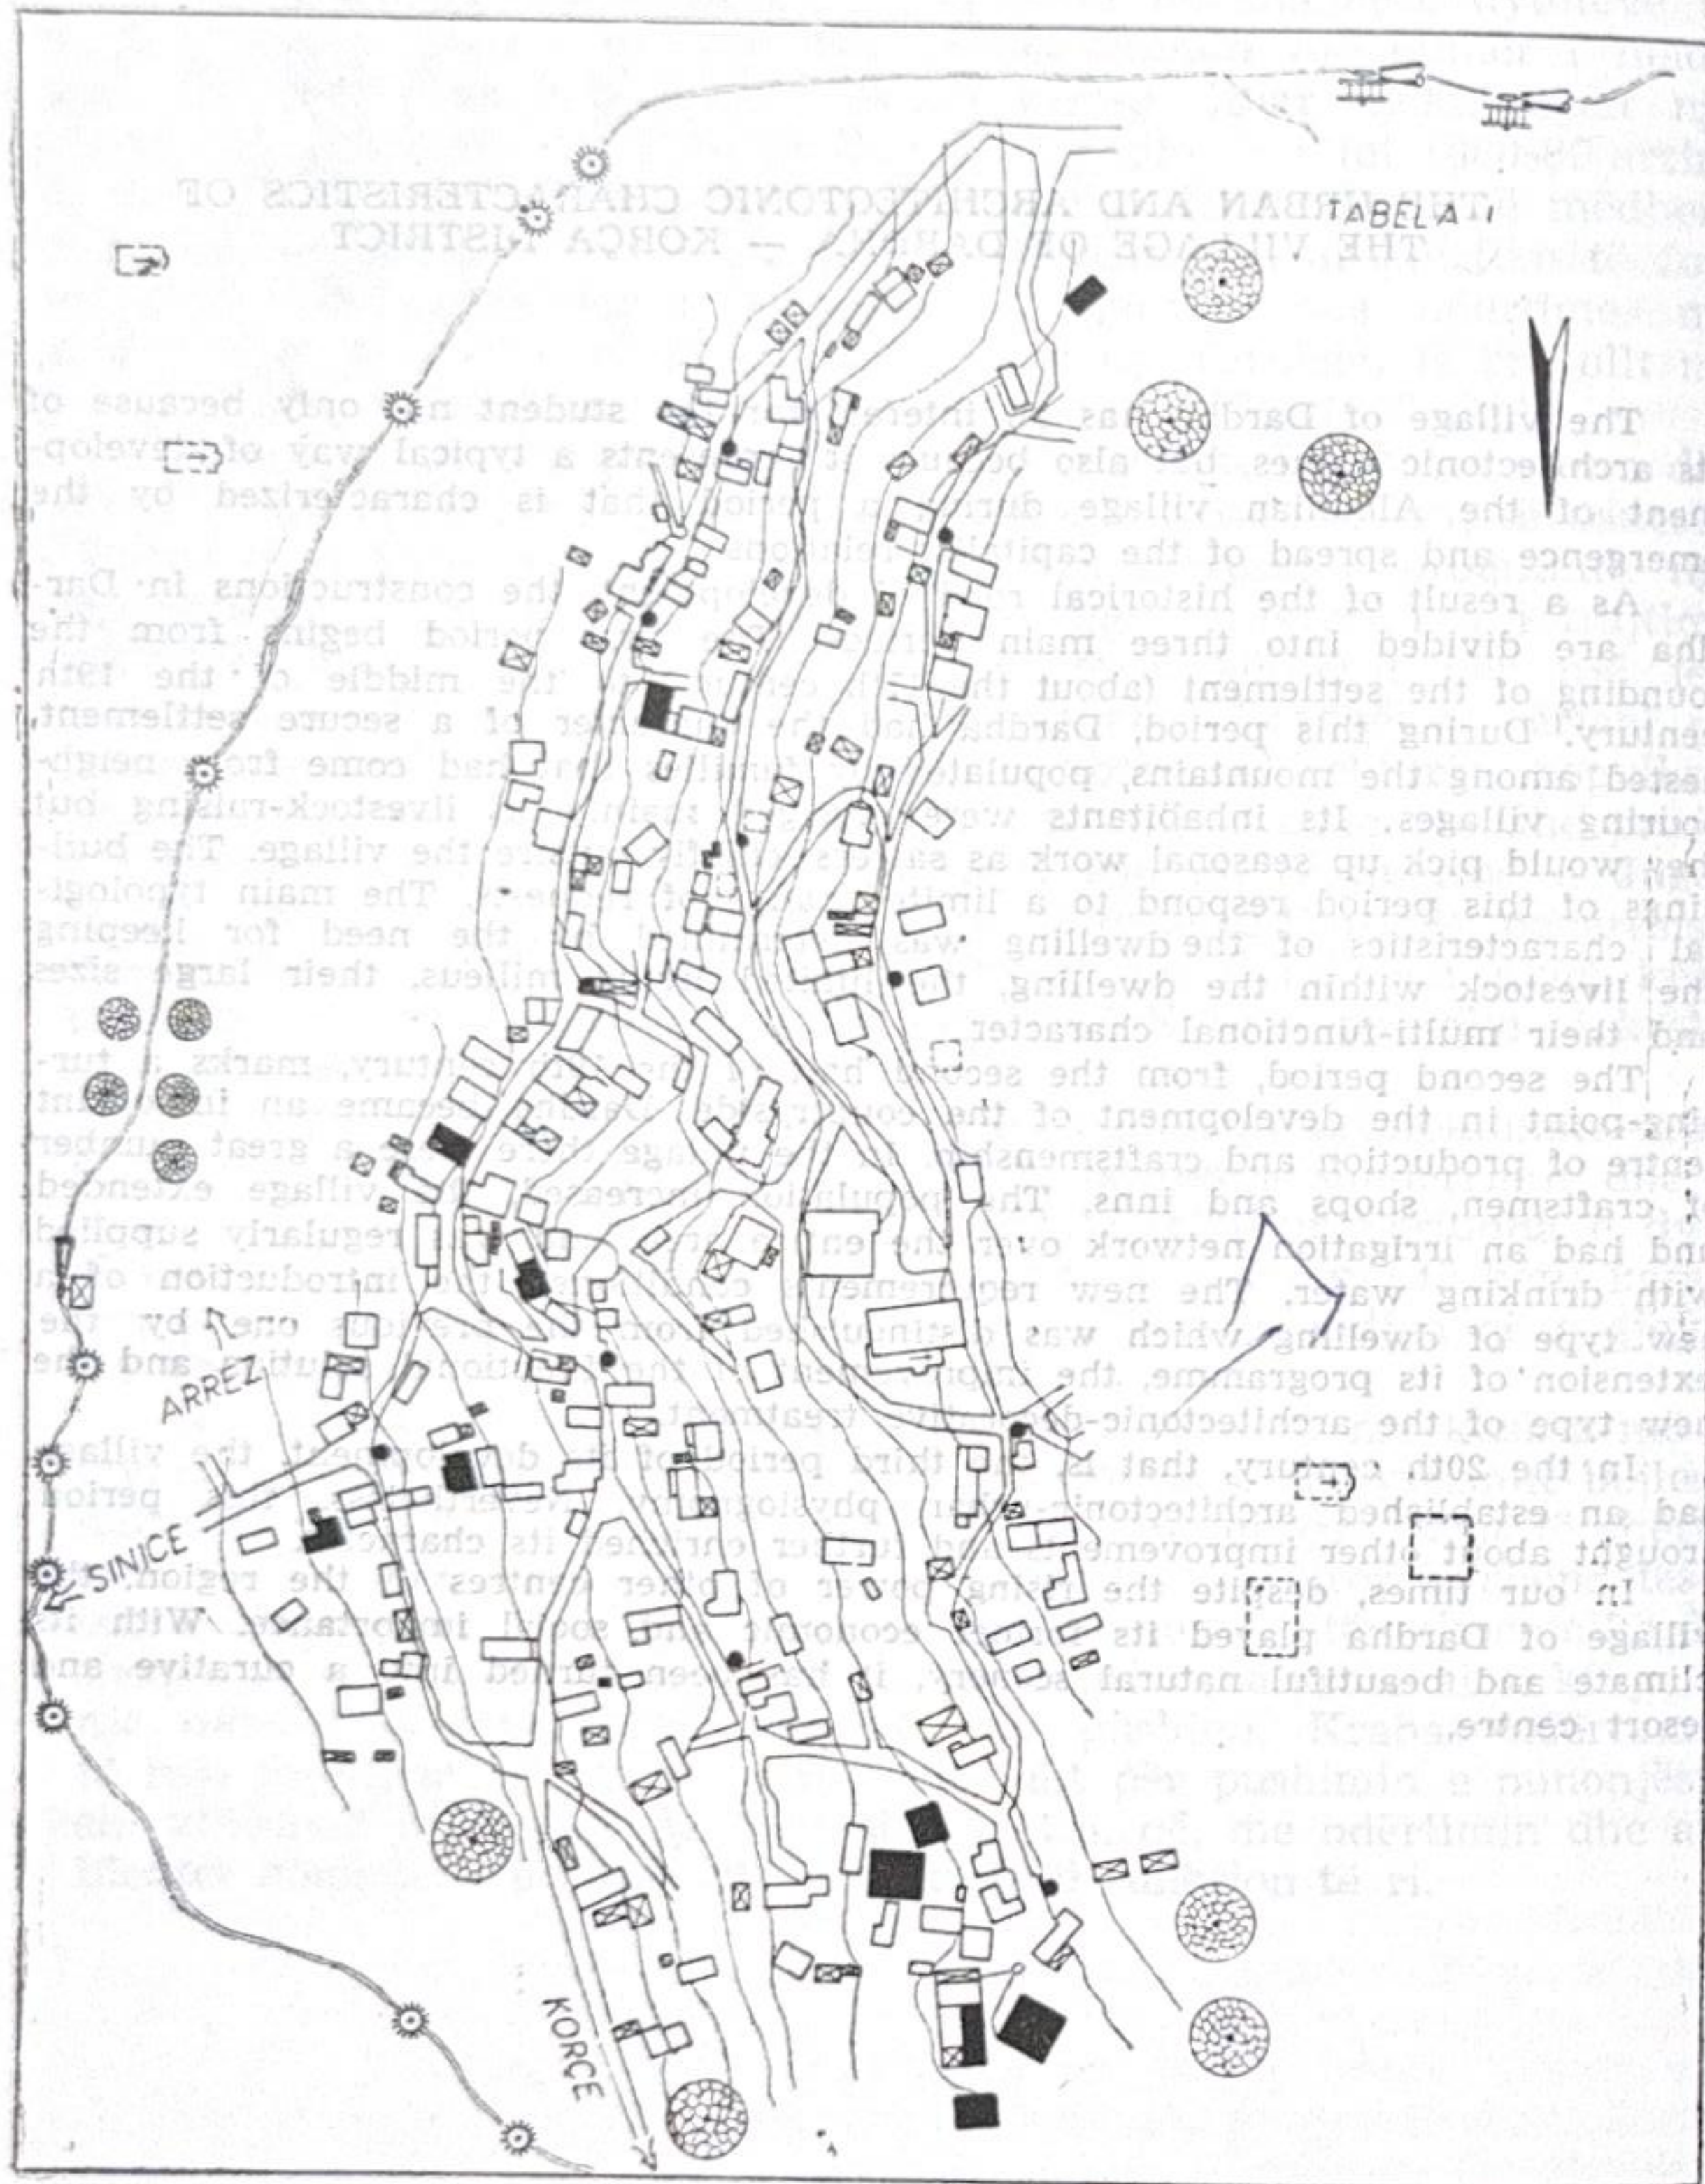


TABELA III

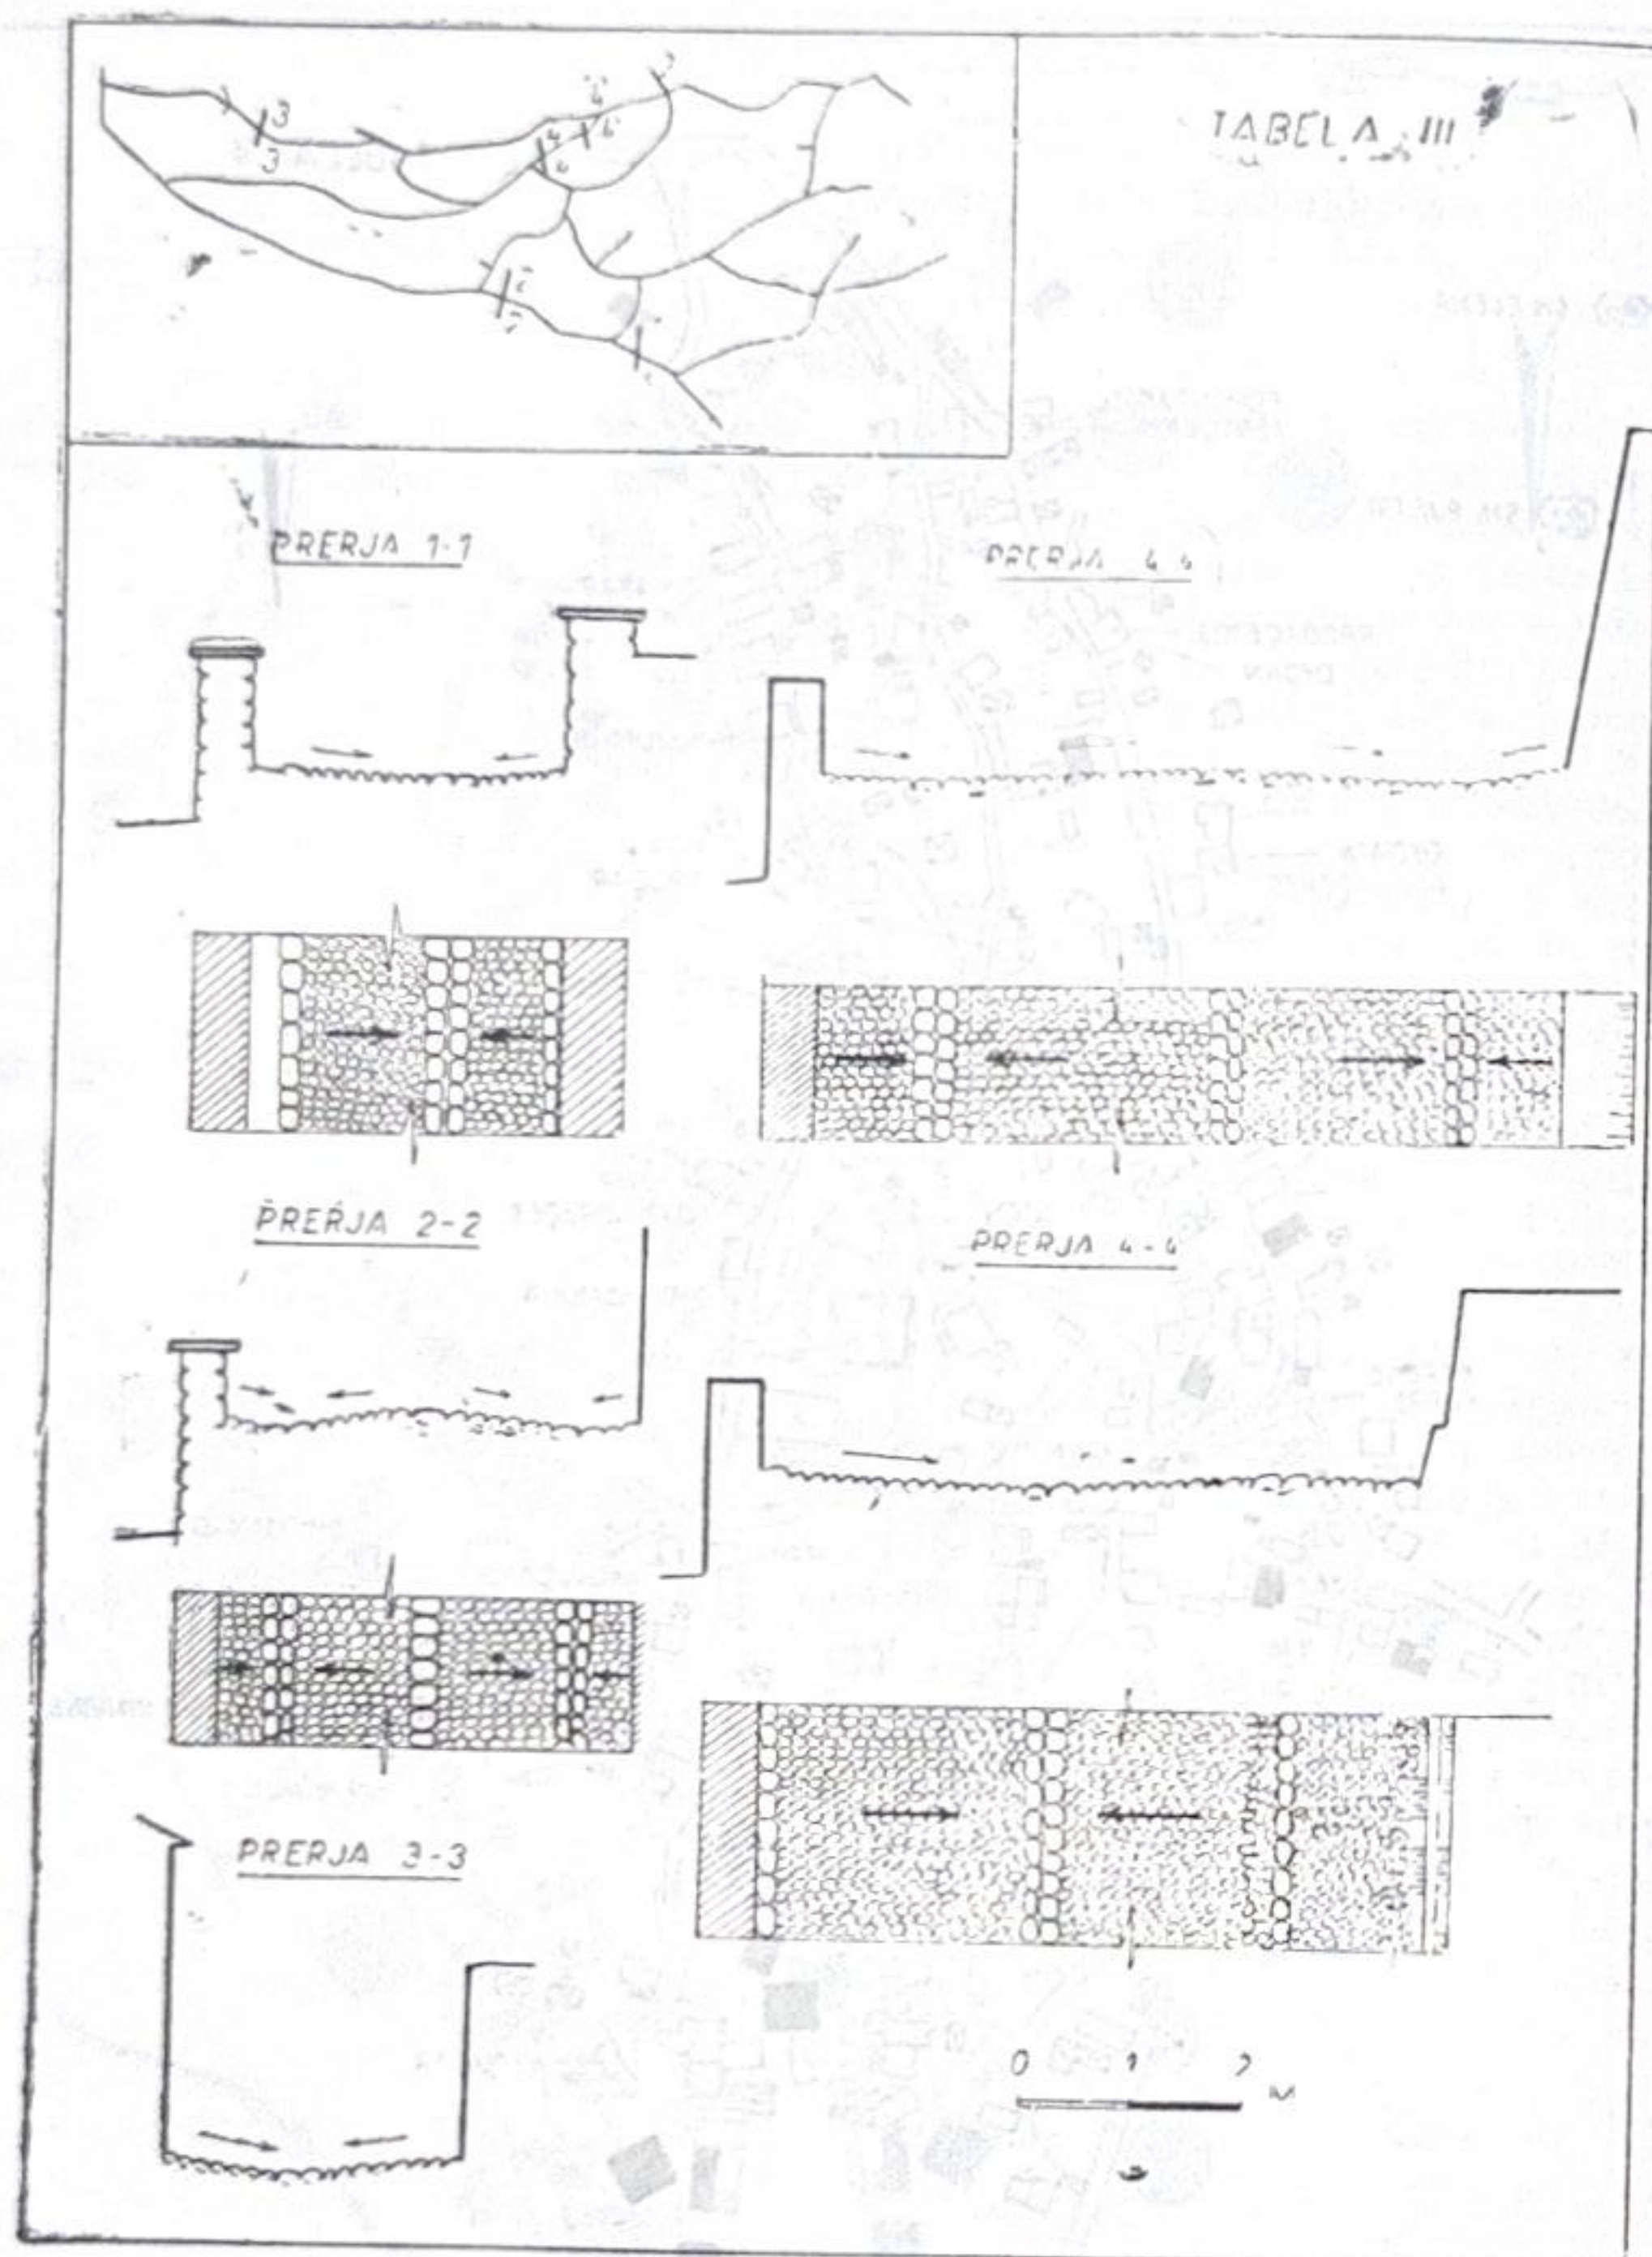


TABELA IV

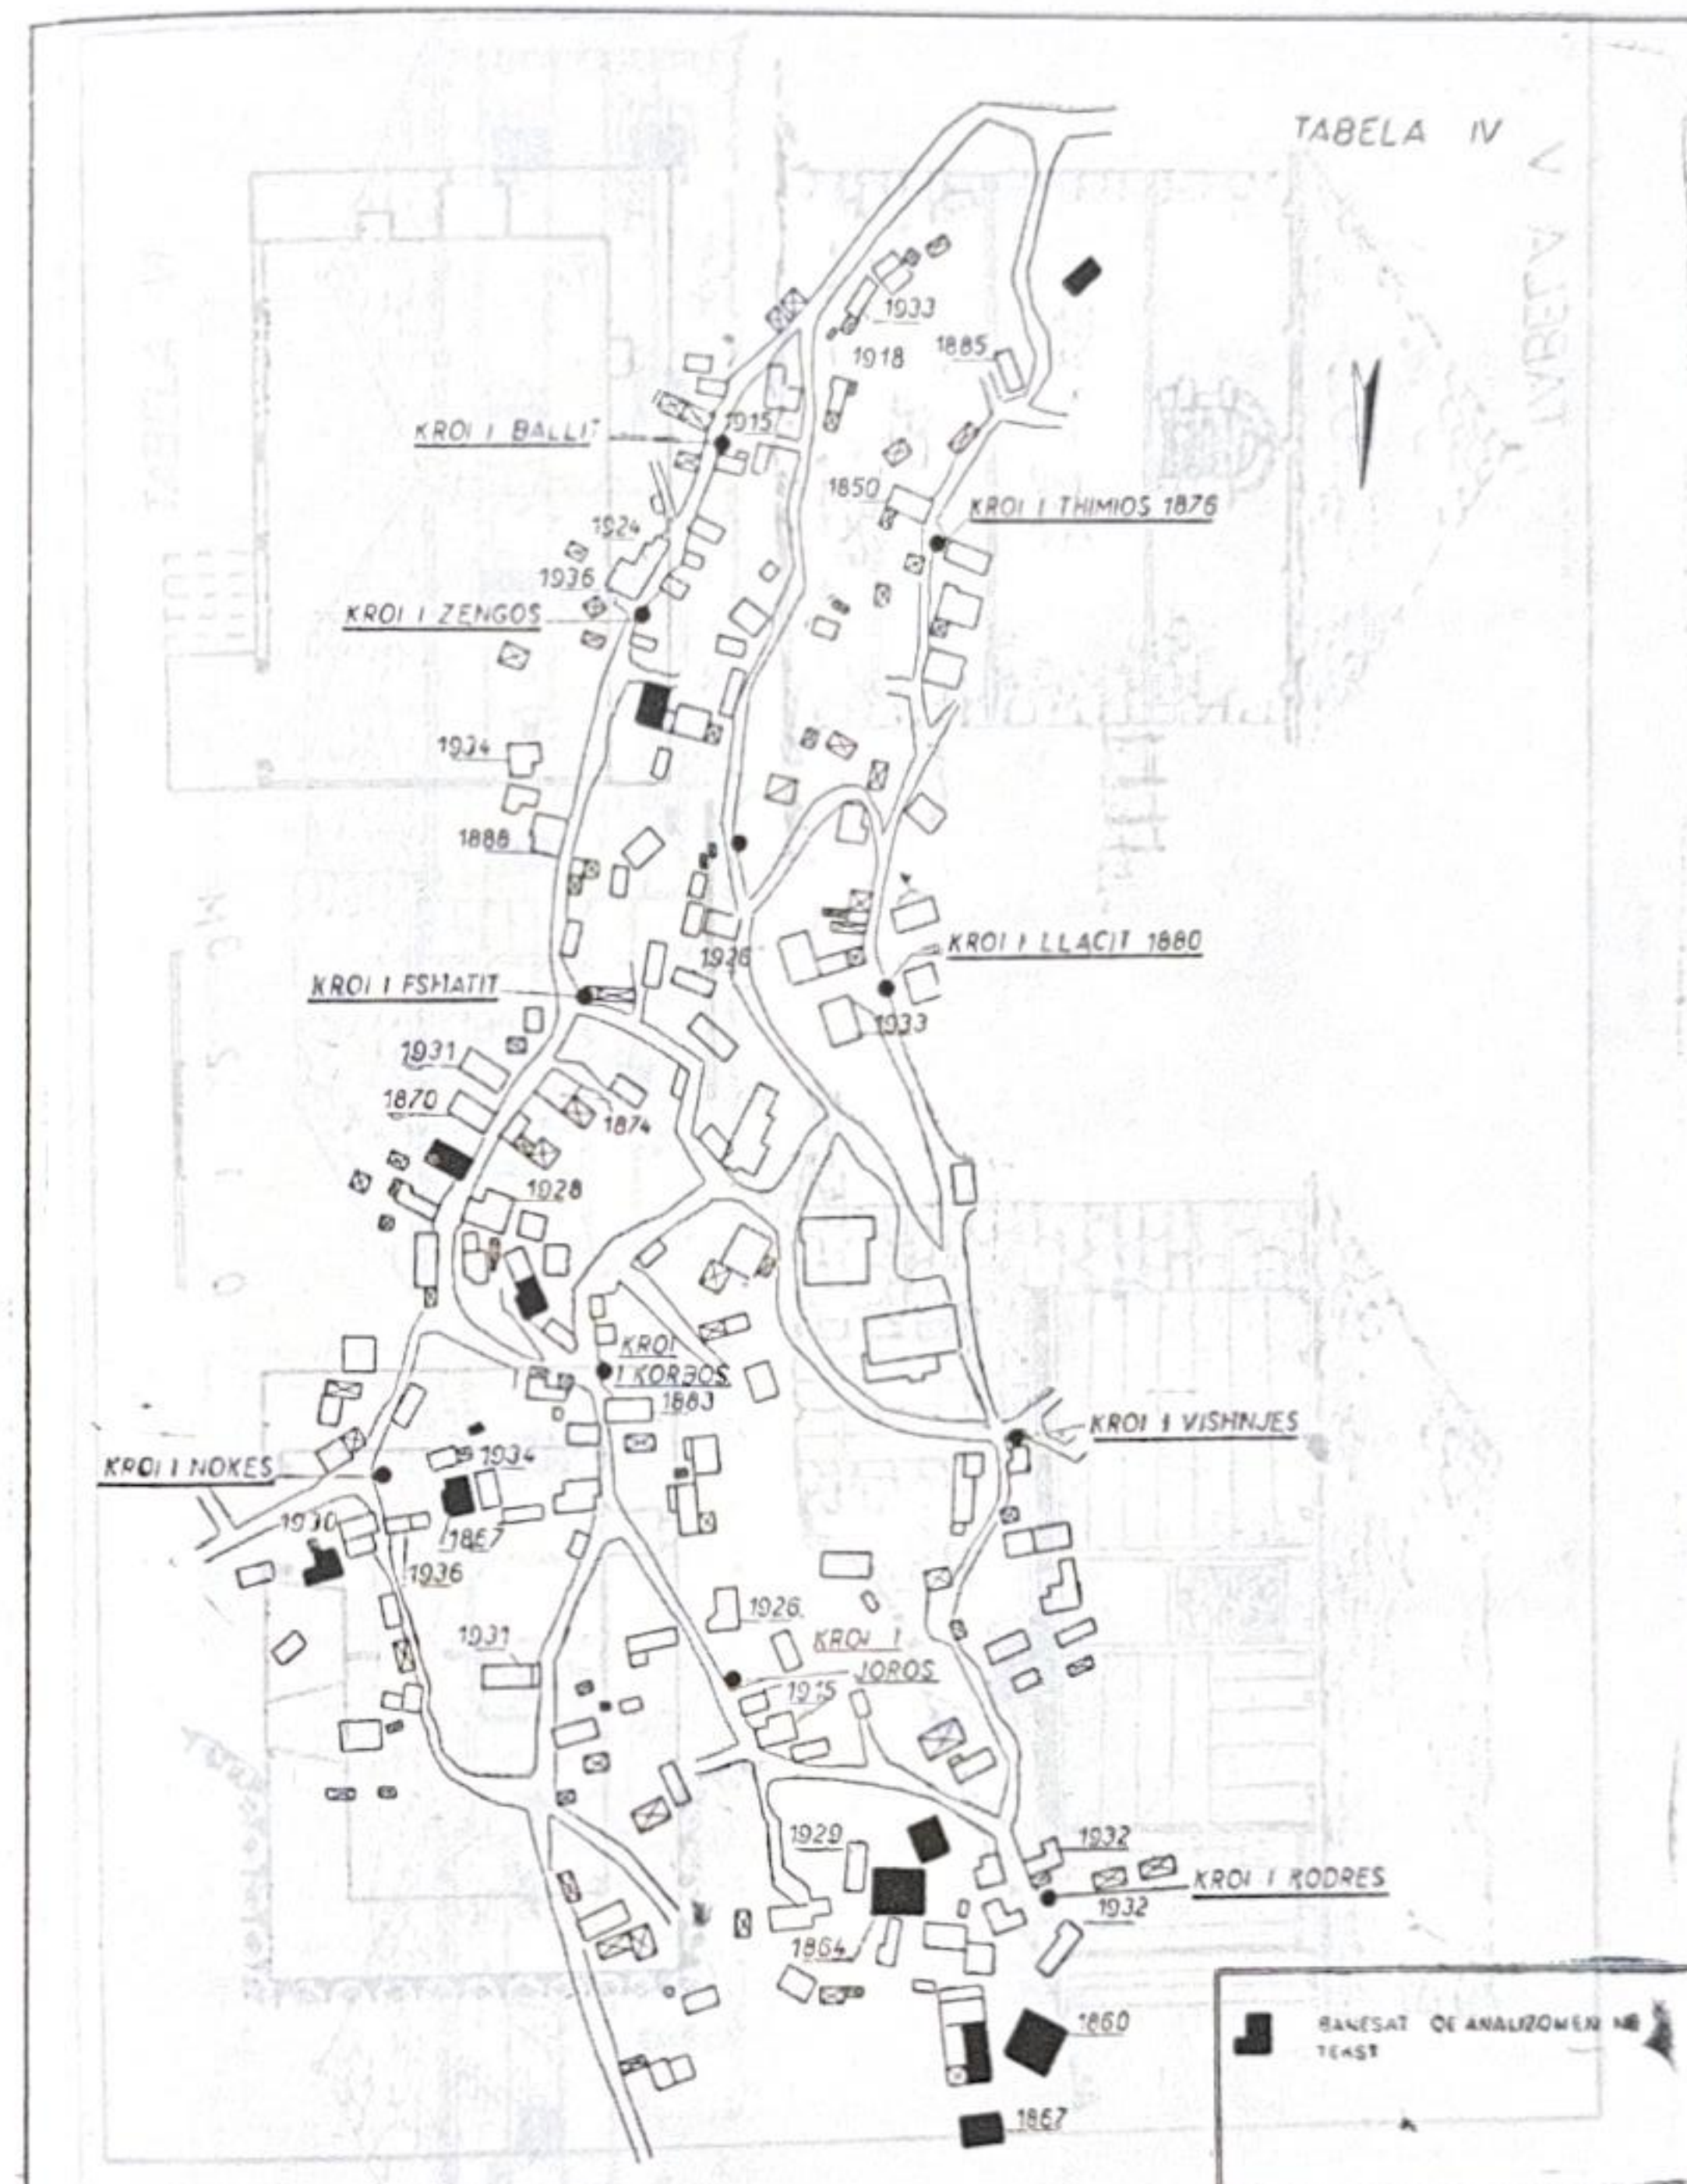


TABELA V

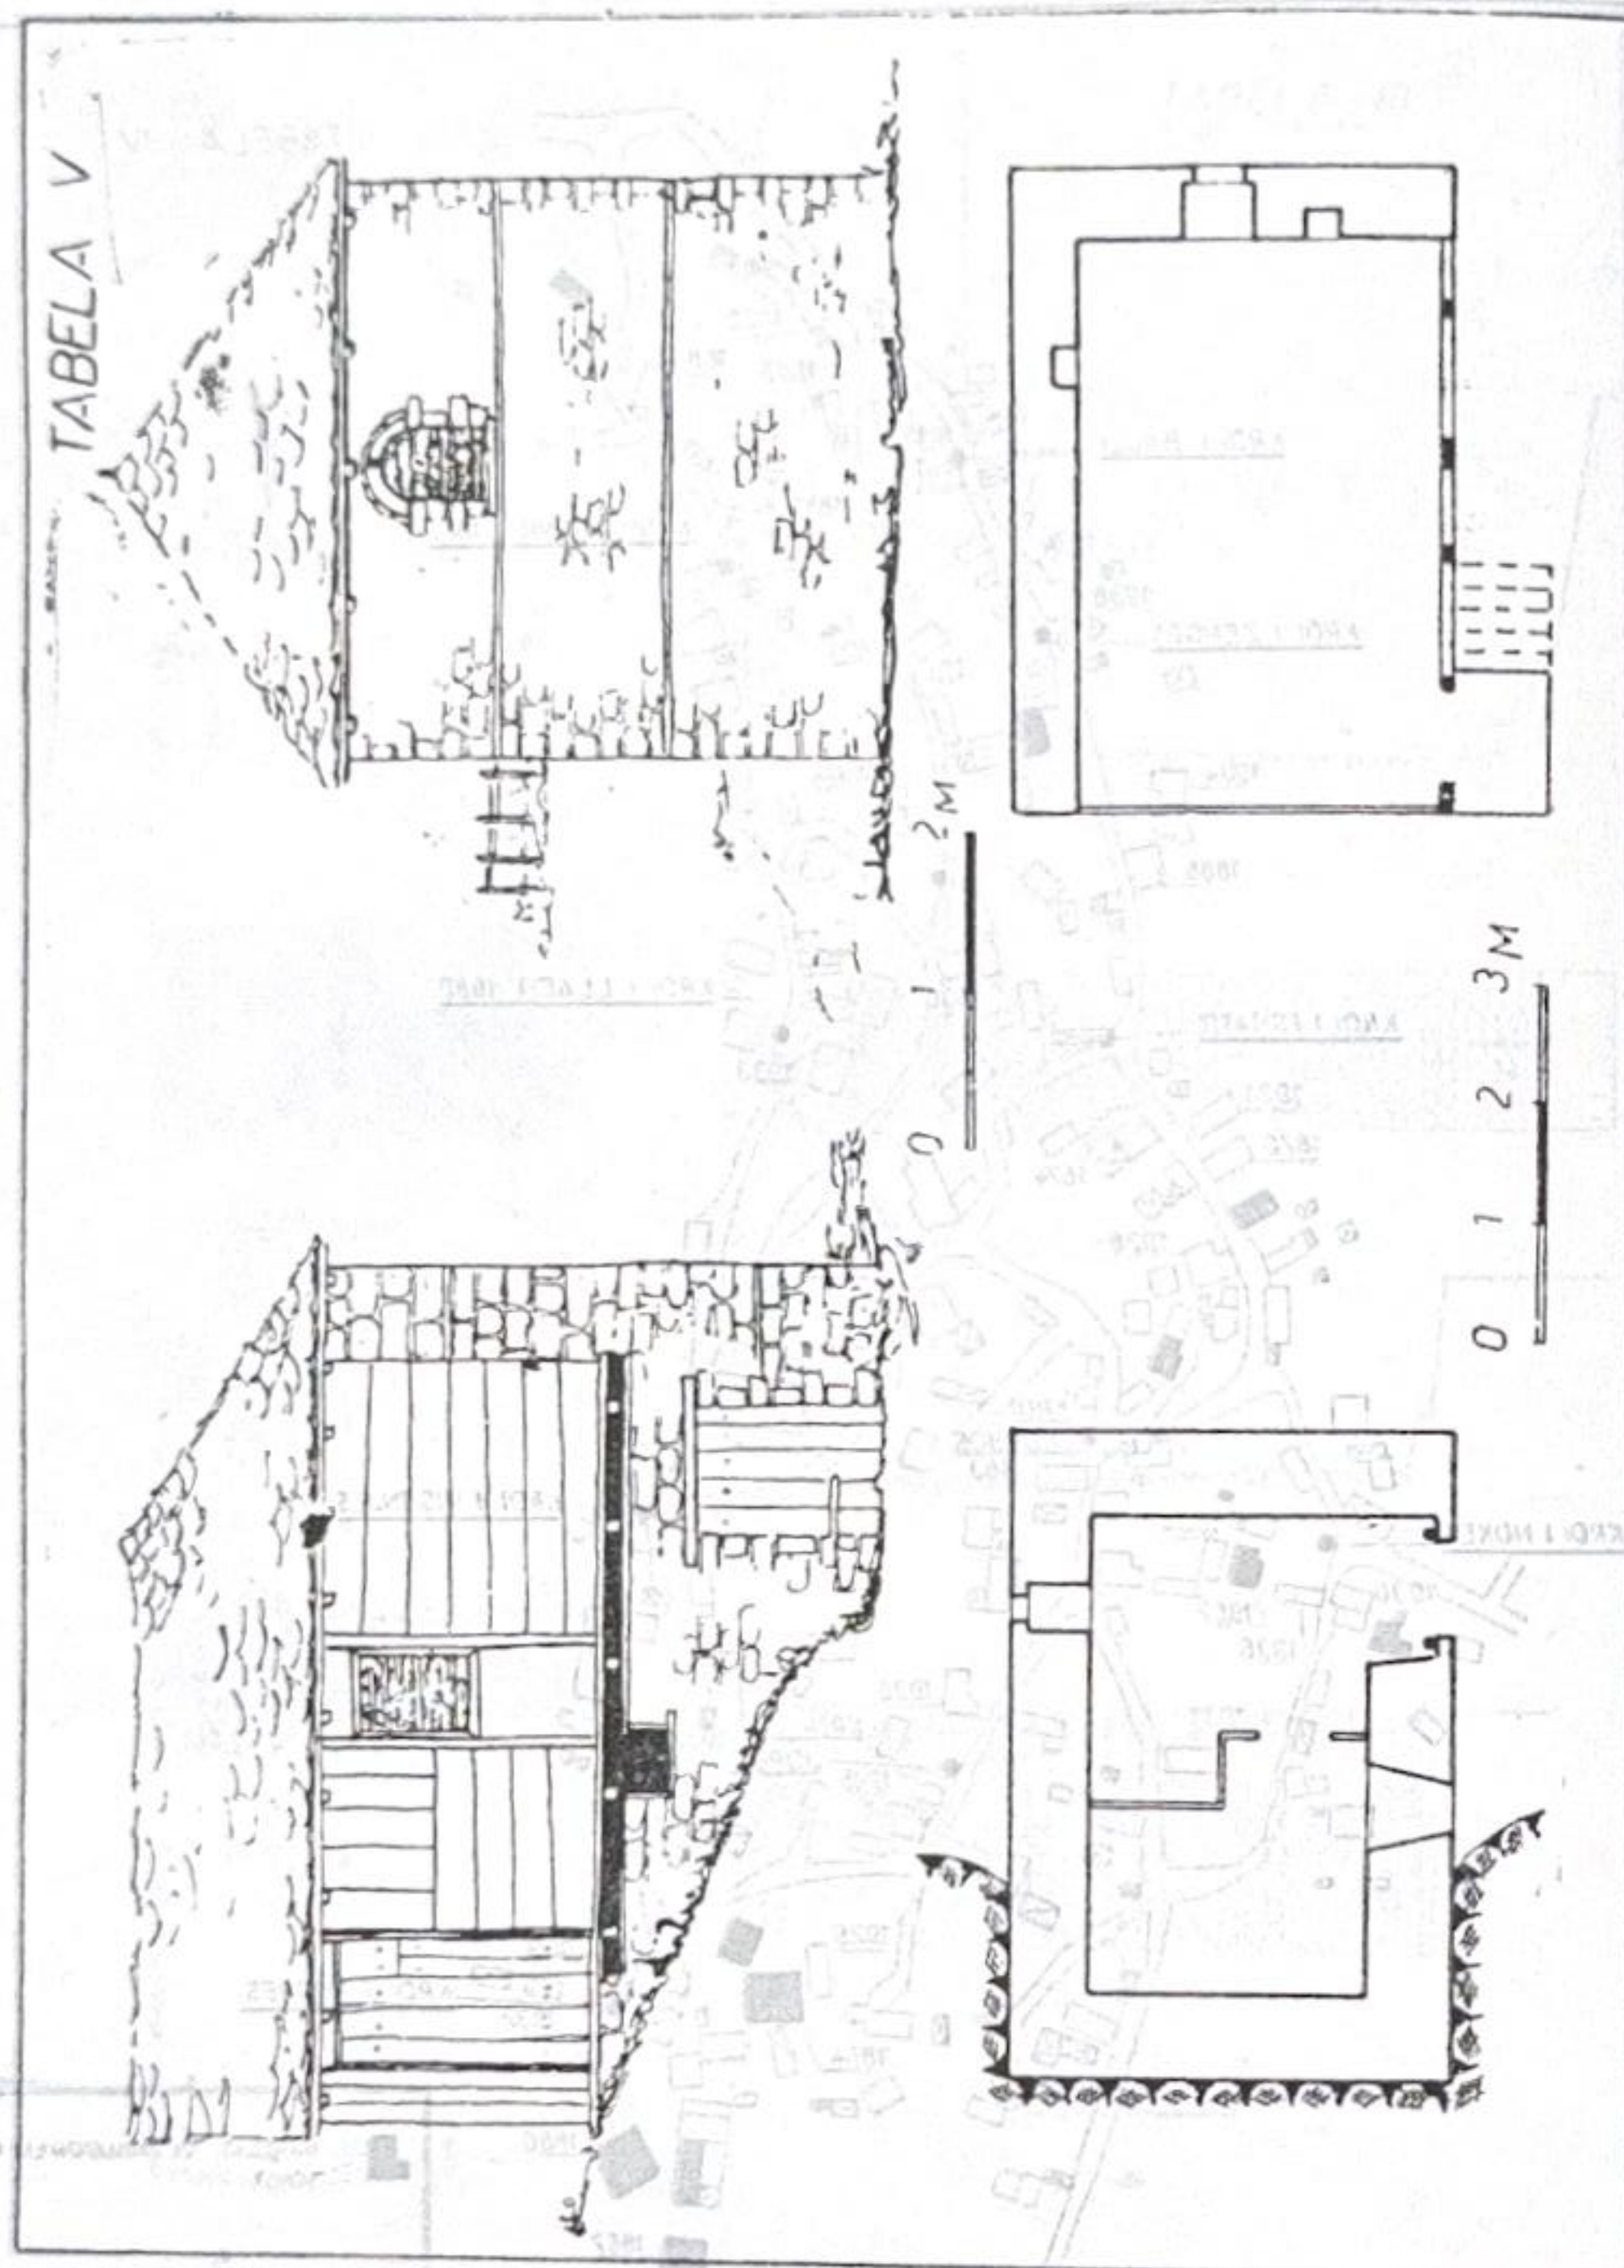


TABELA VI

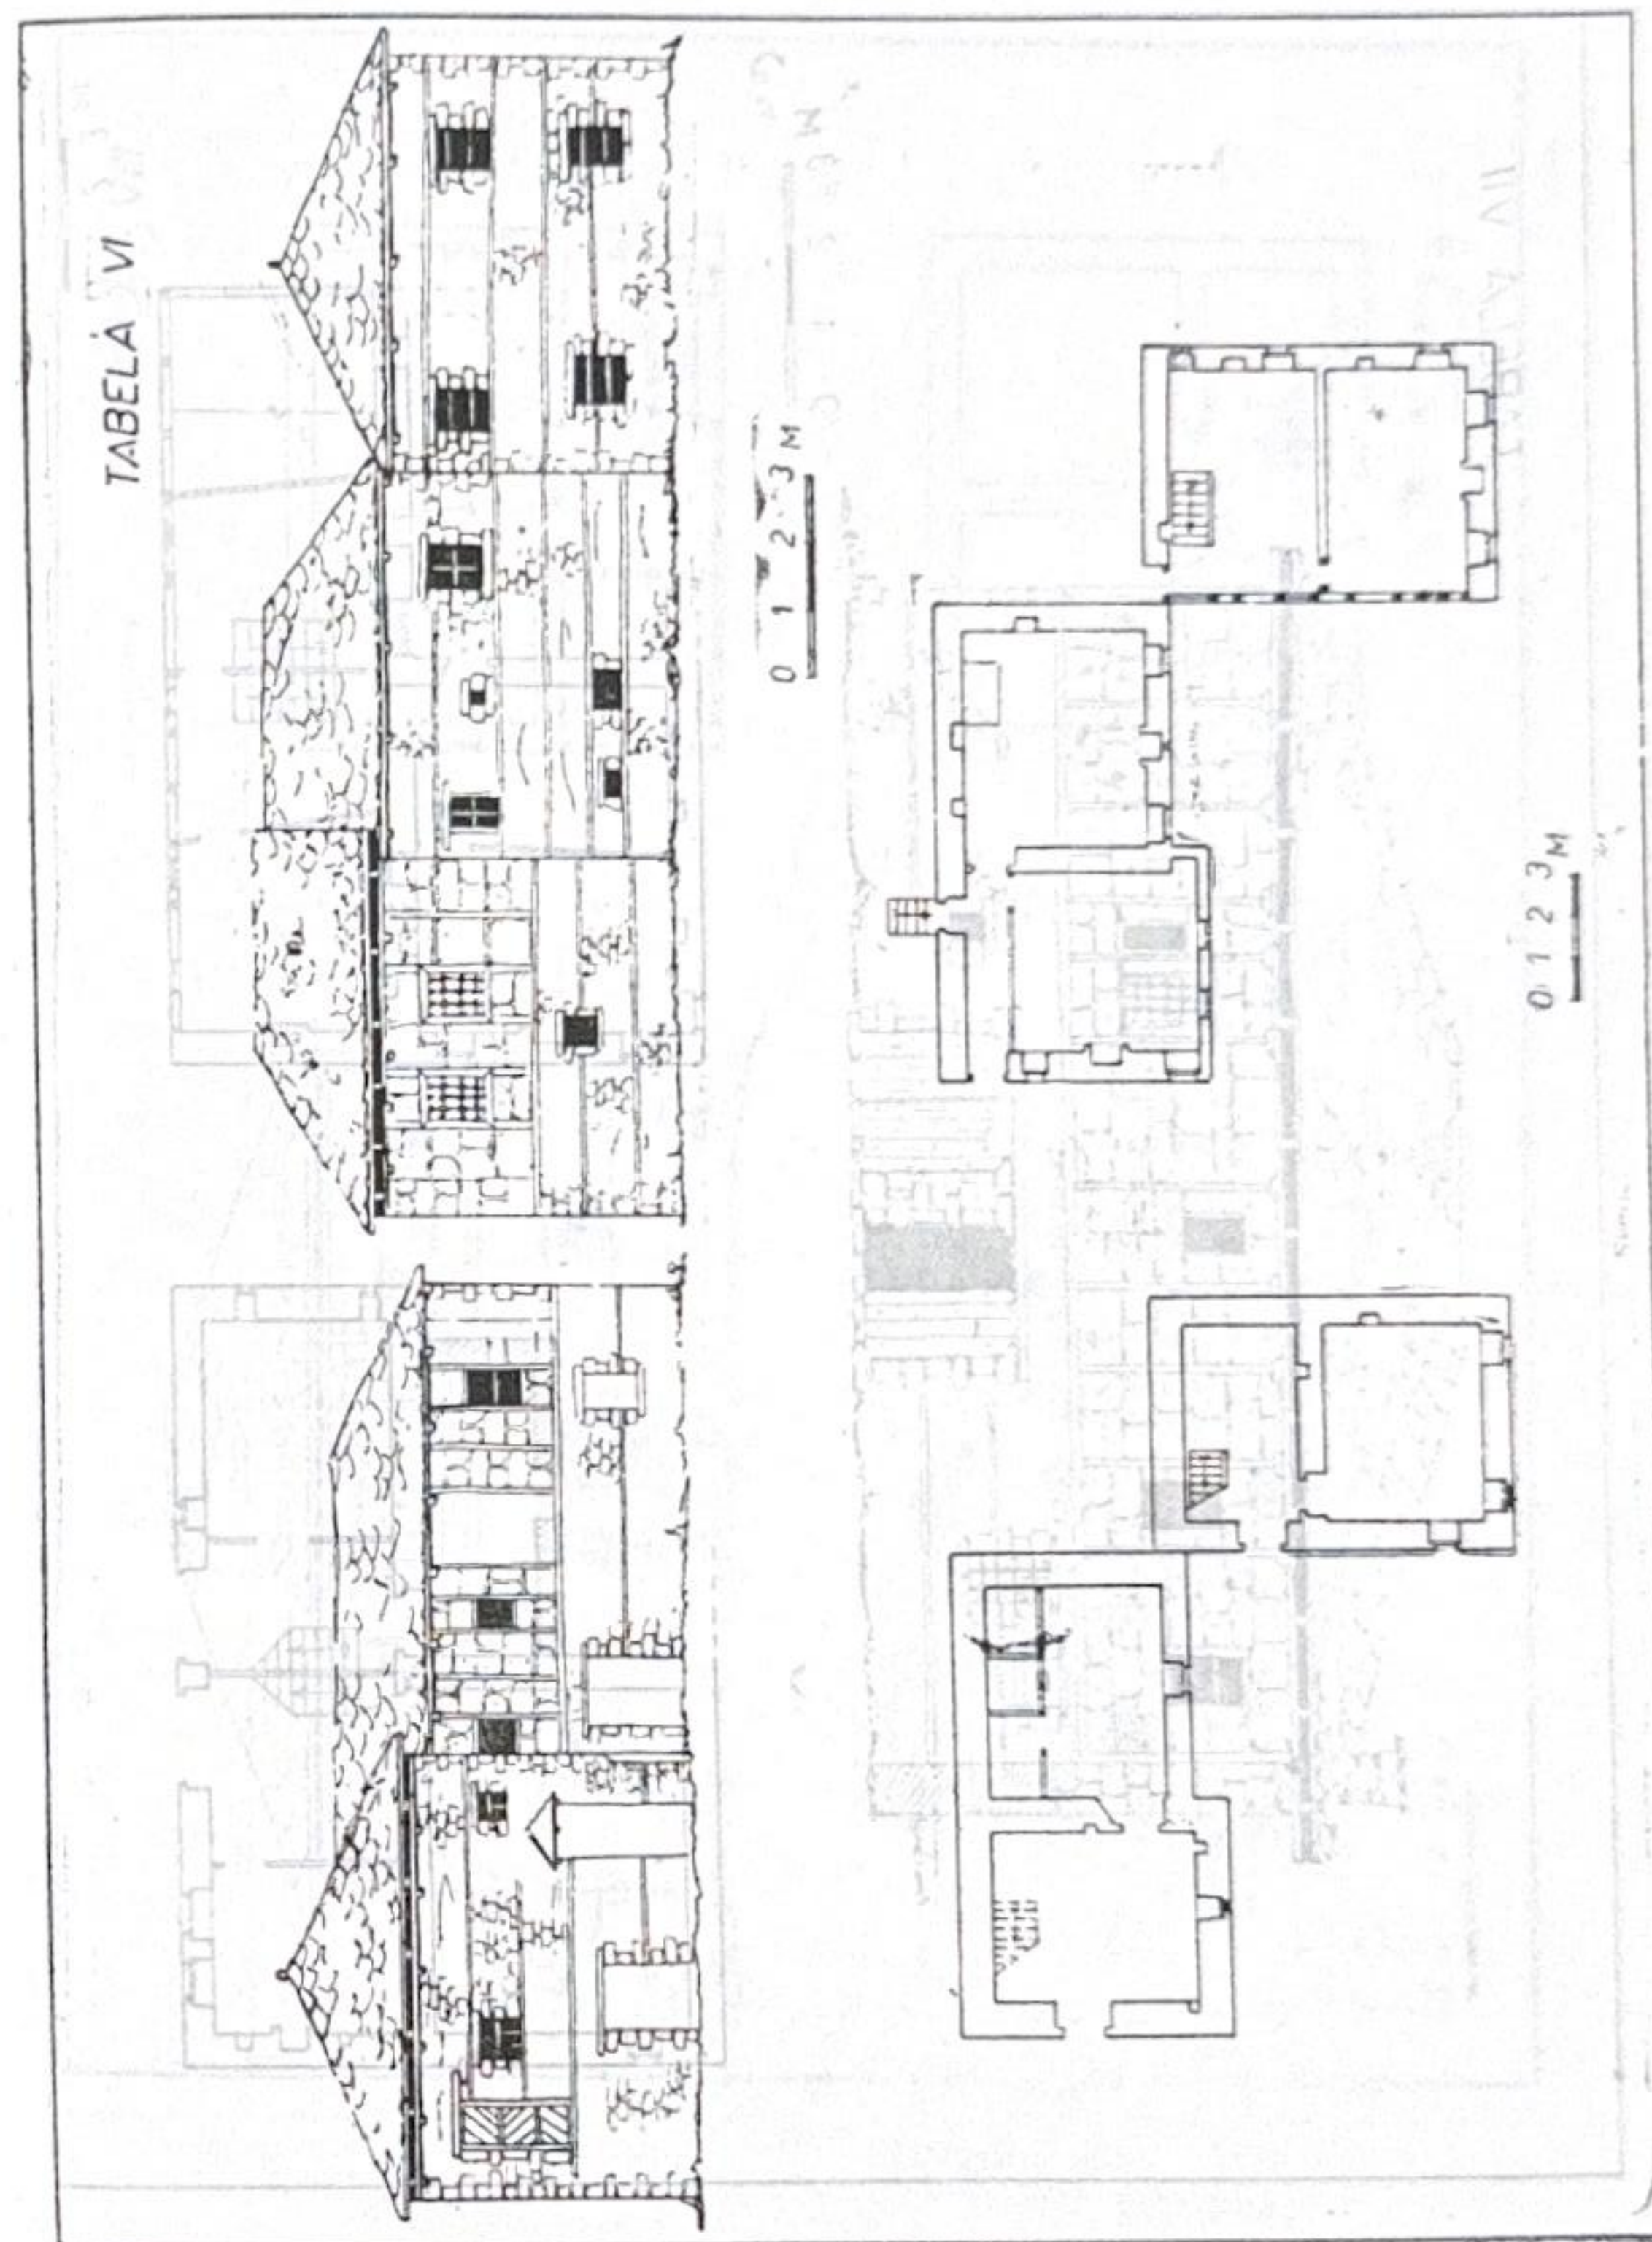


TABELA VII

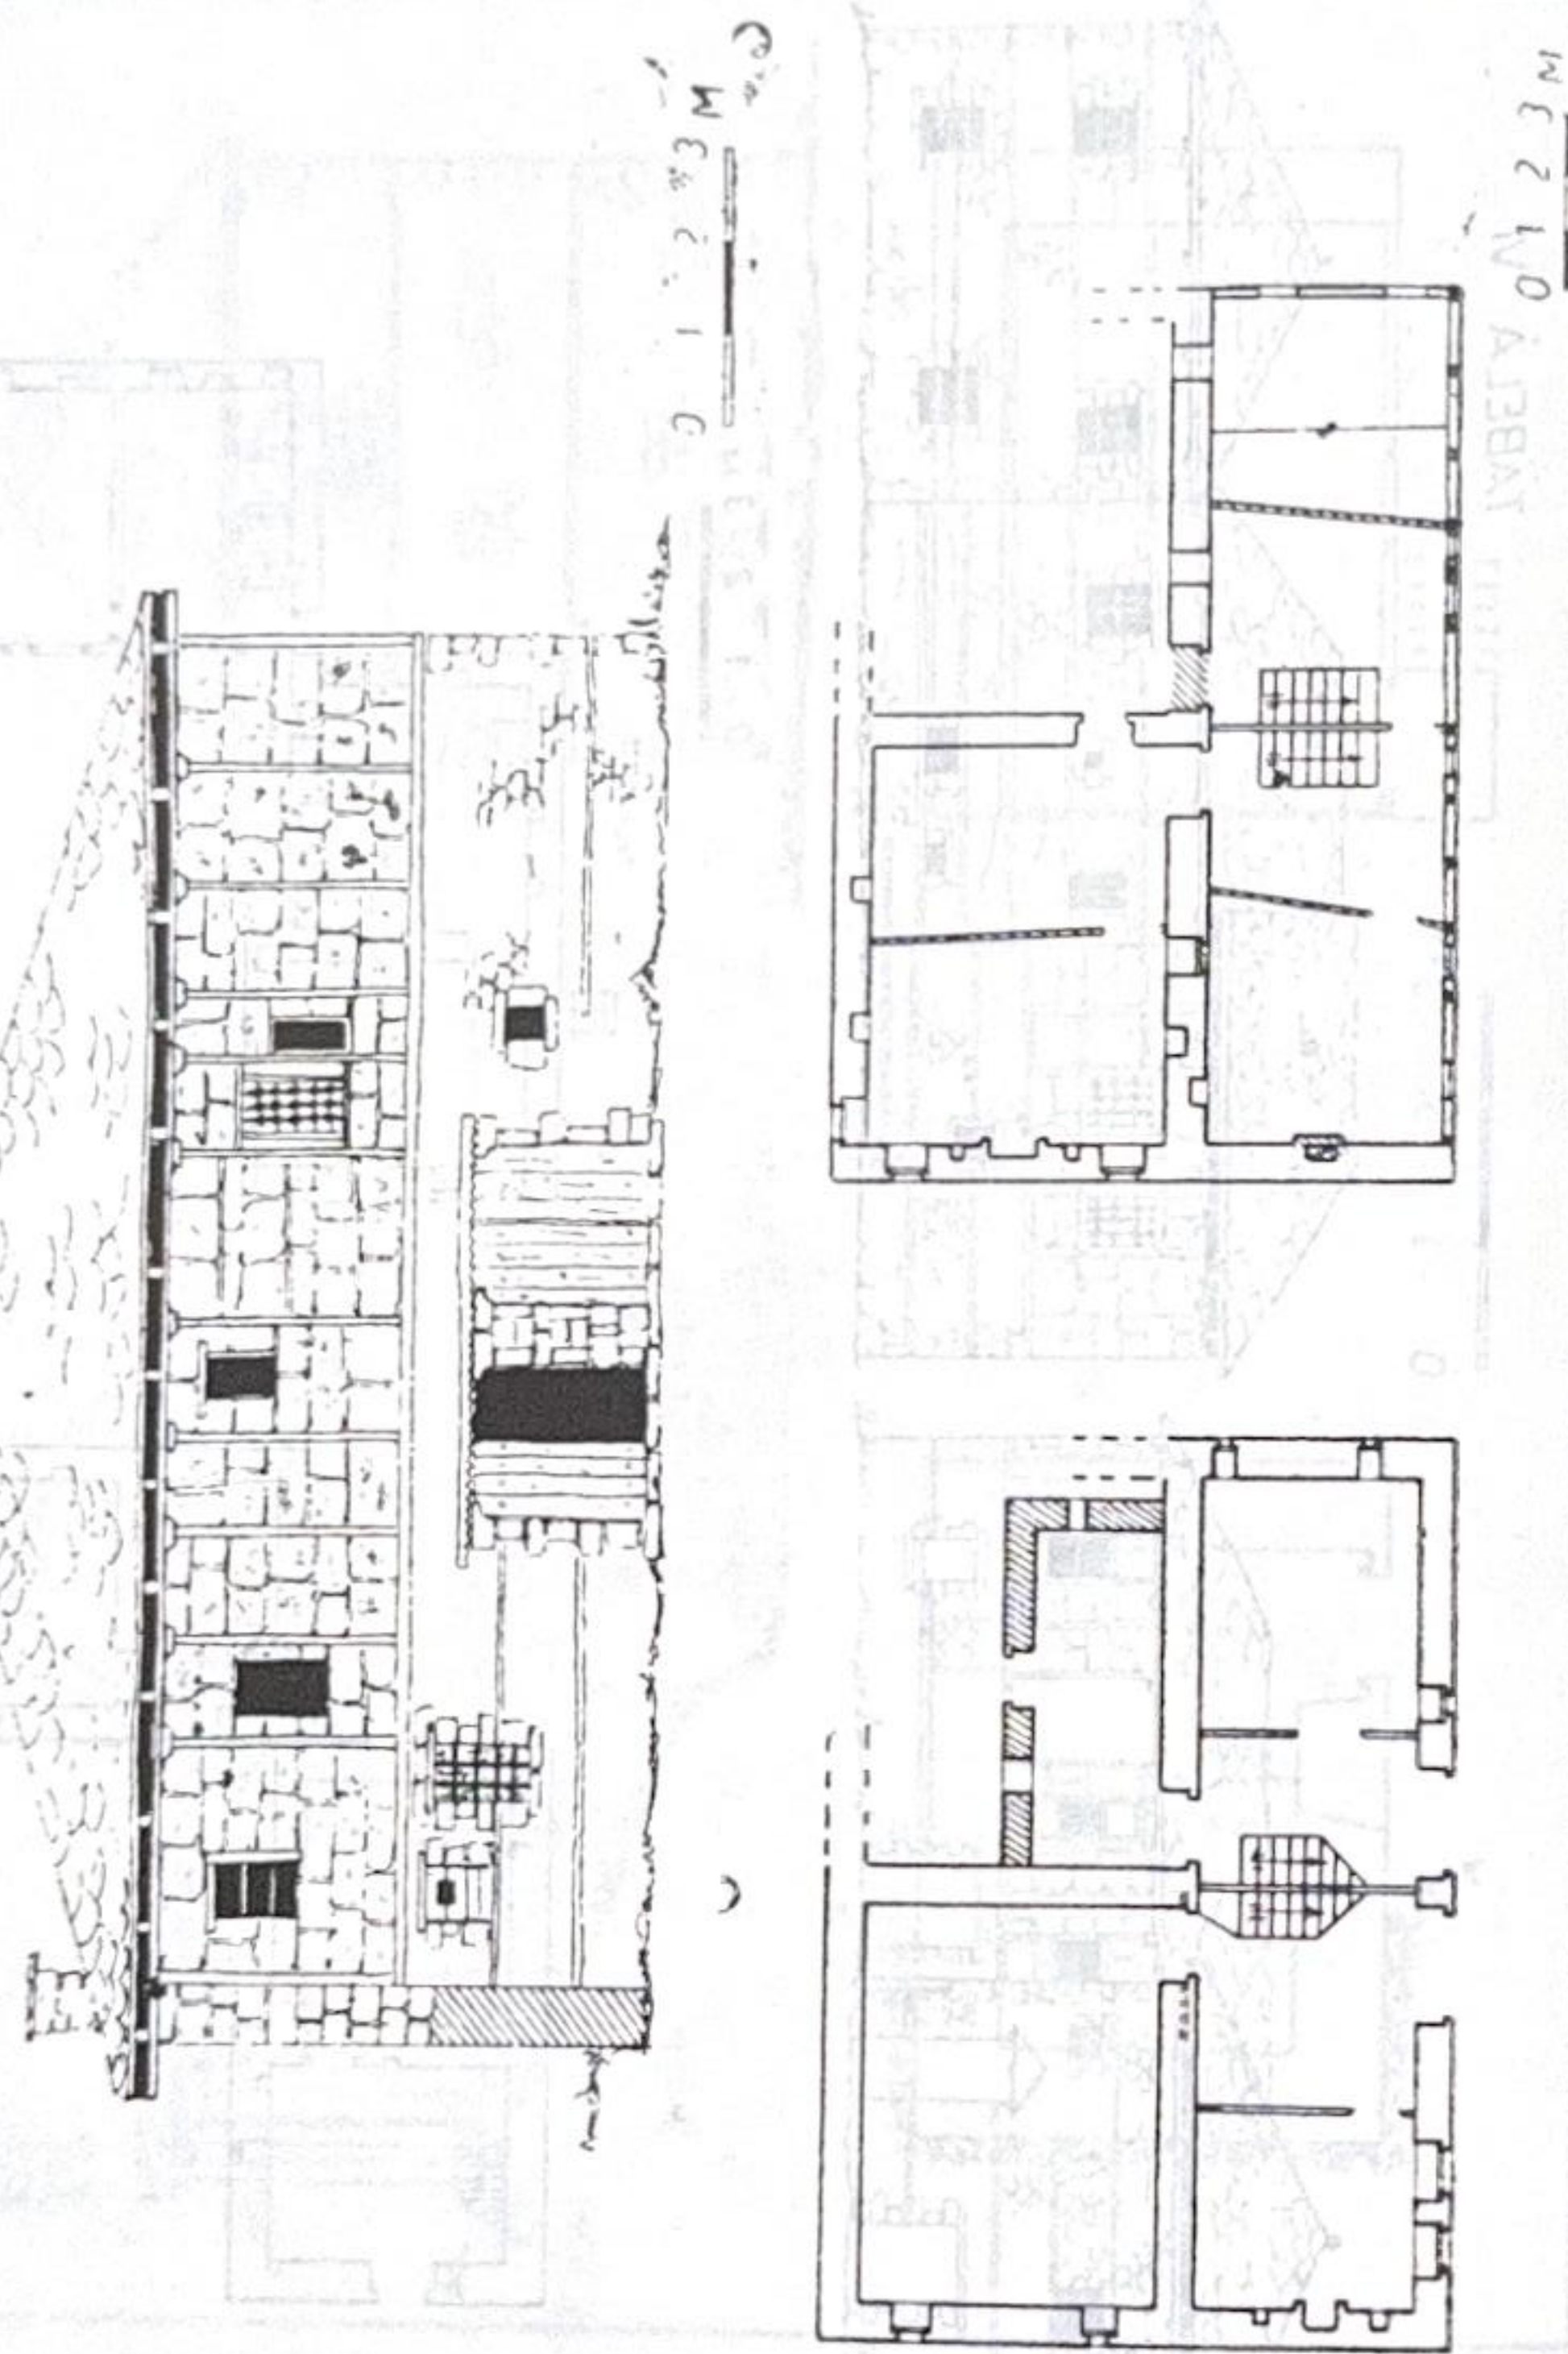
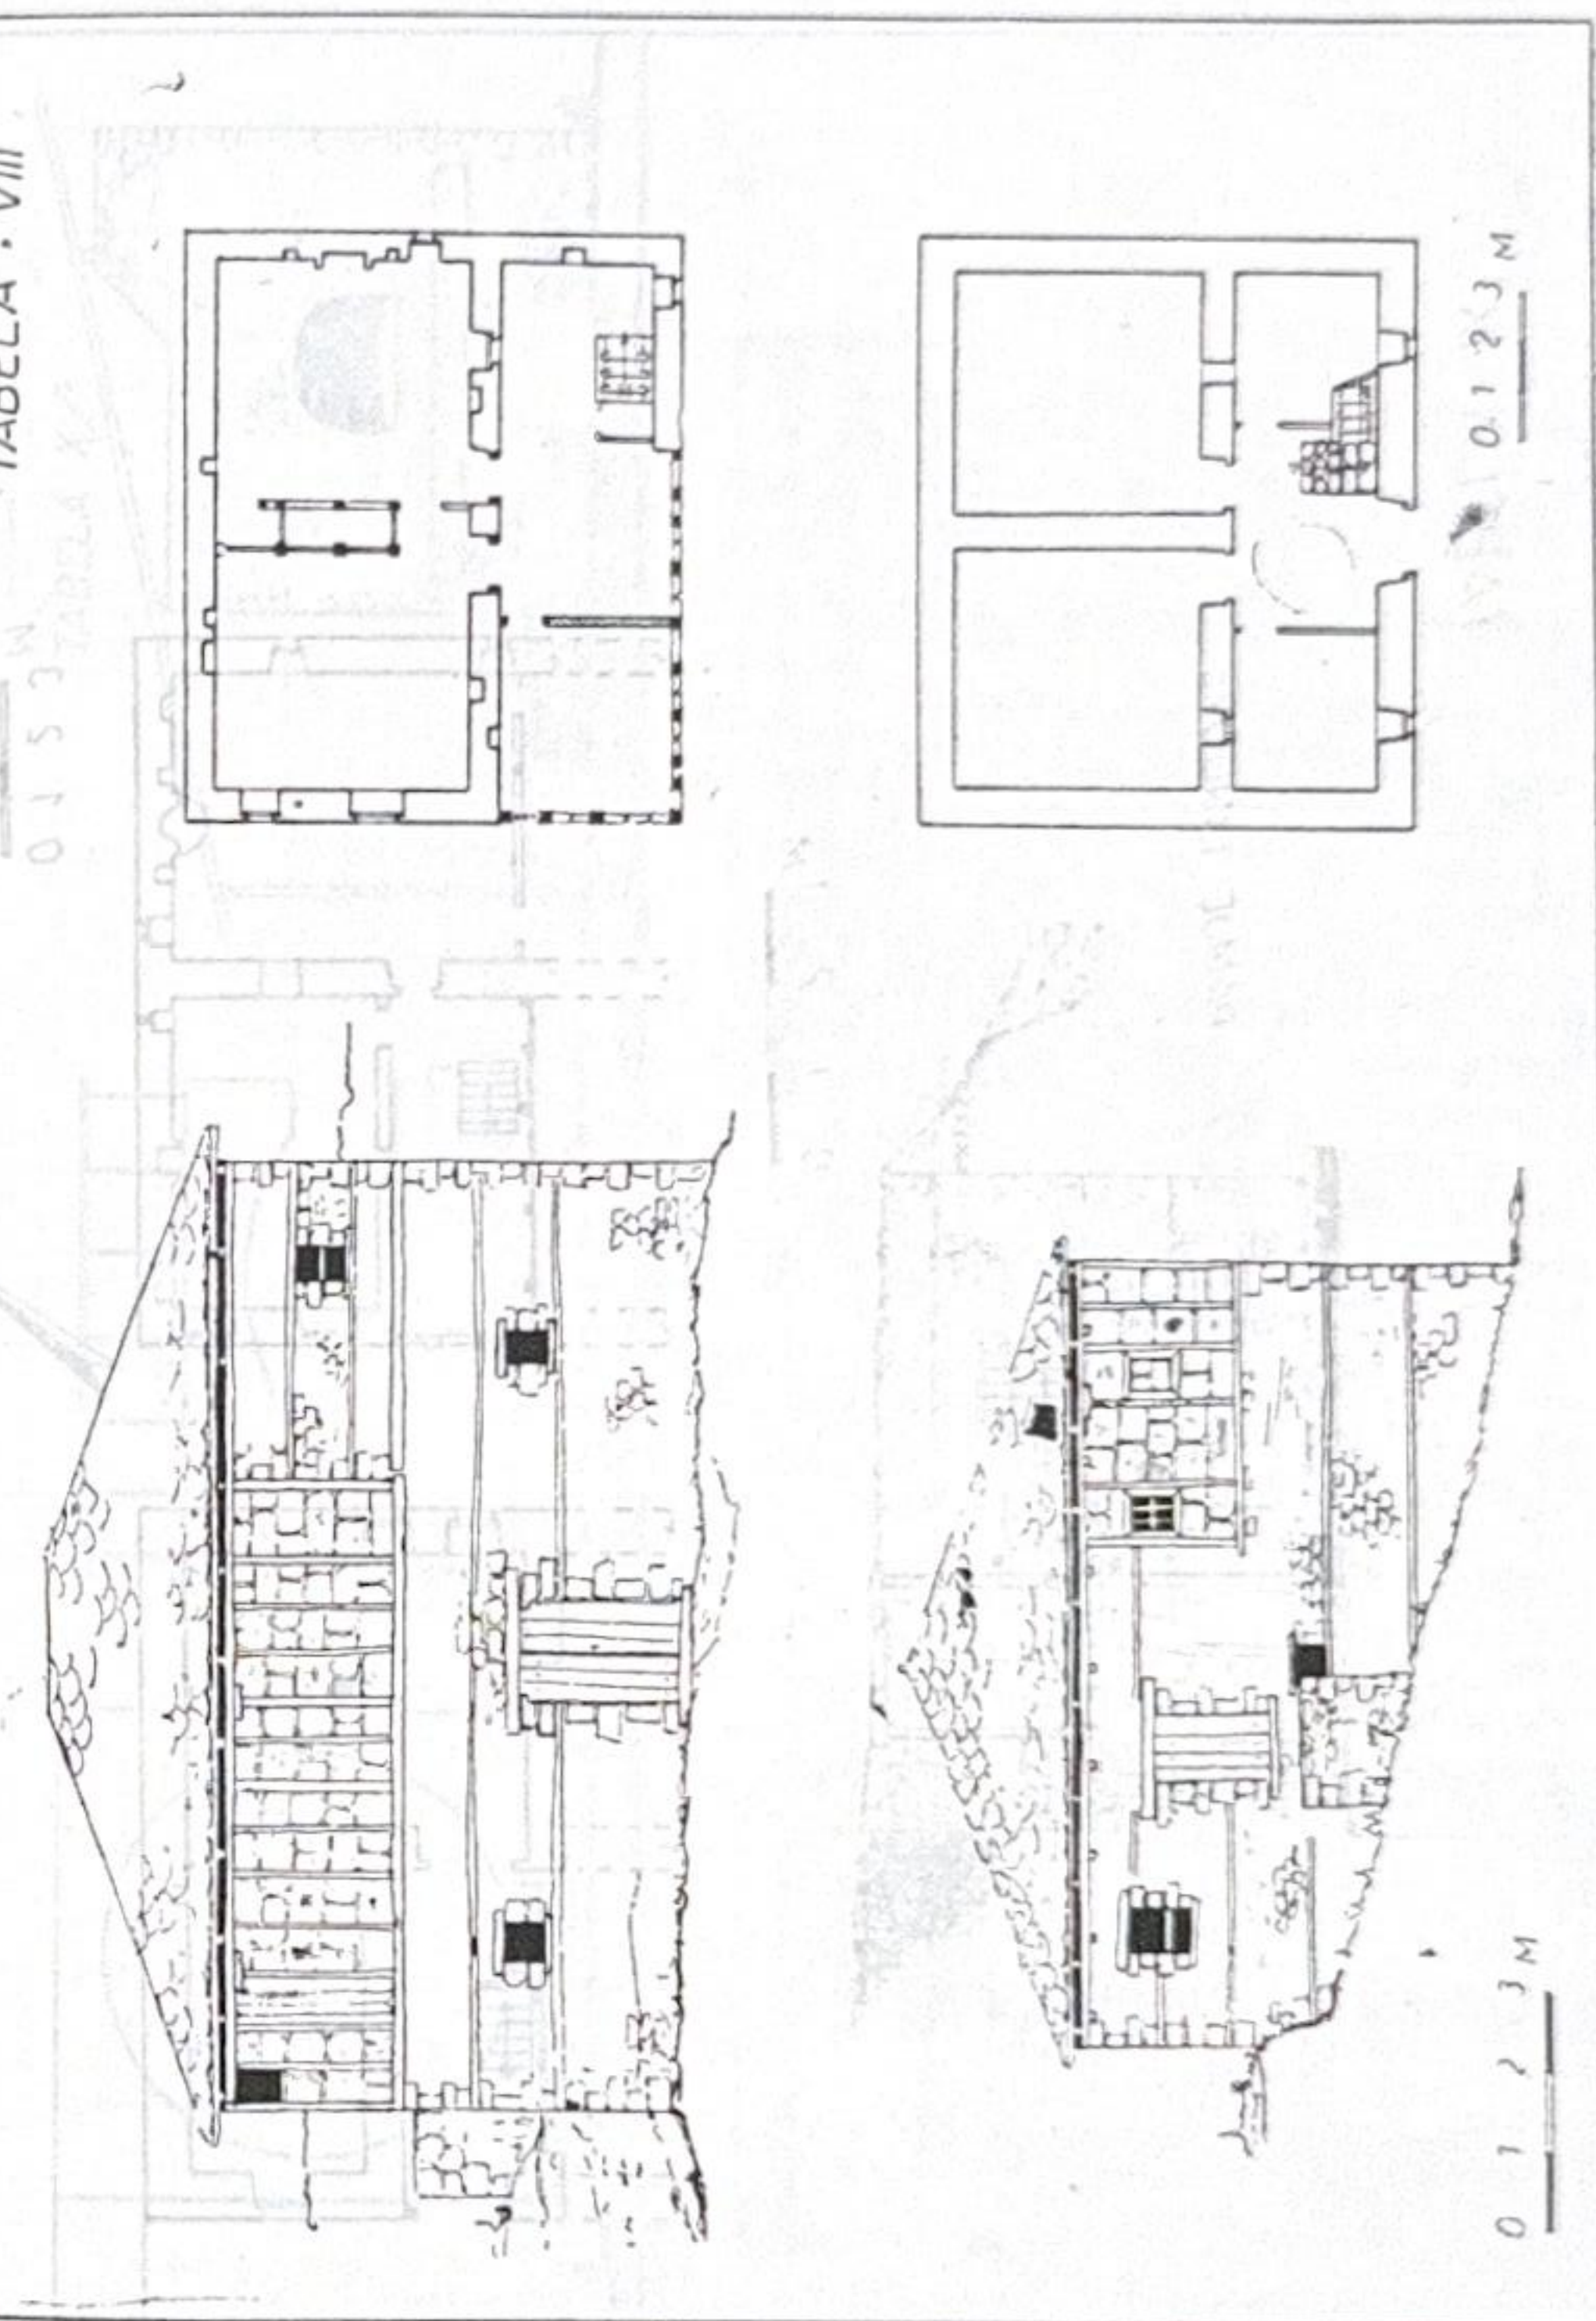


TABELA VIII



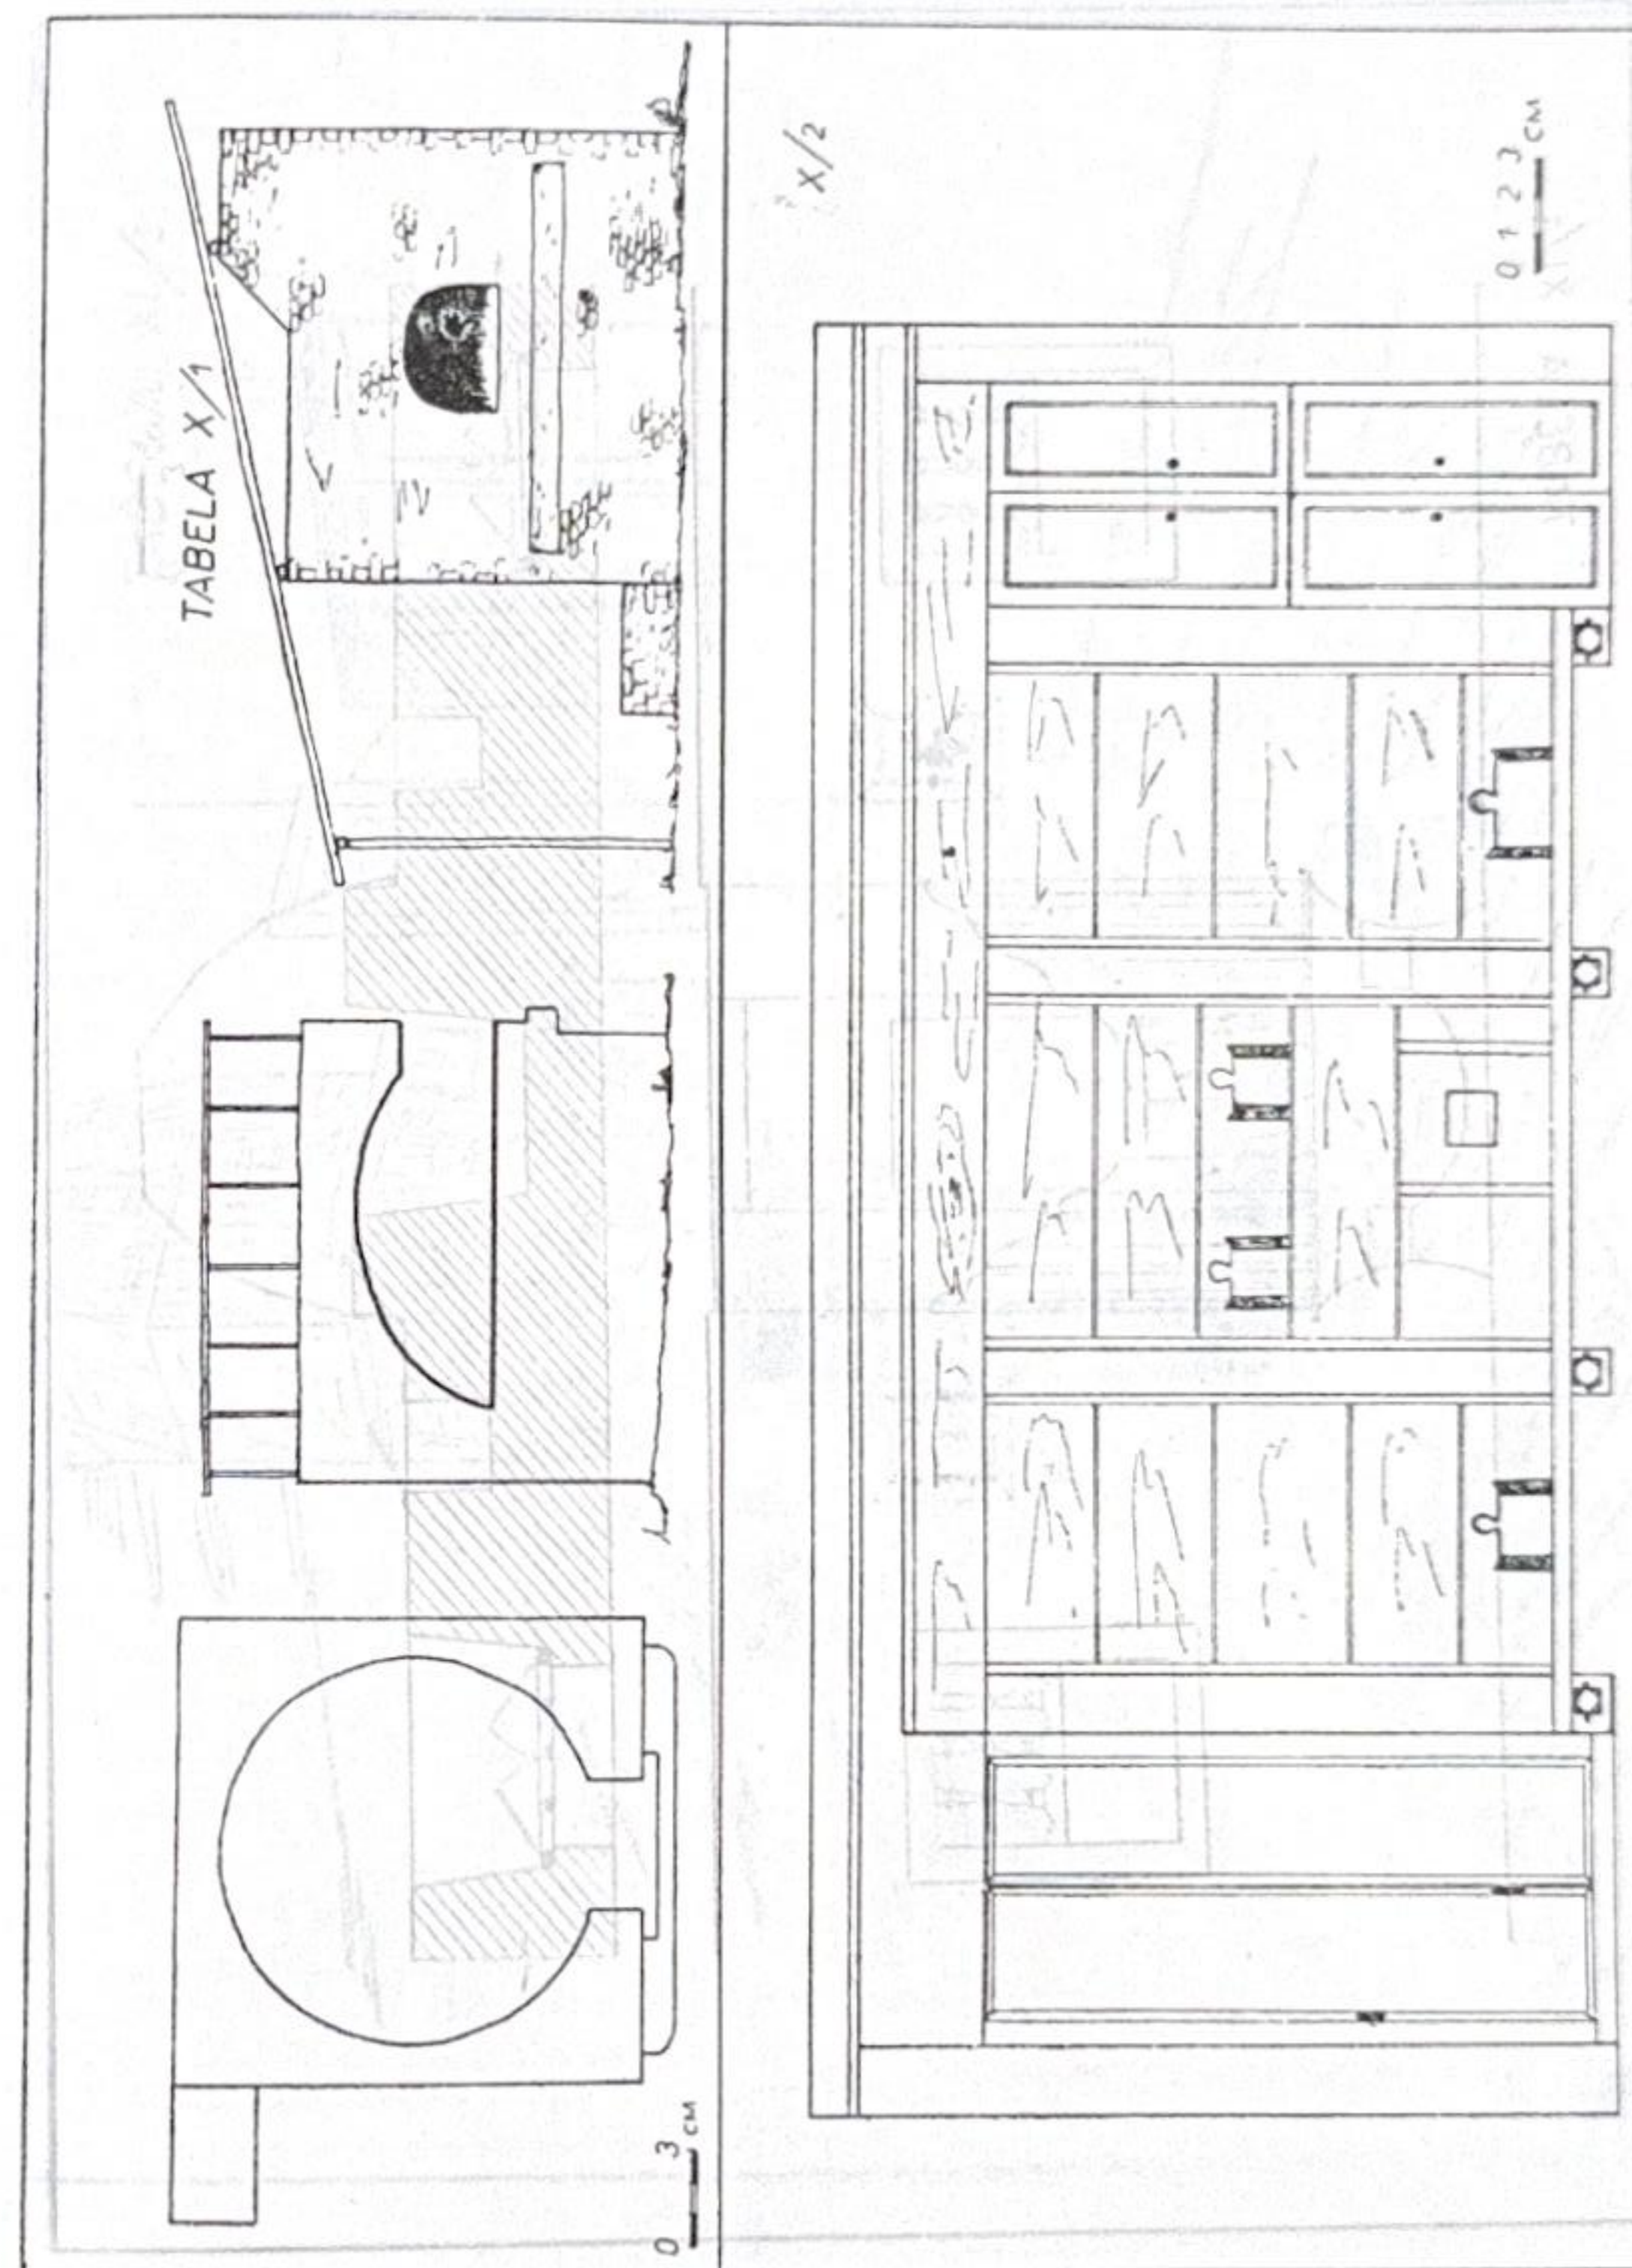
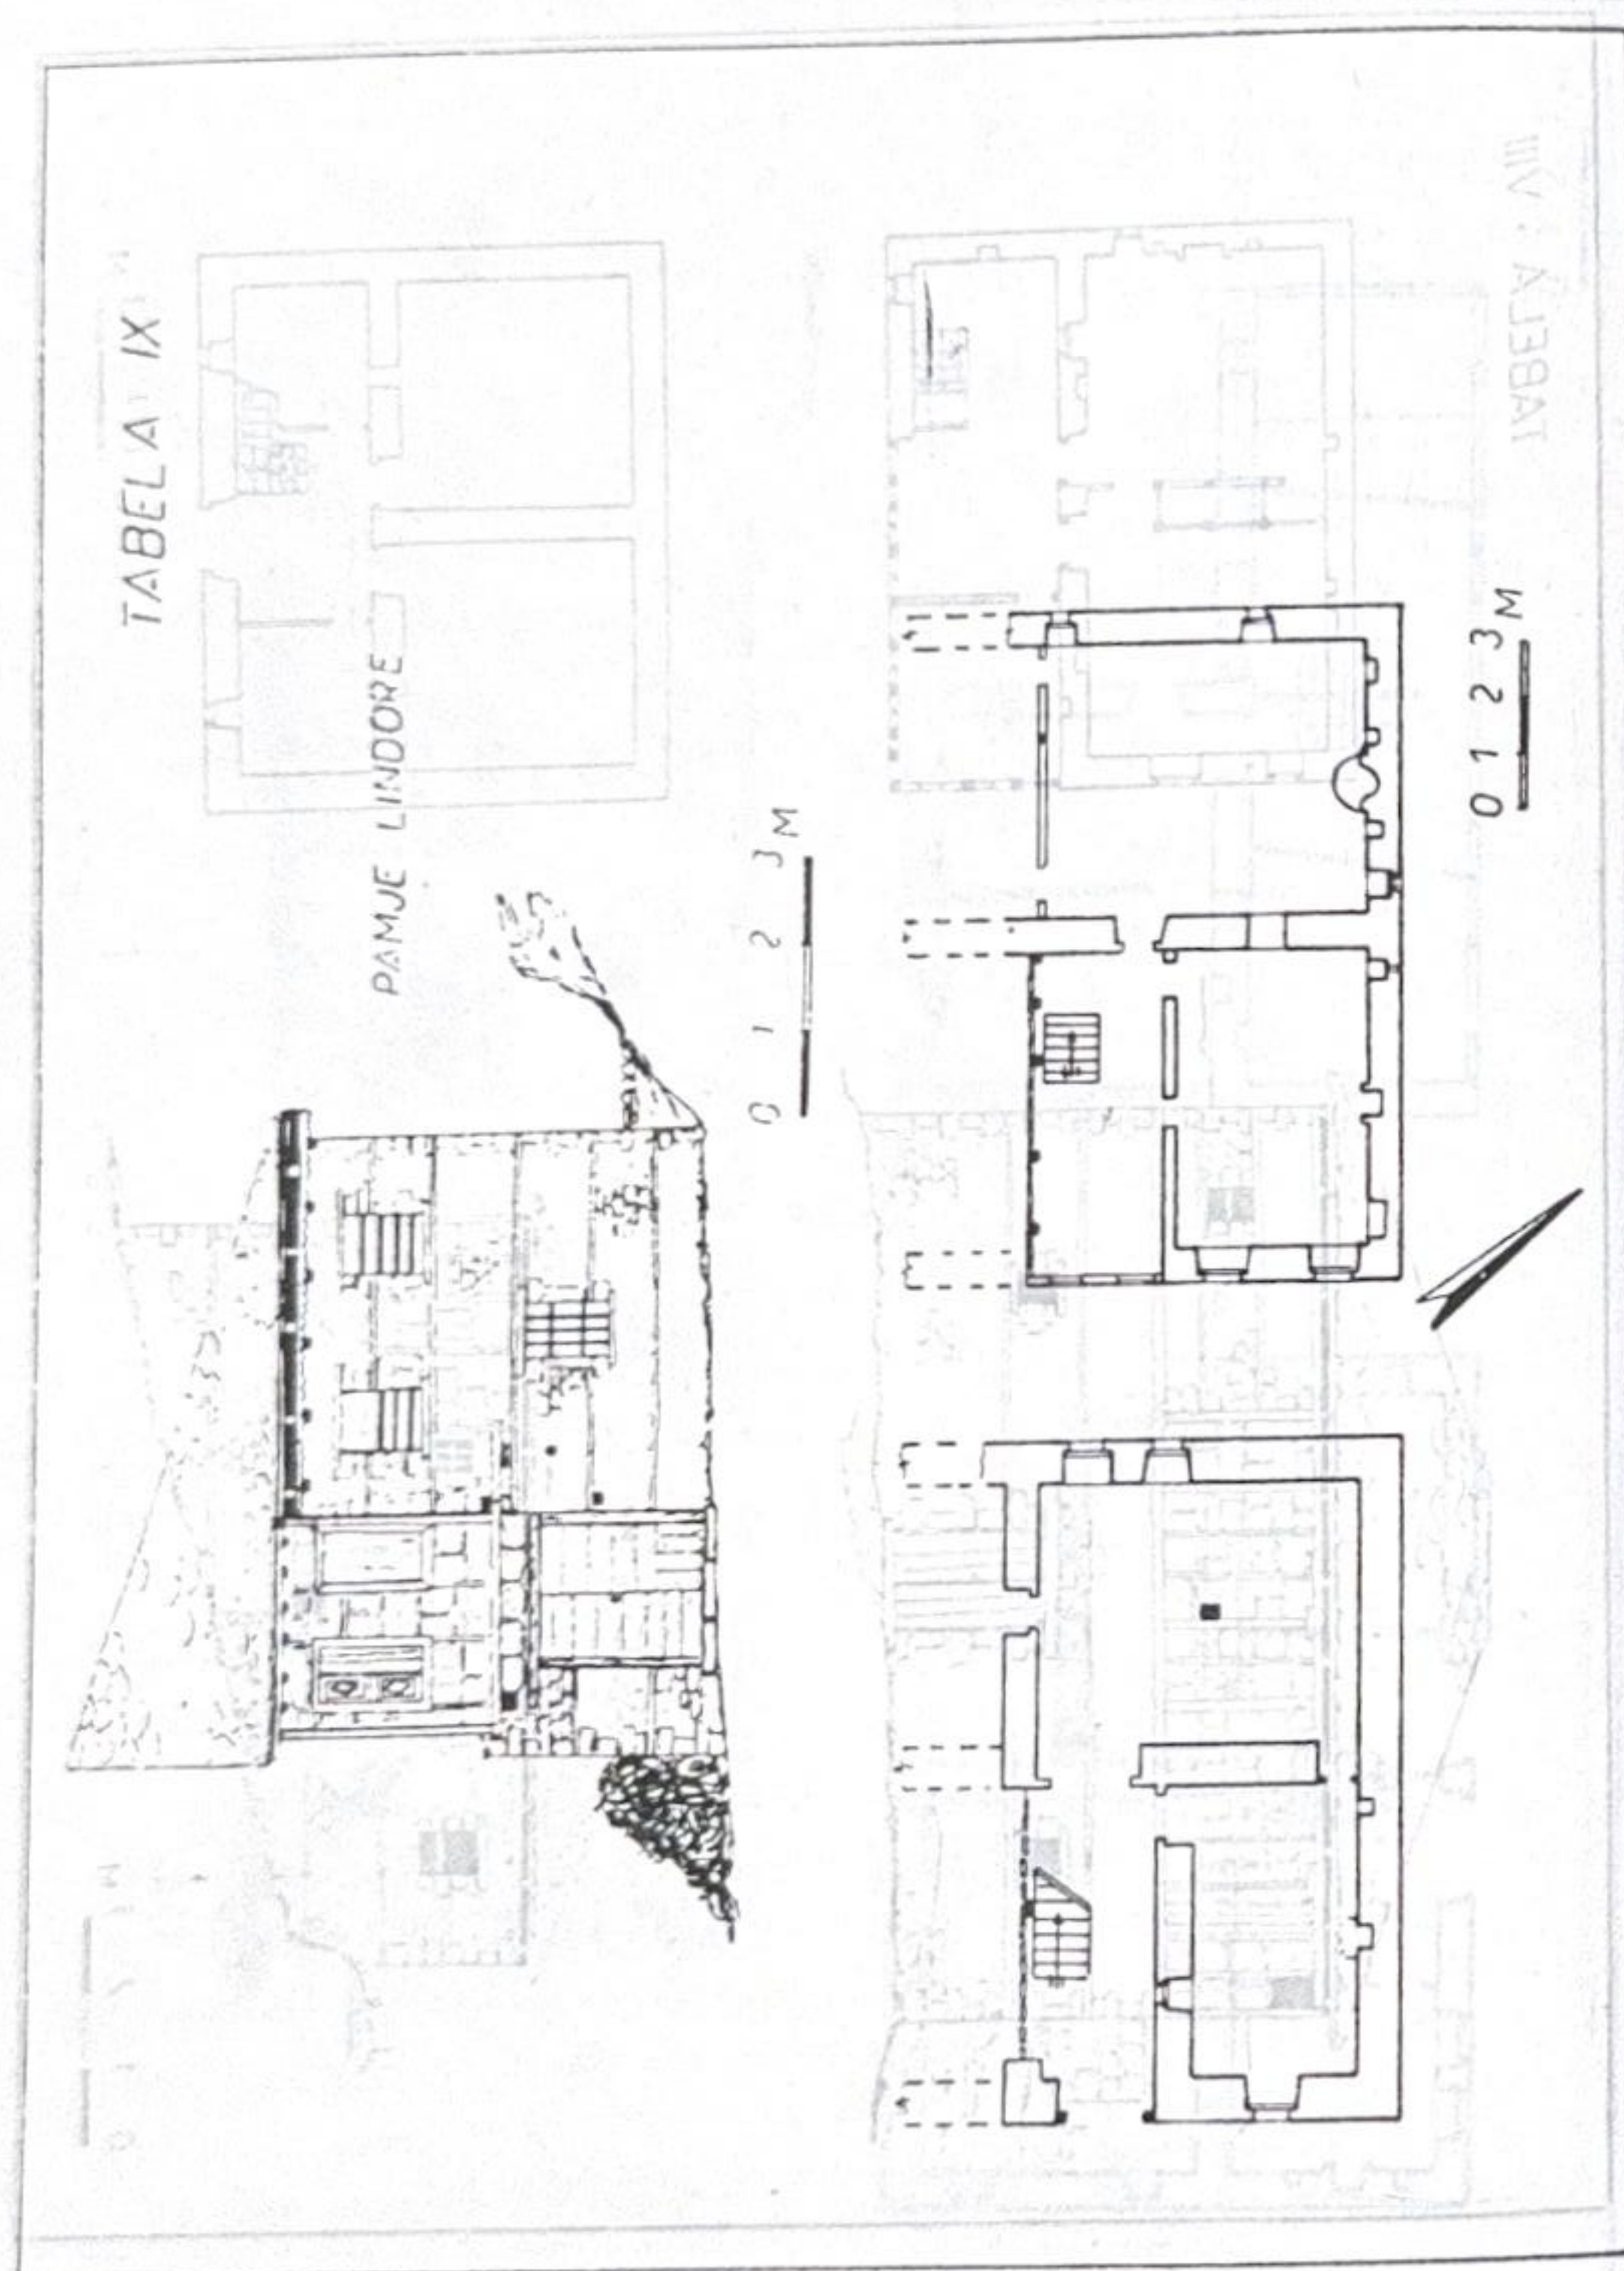


TABELA XI/1

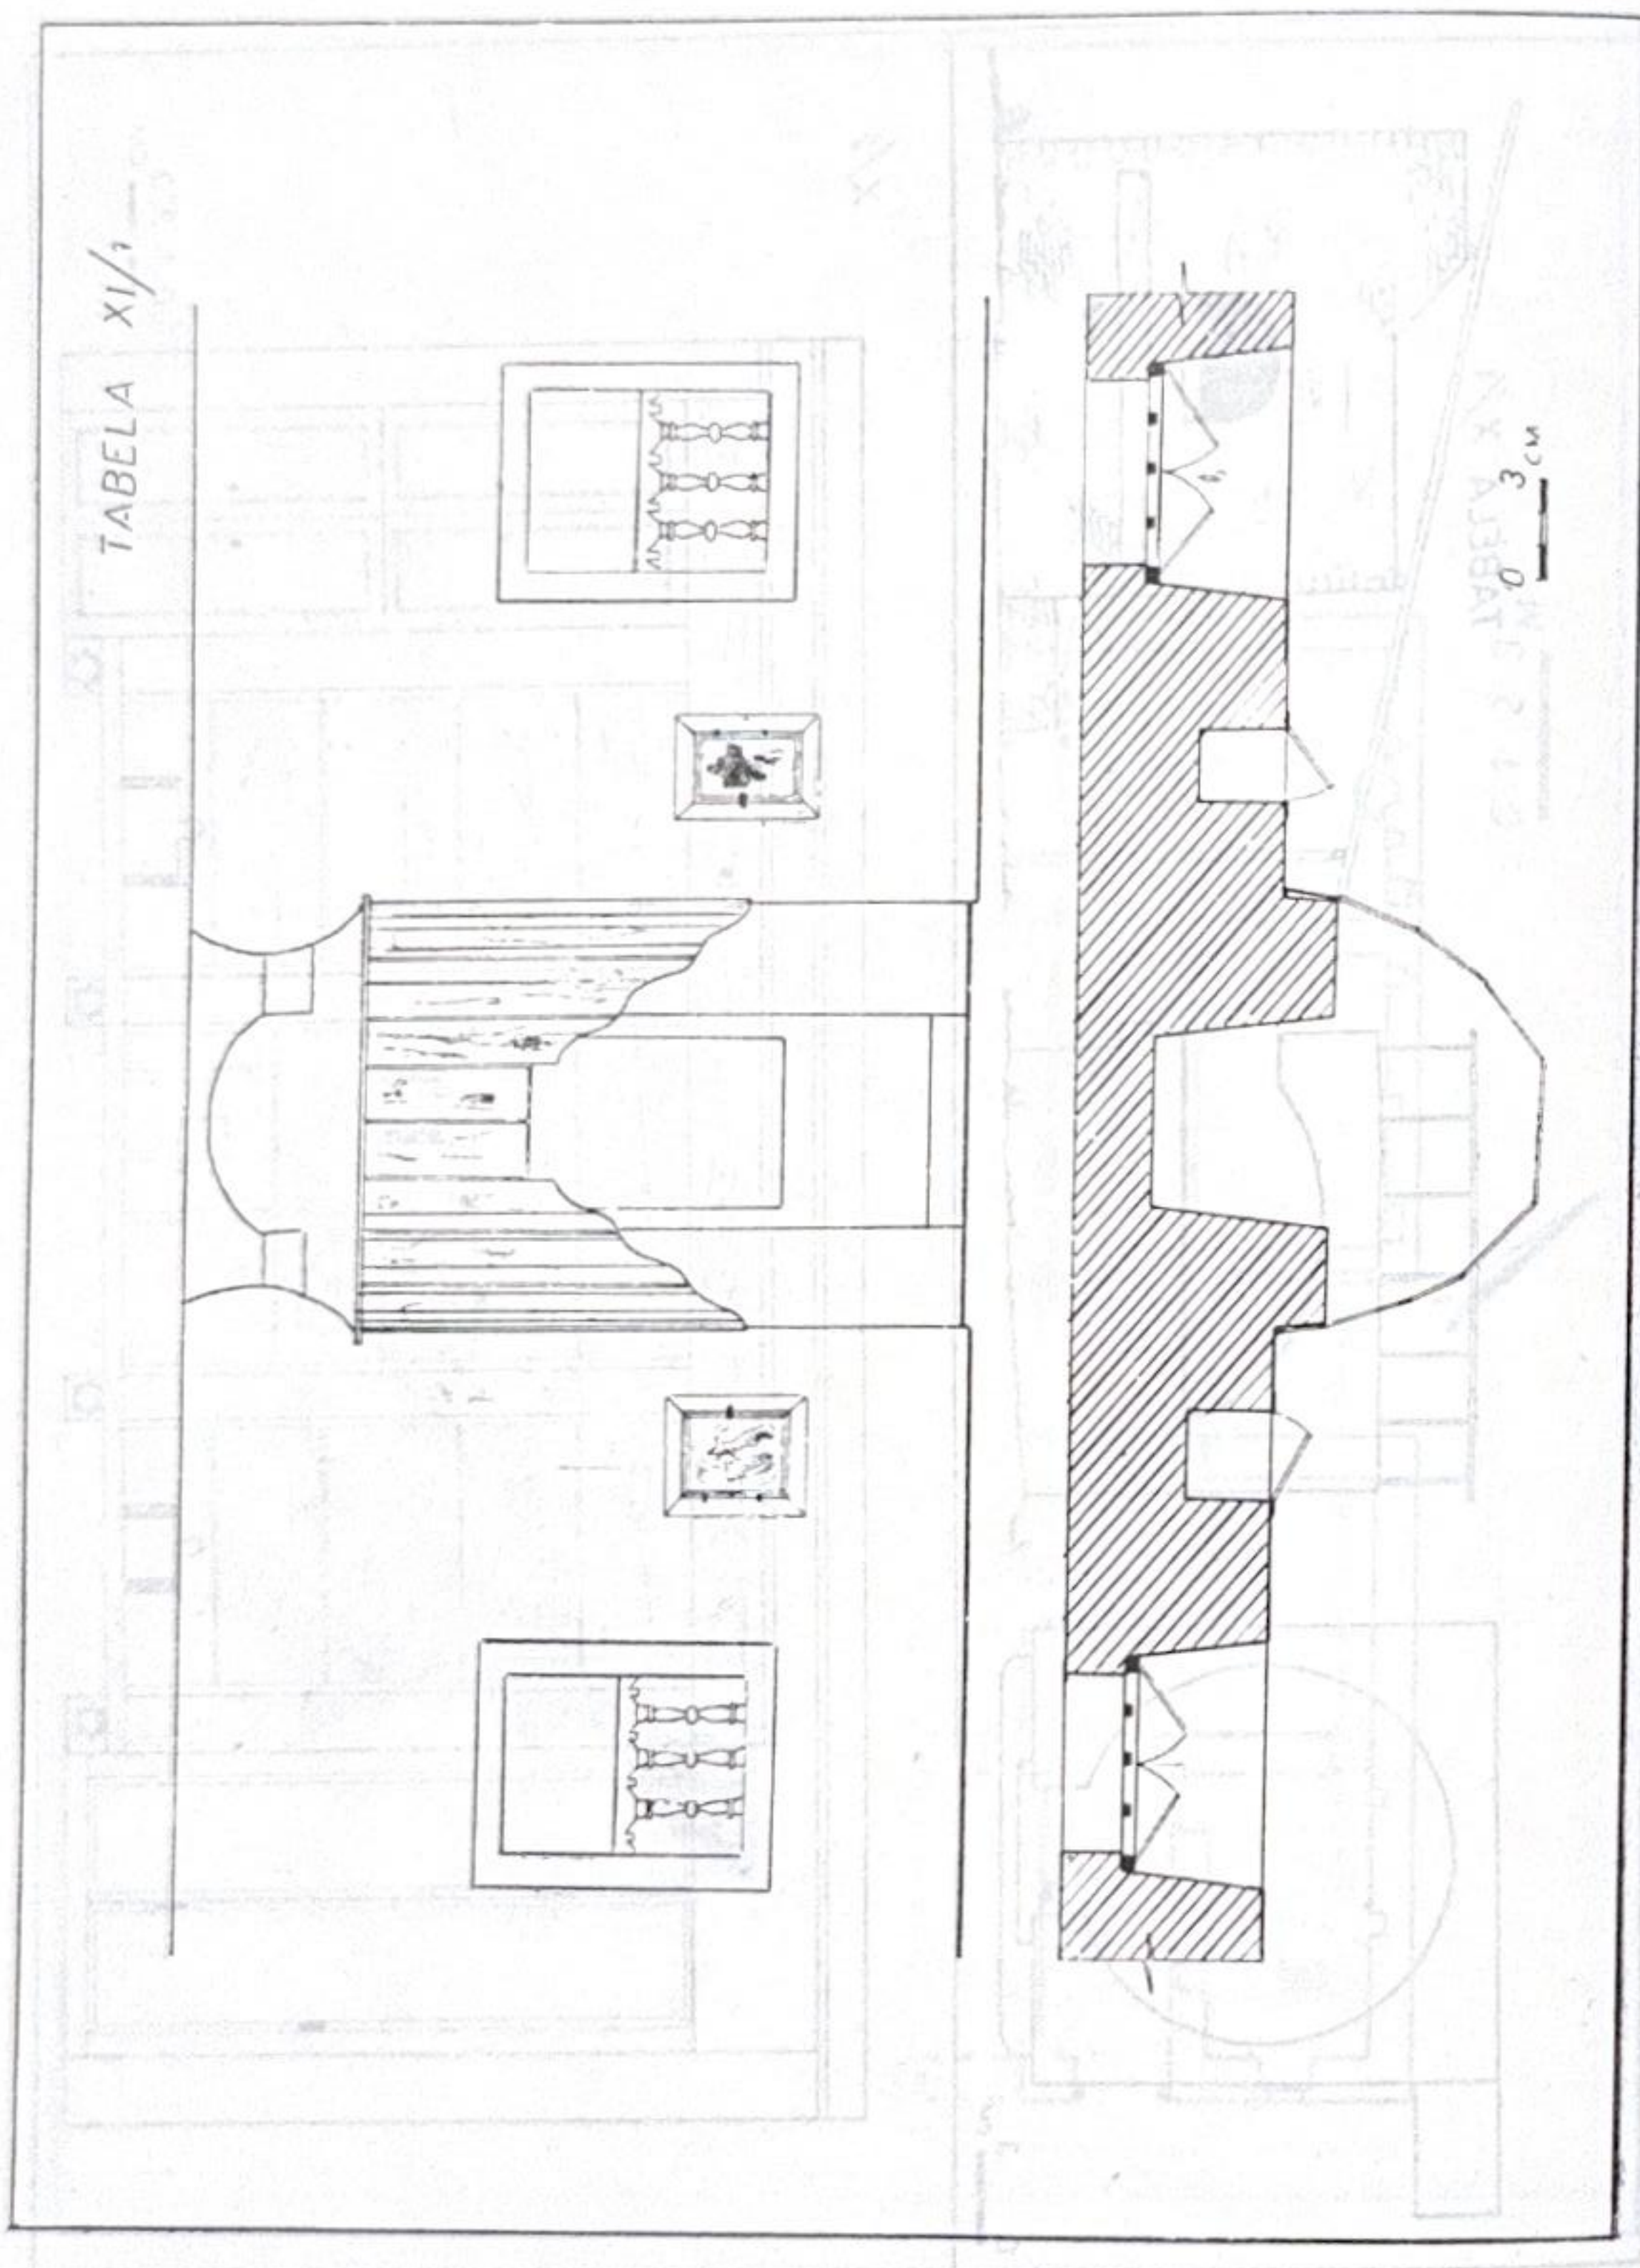
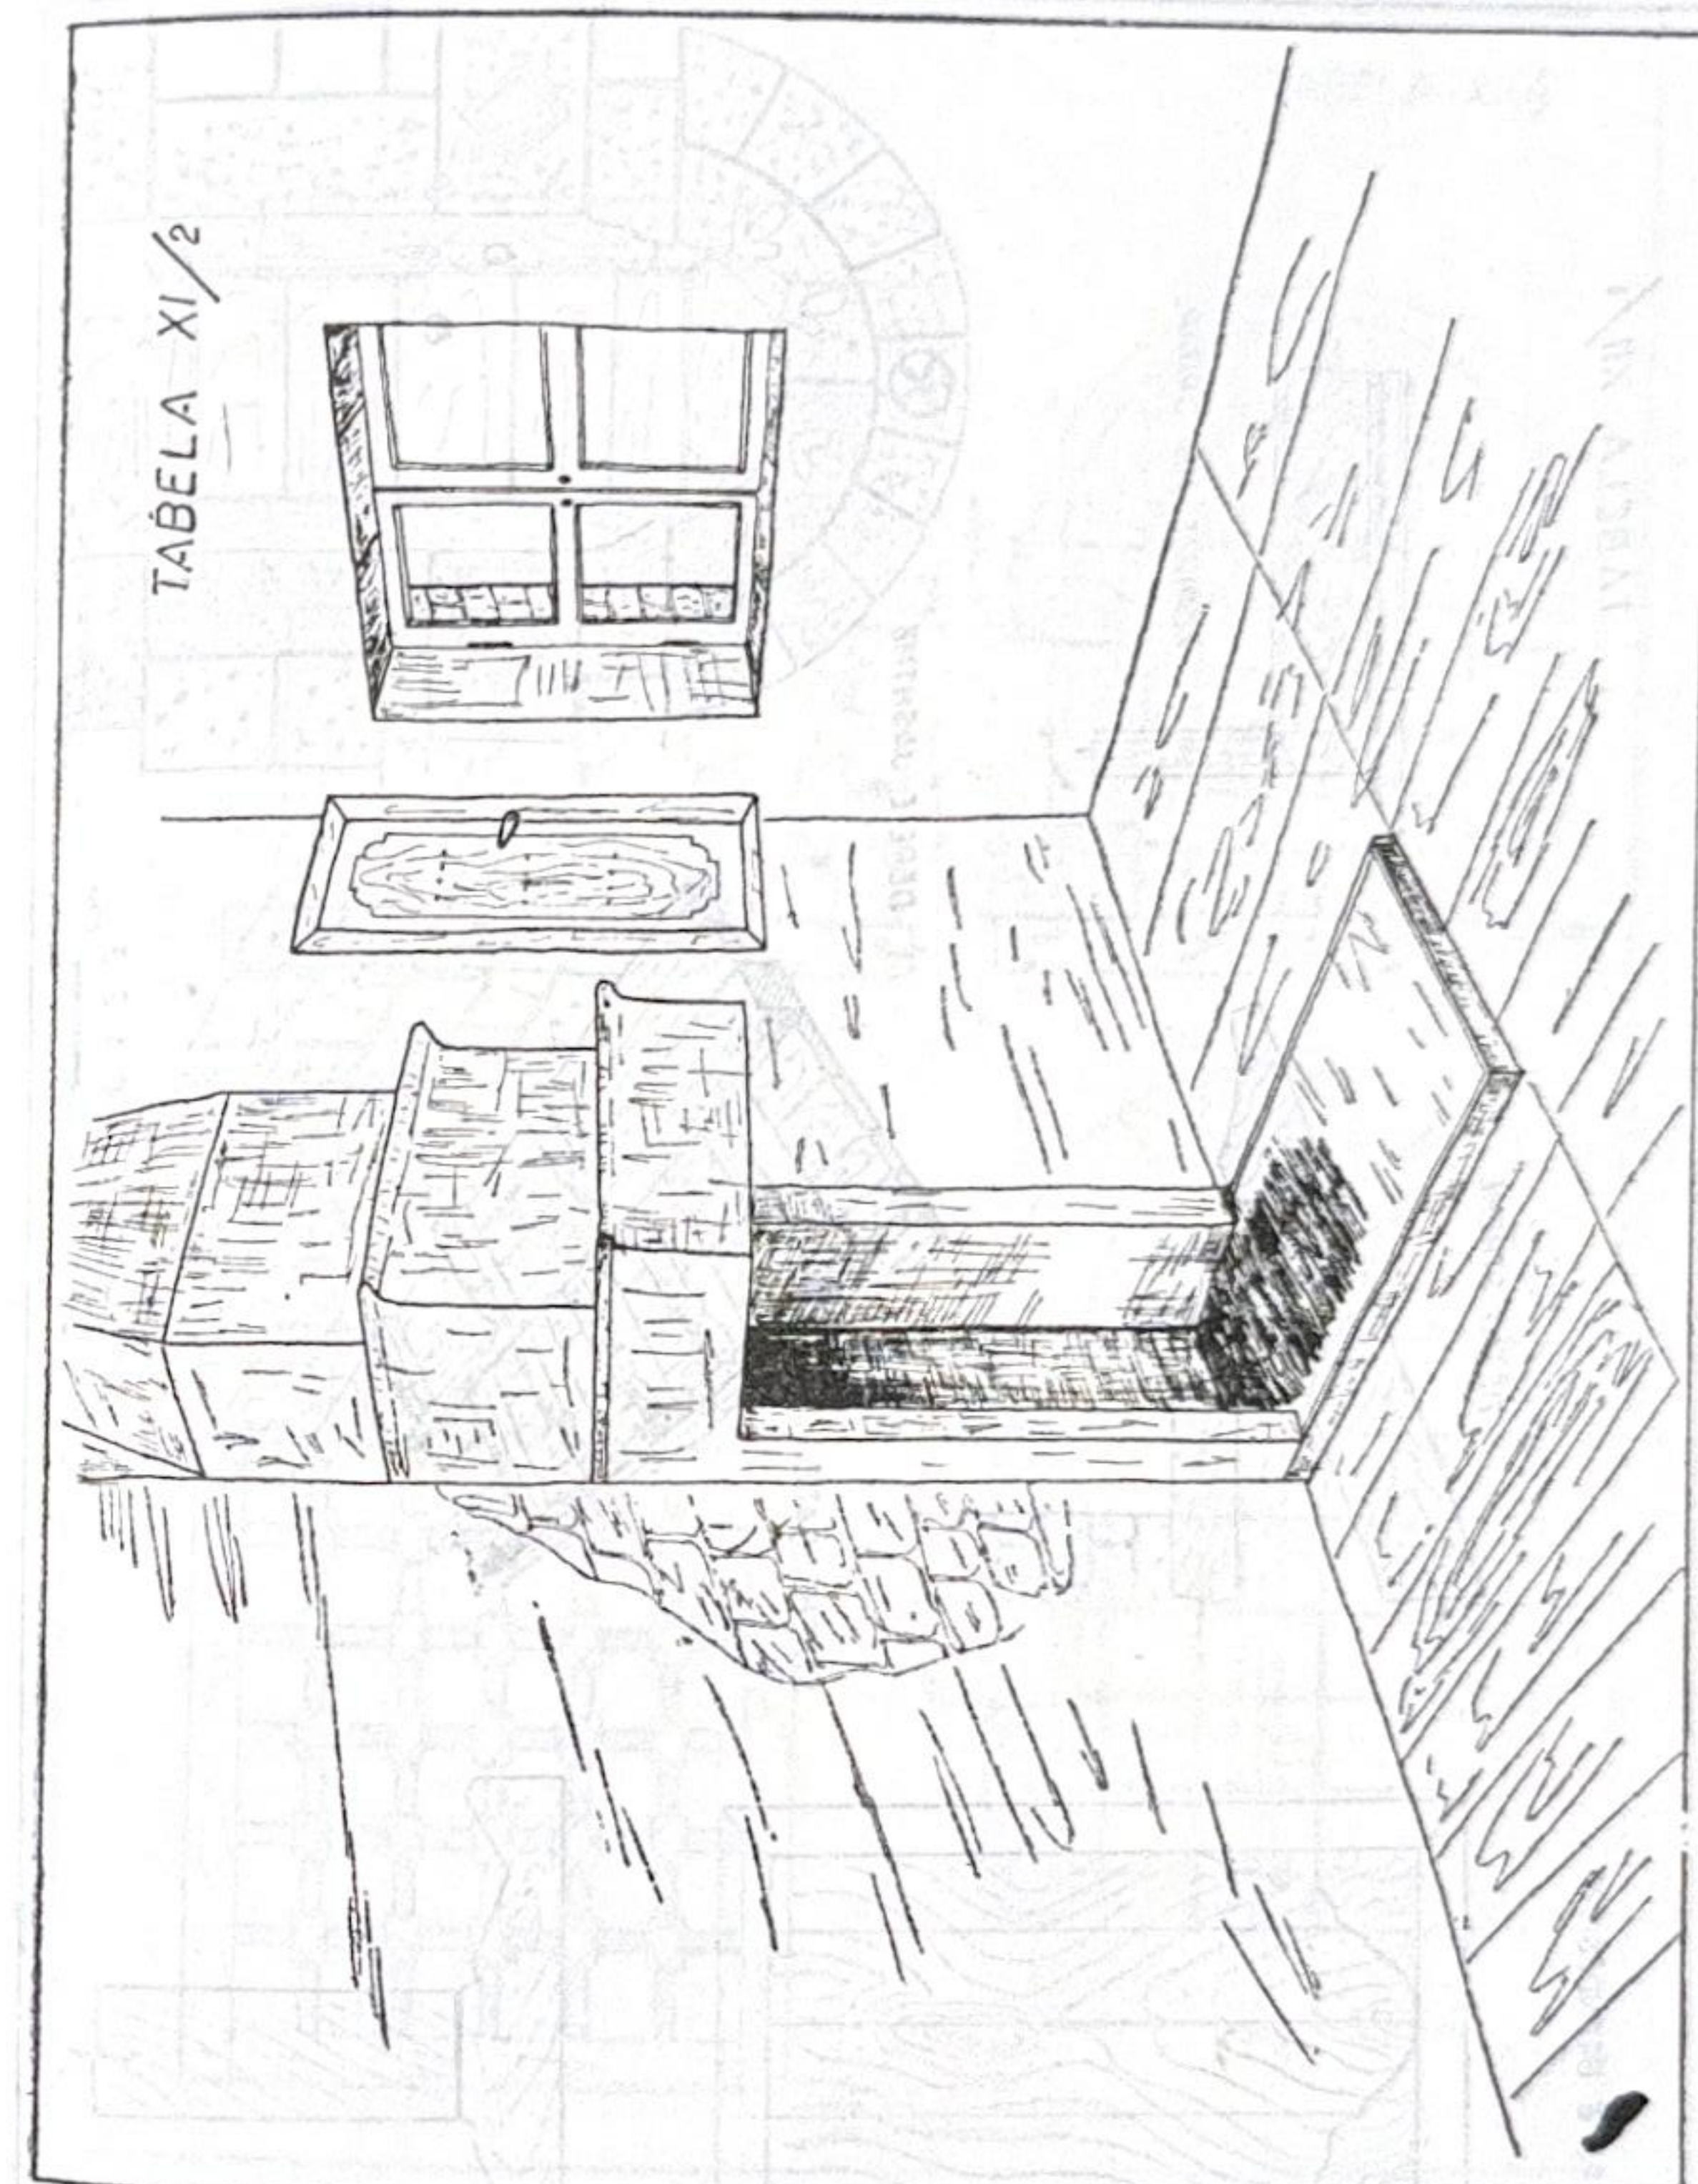


TABELA XI/2



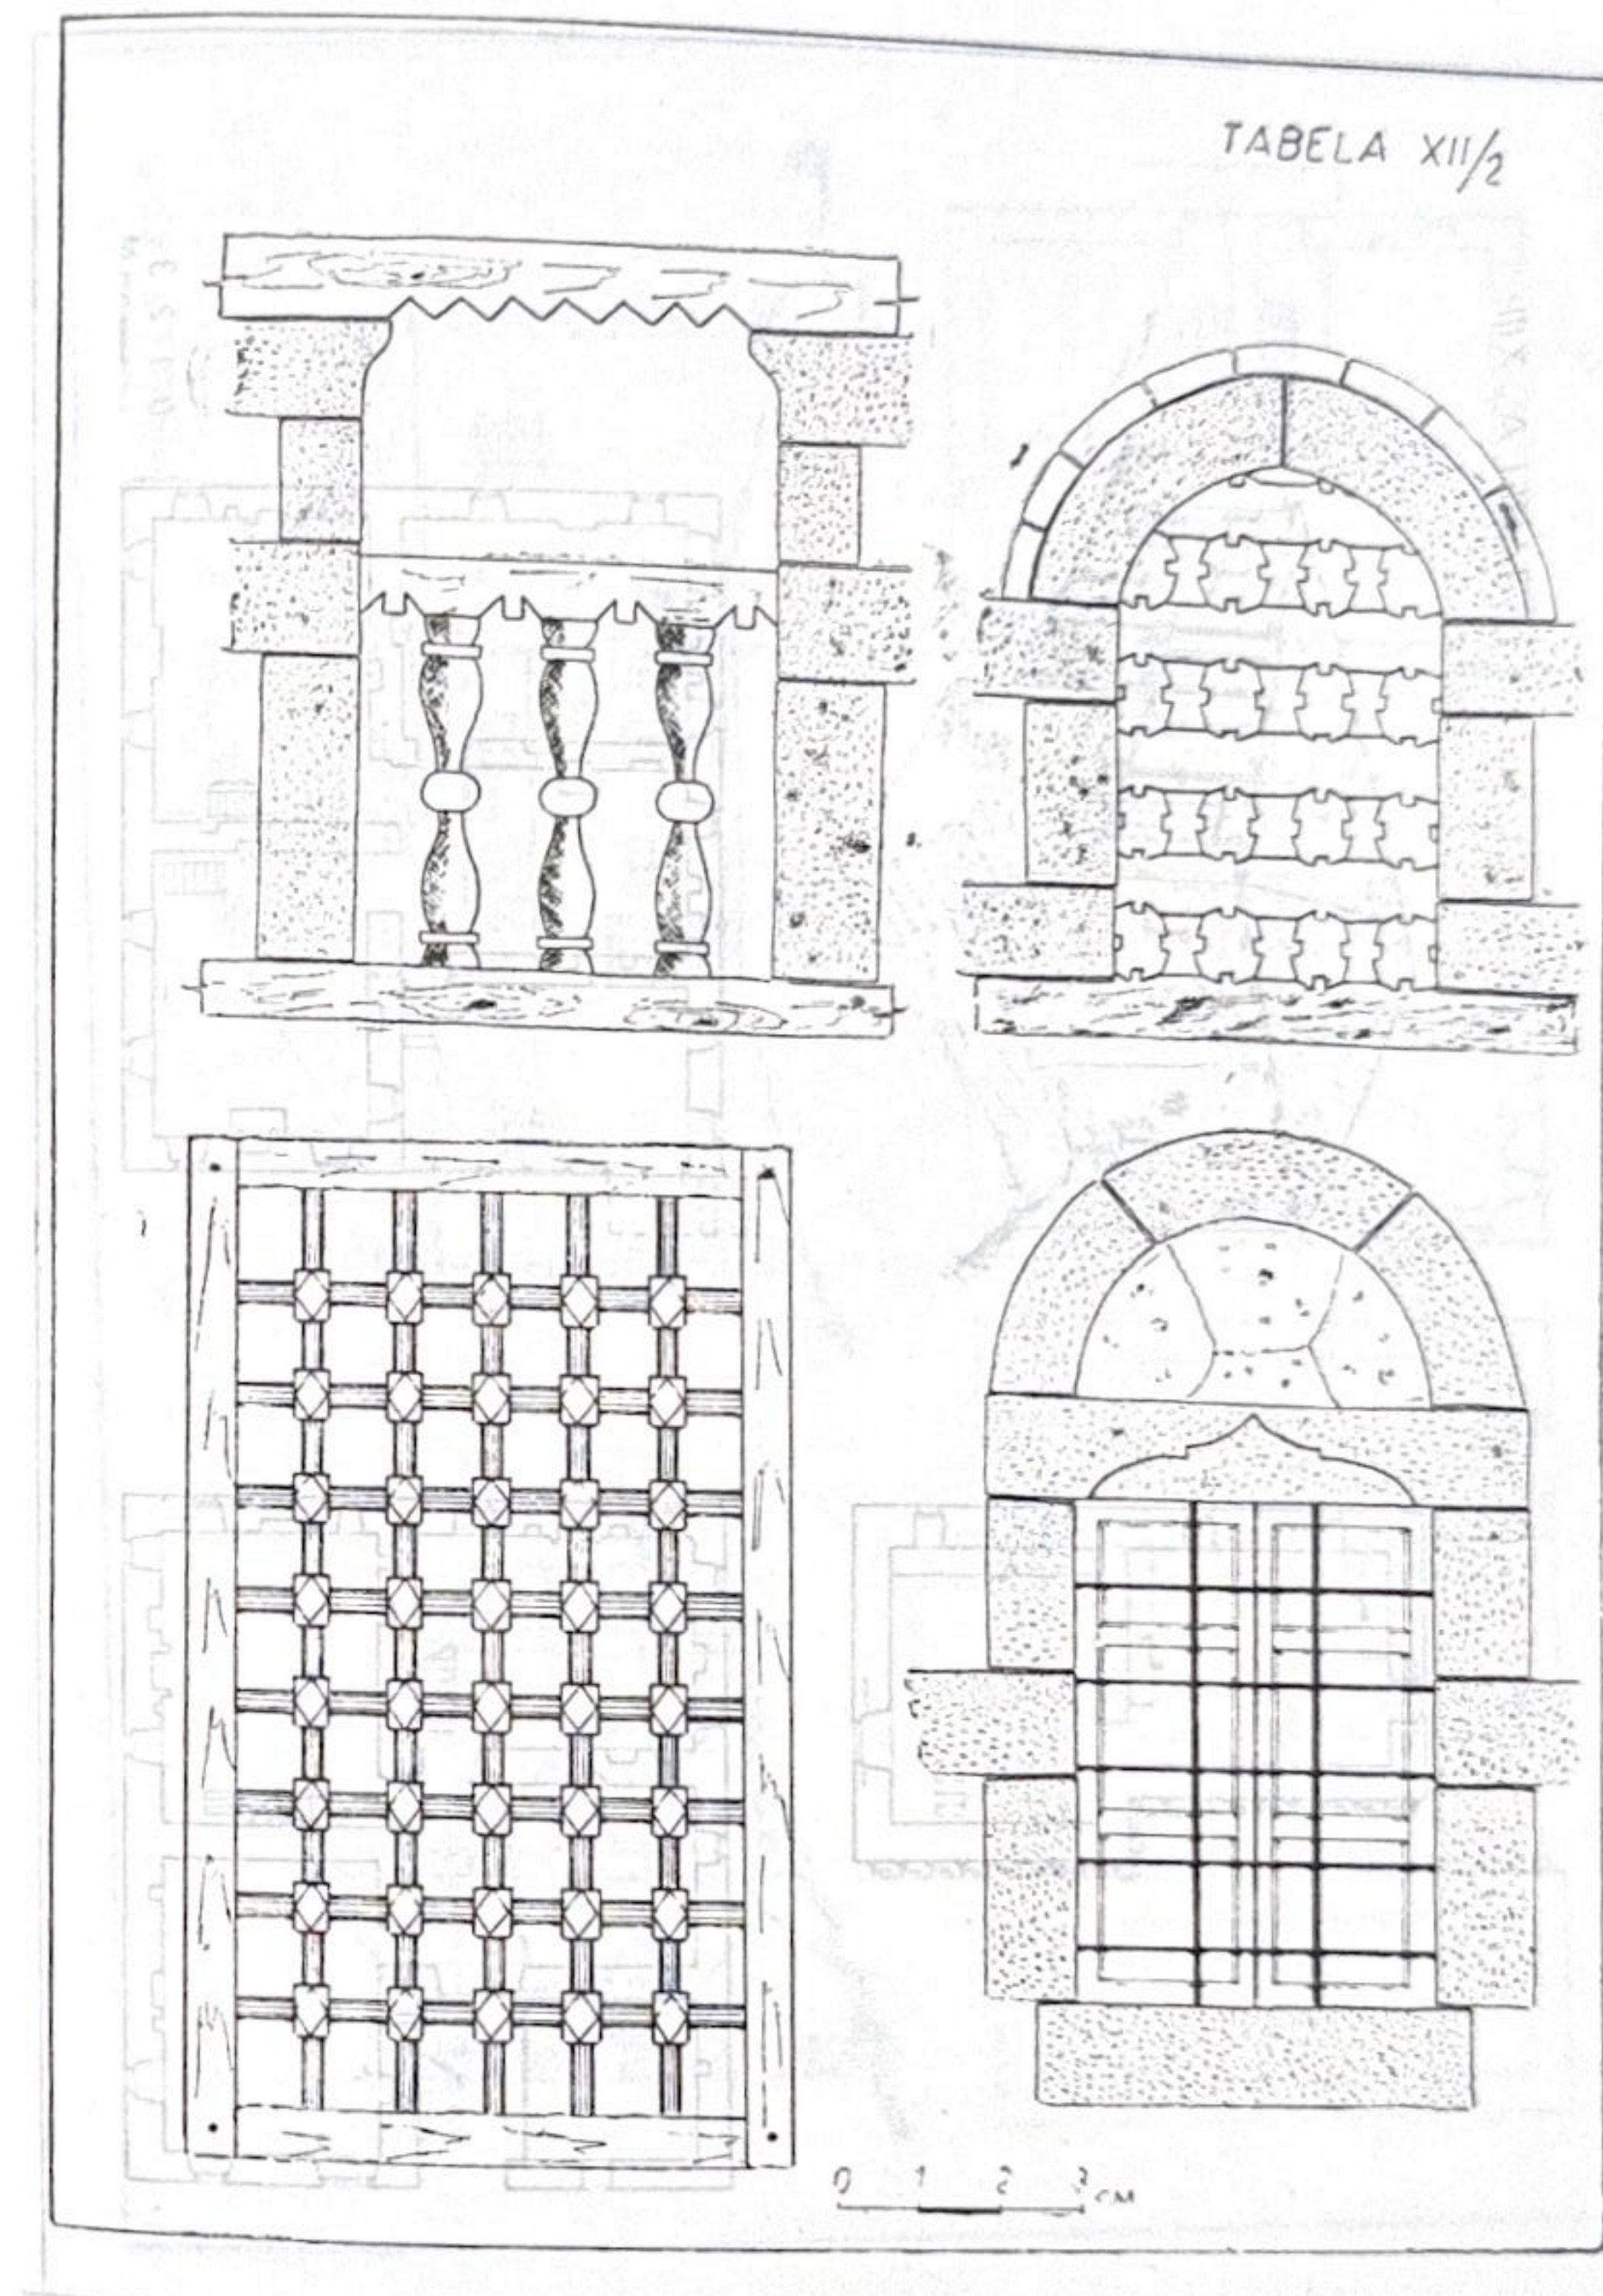
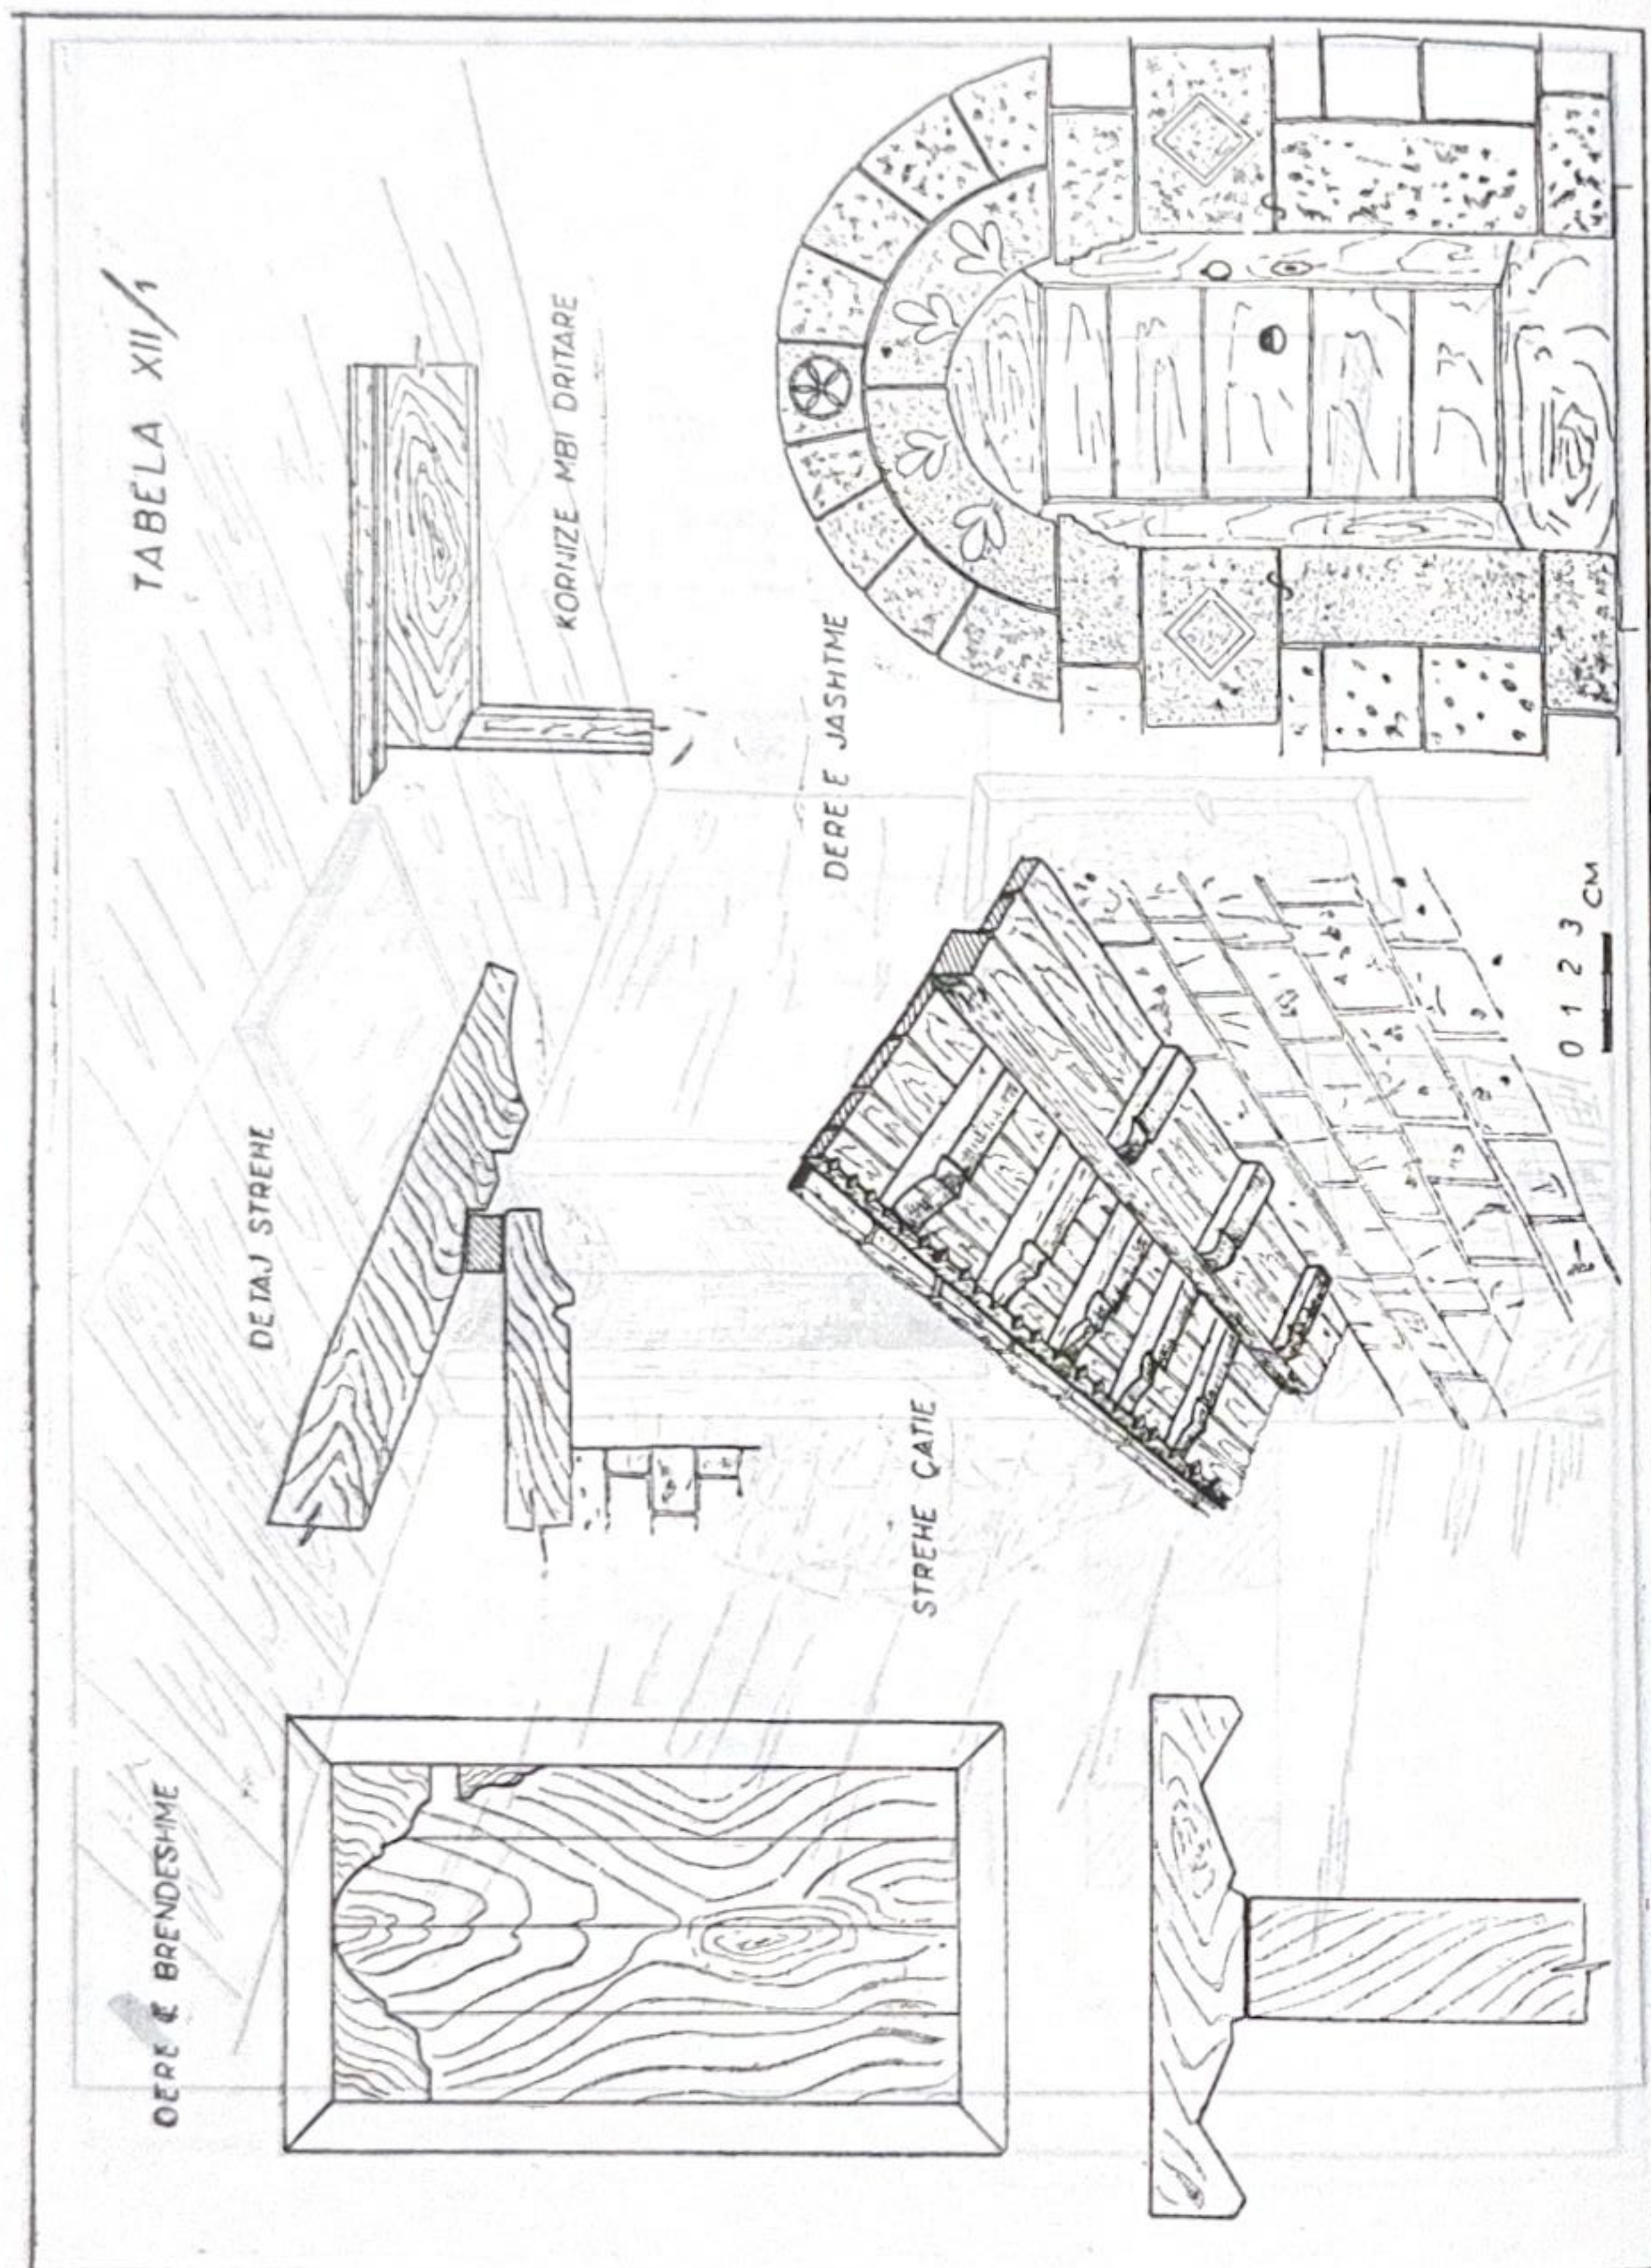
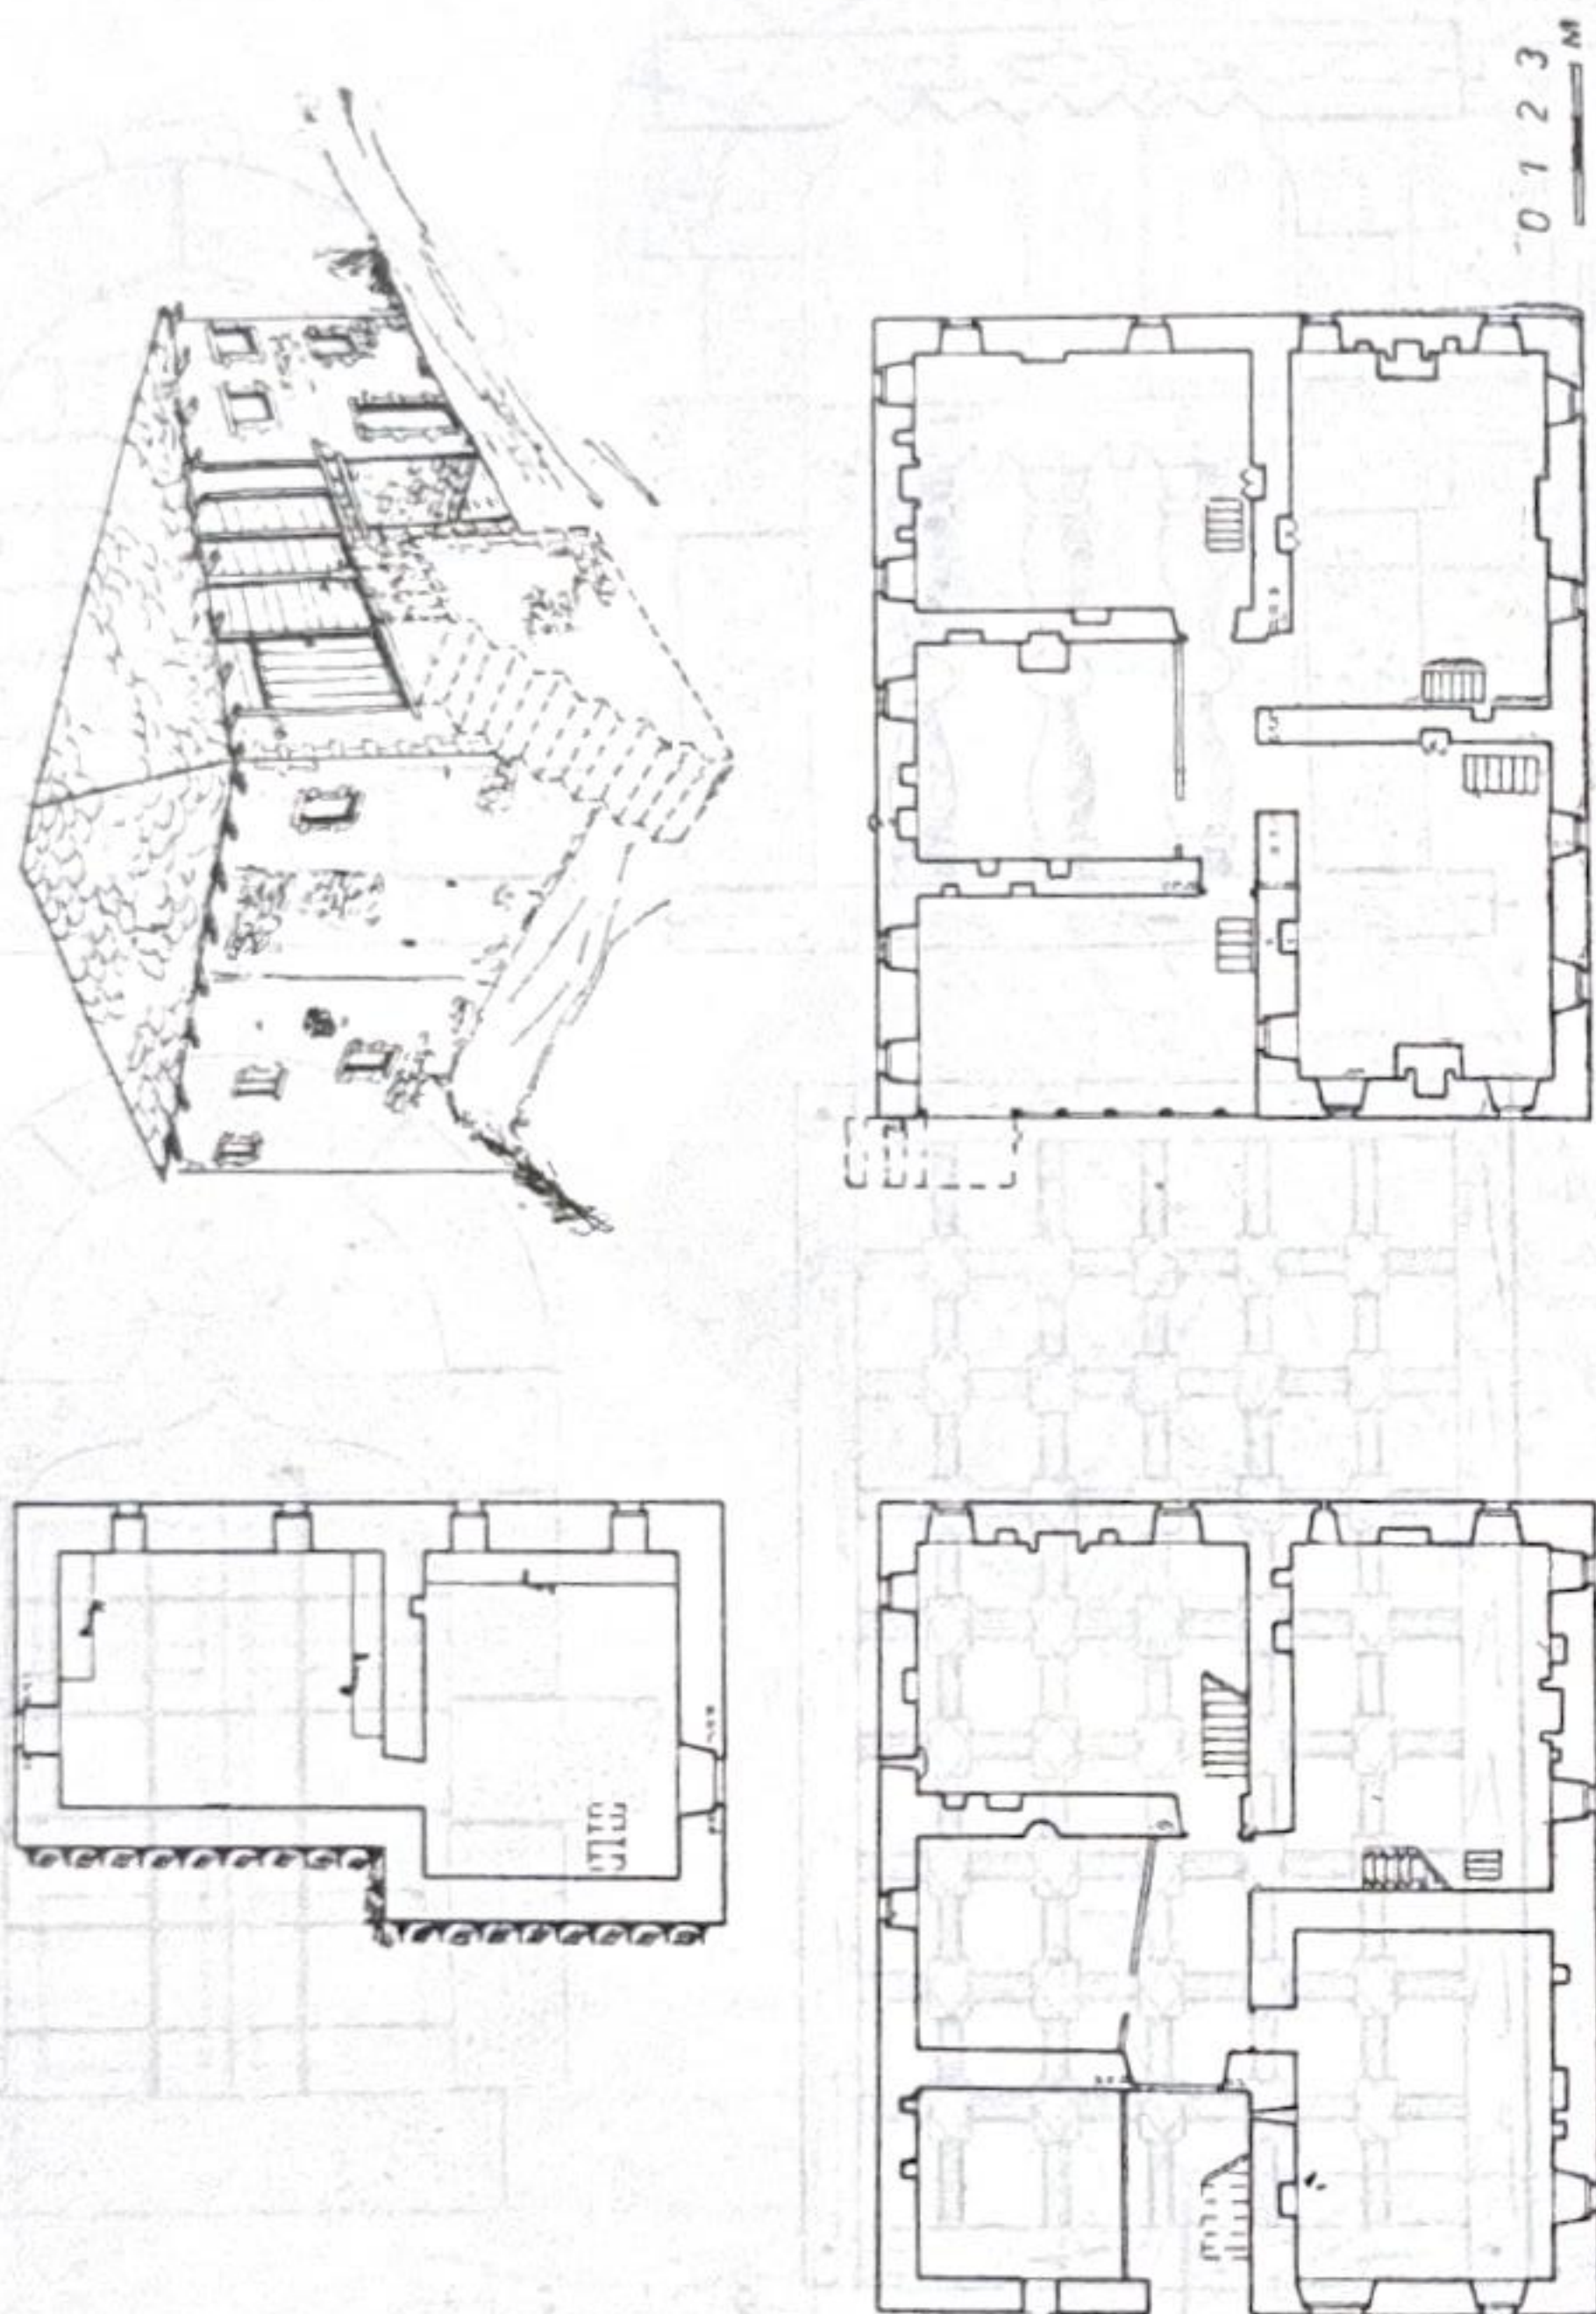
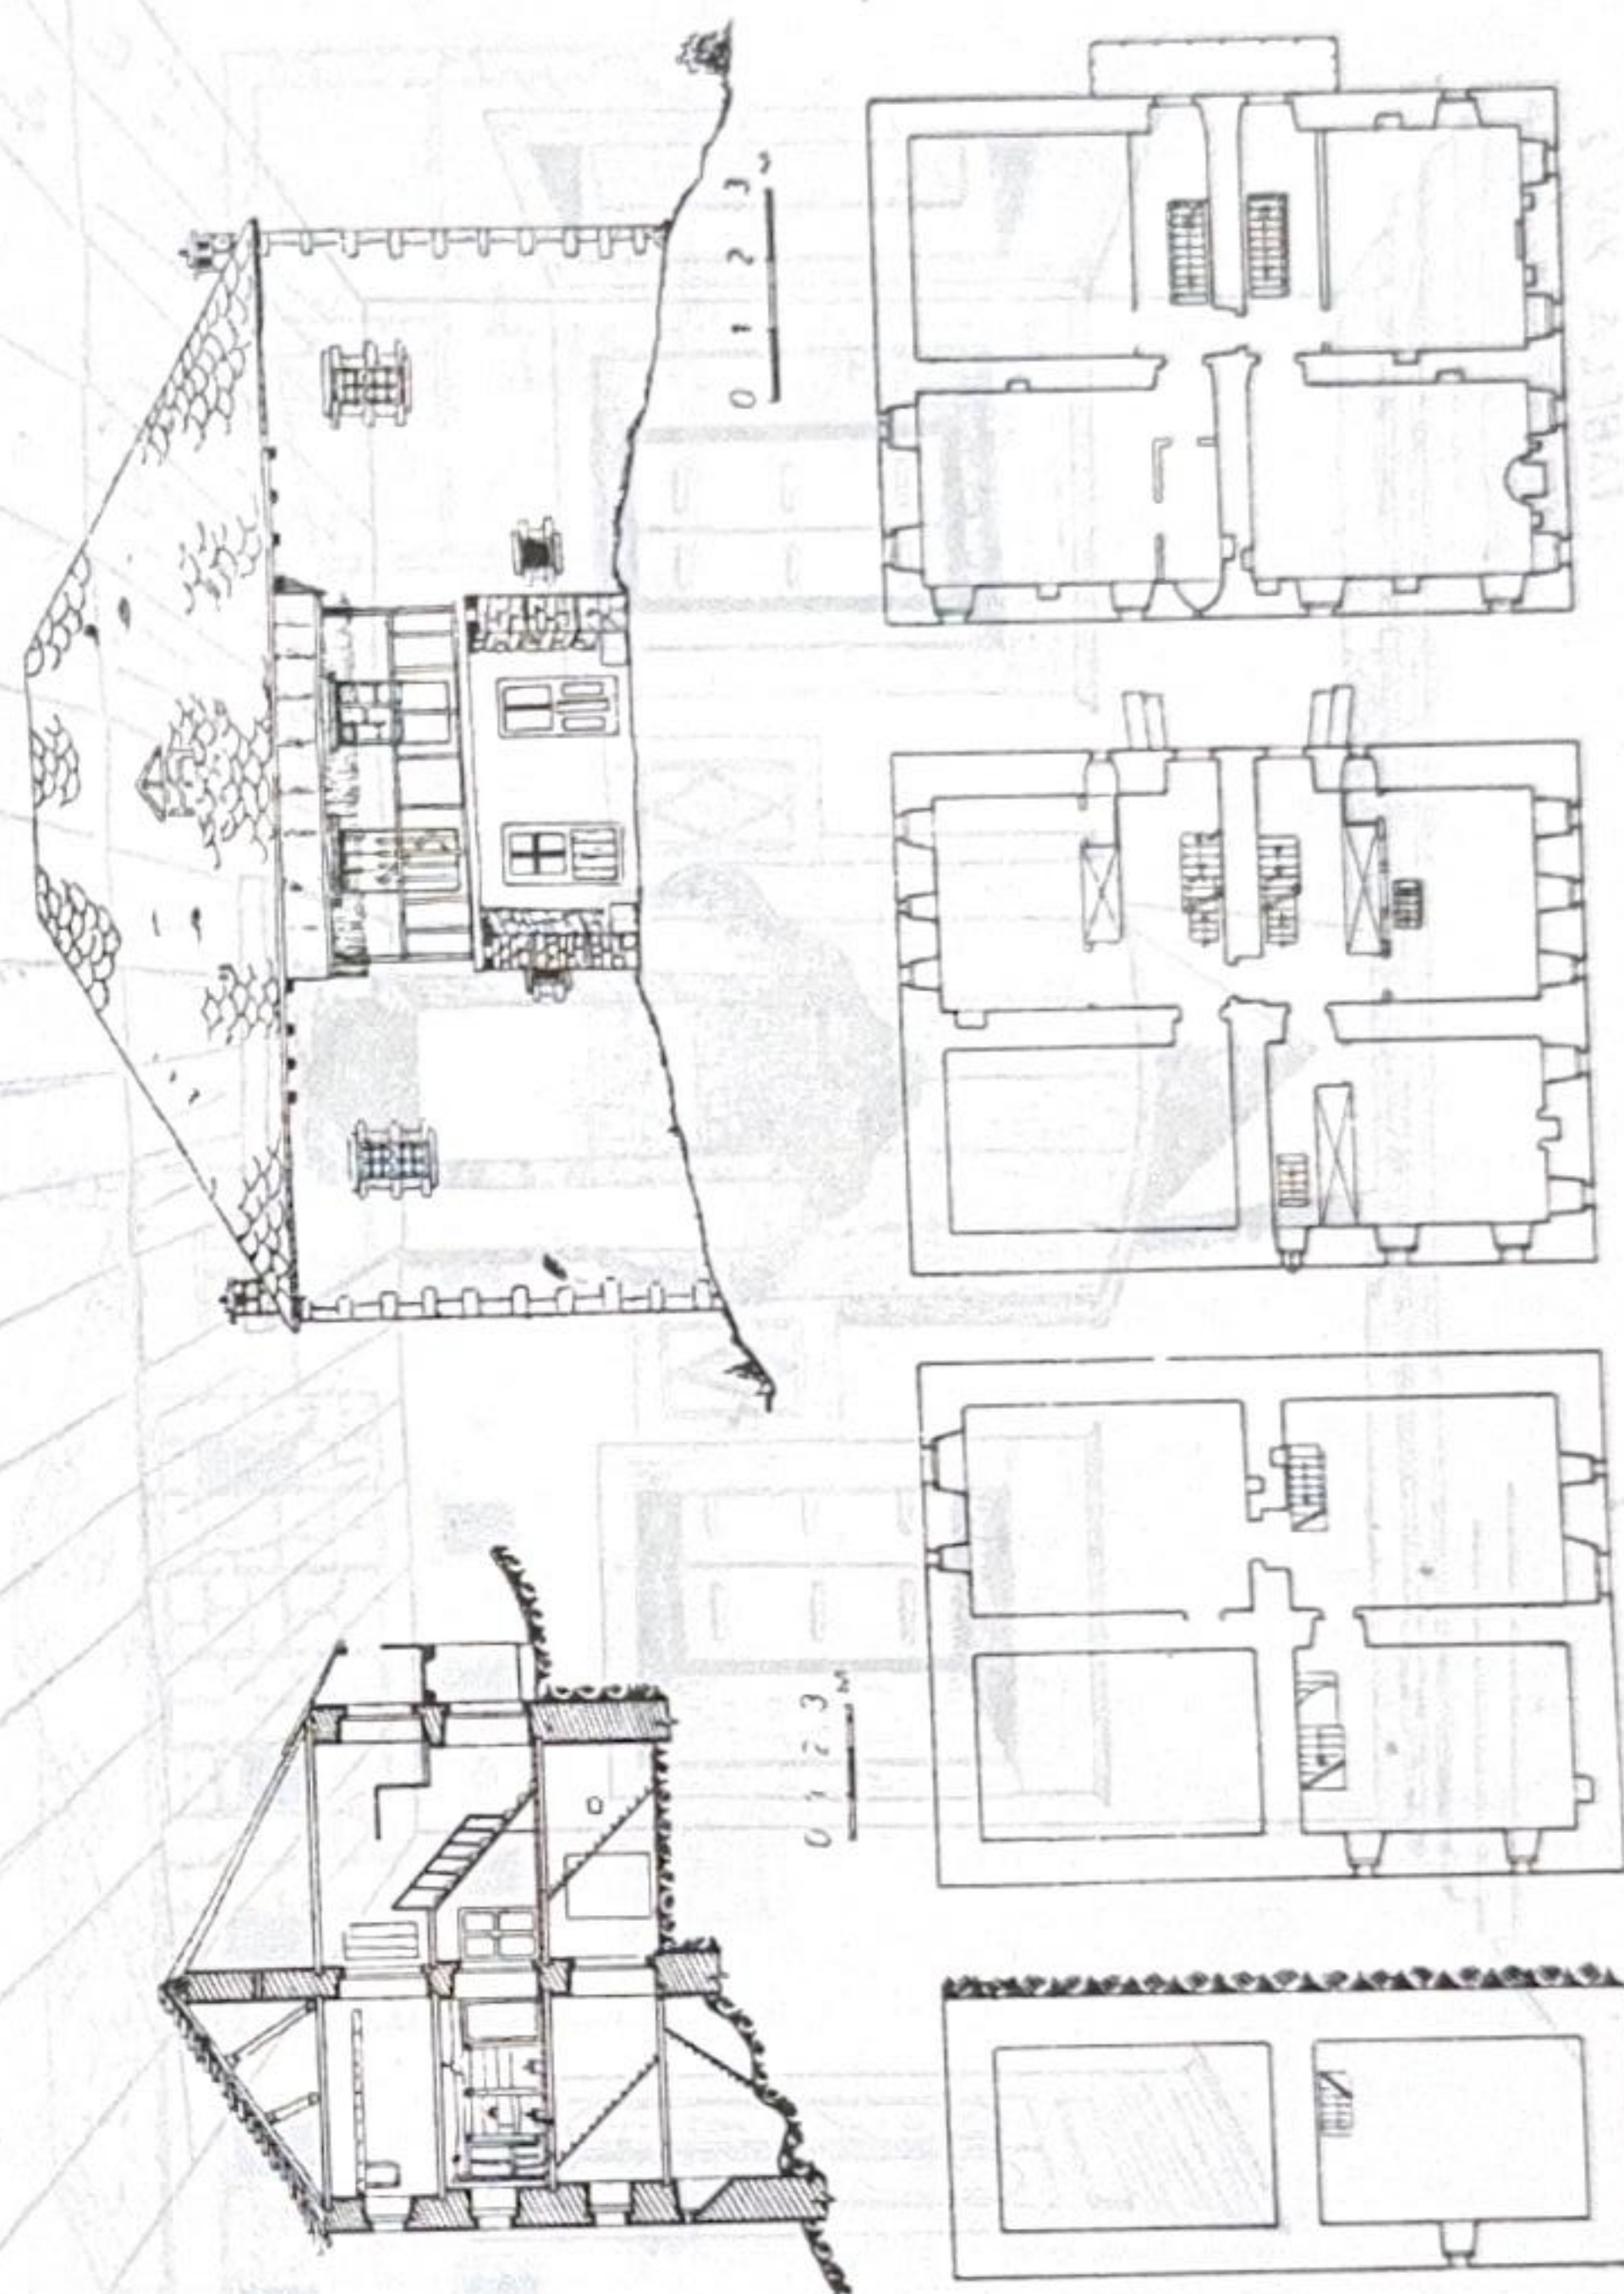


TABELA XIII

TABELA XIV¹




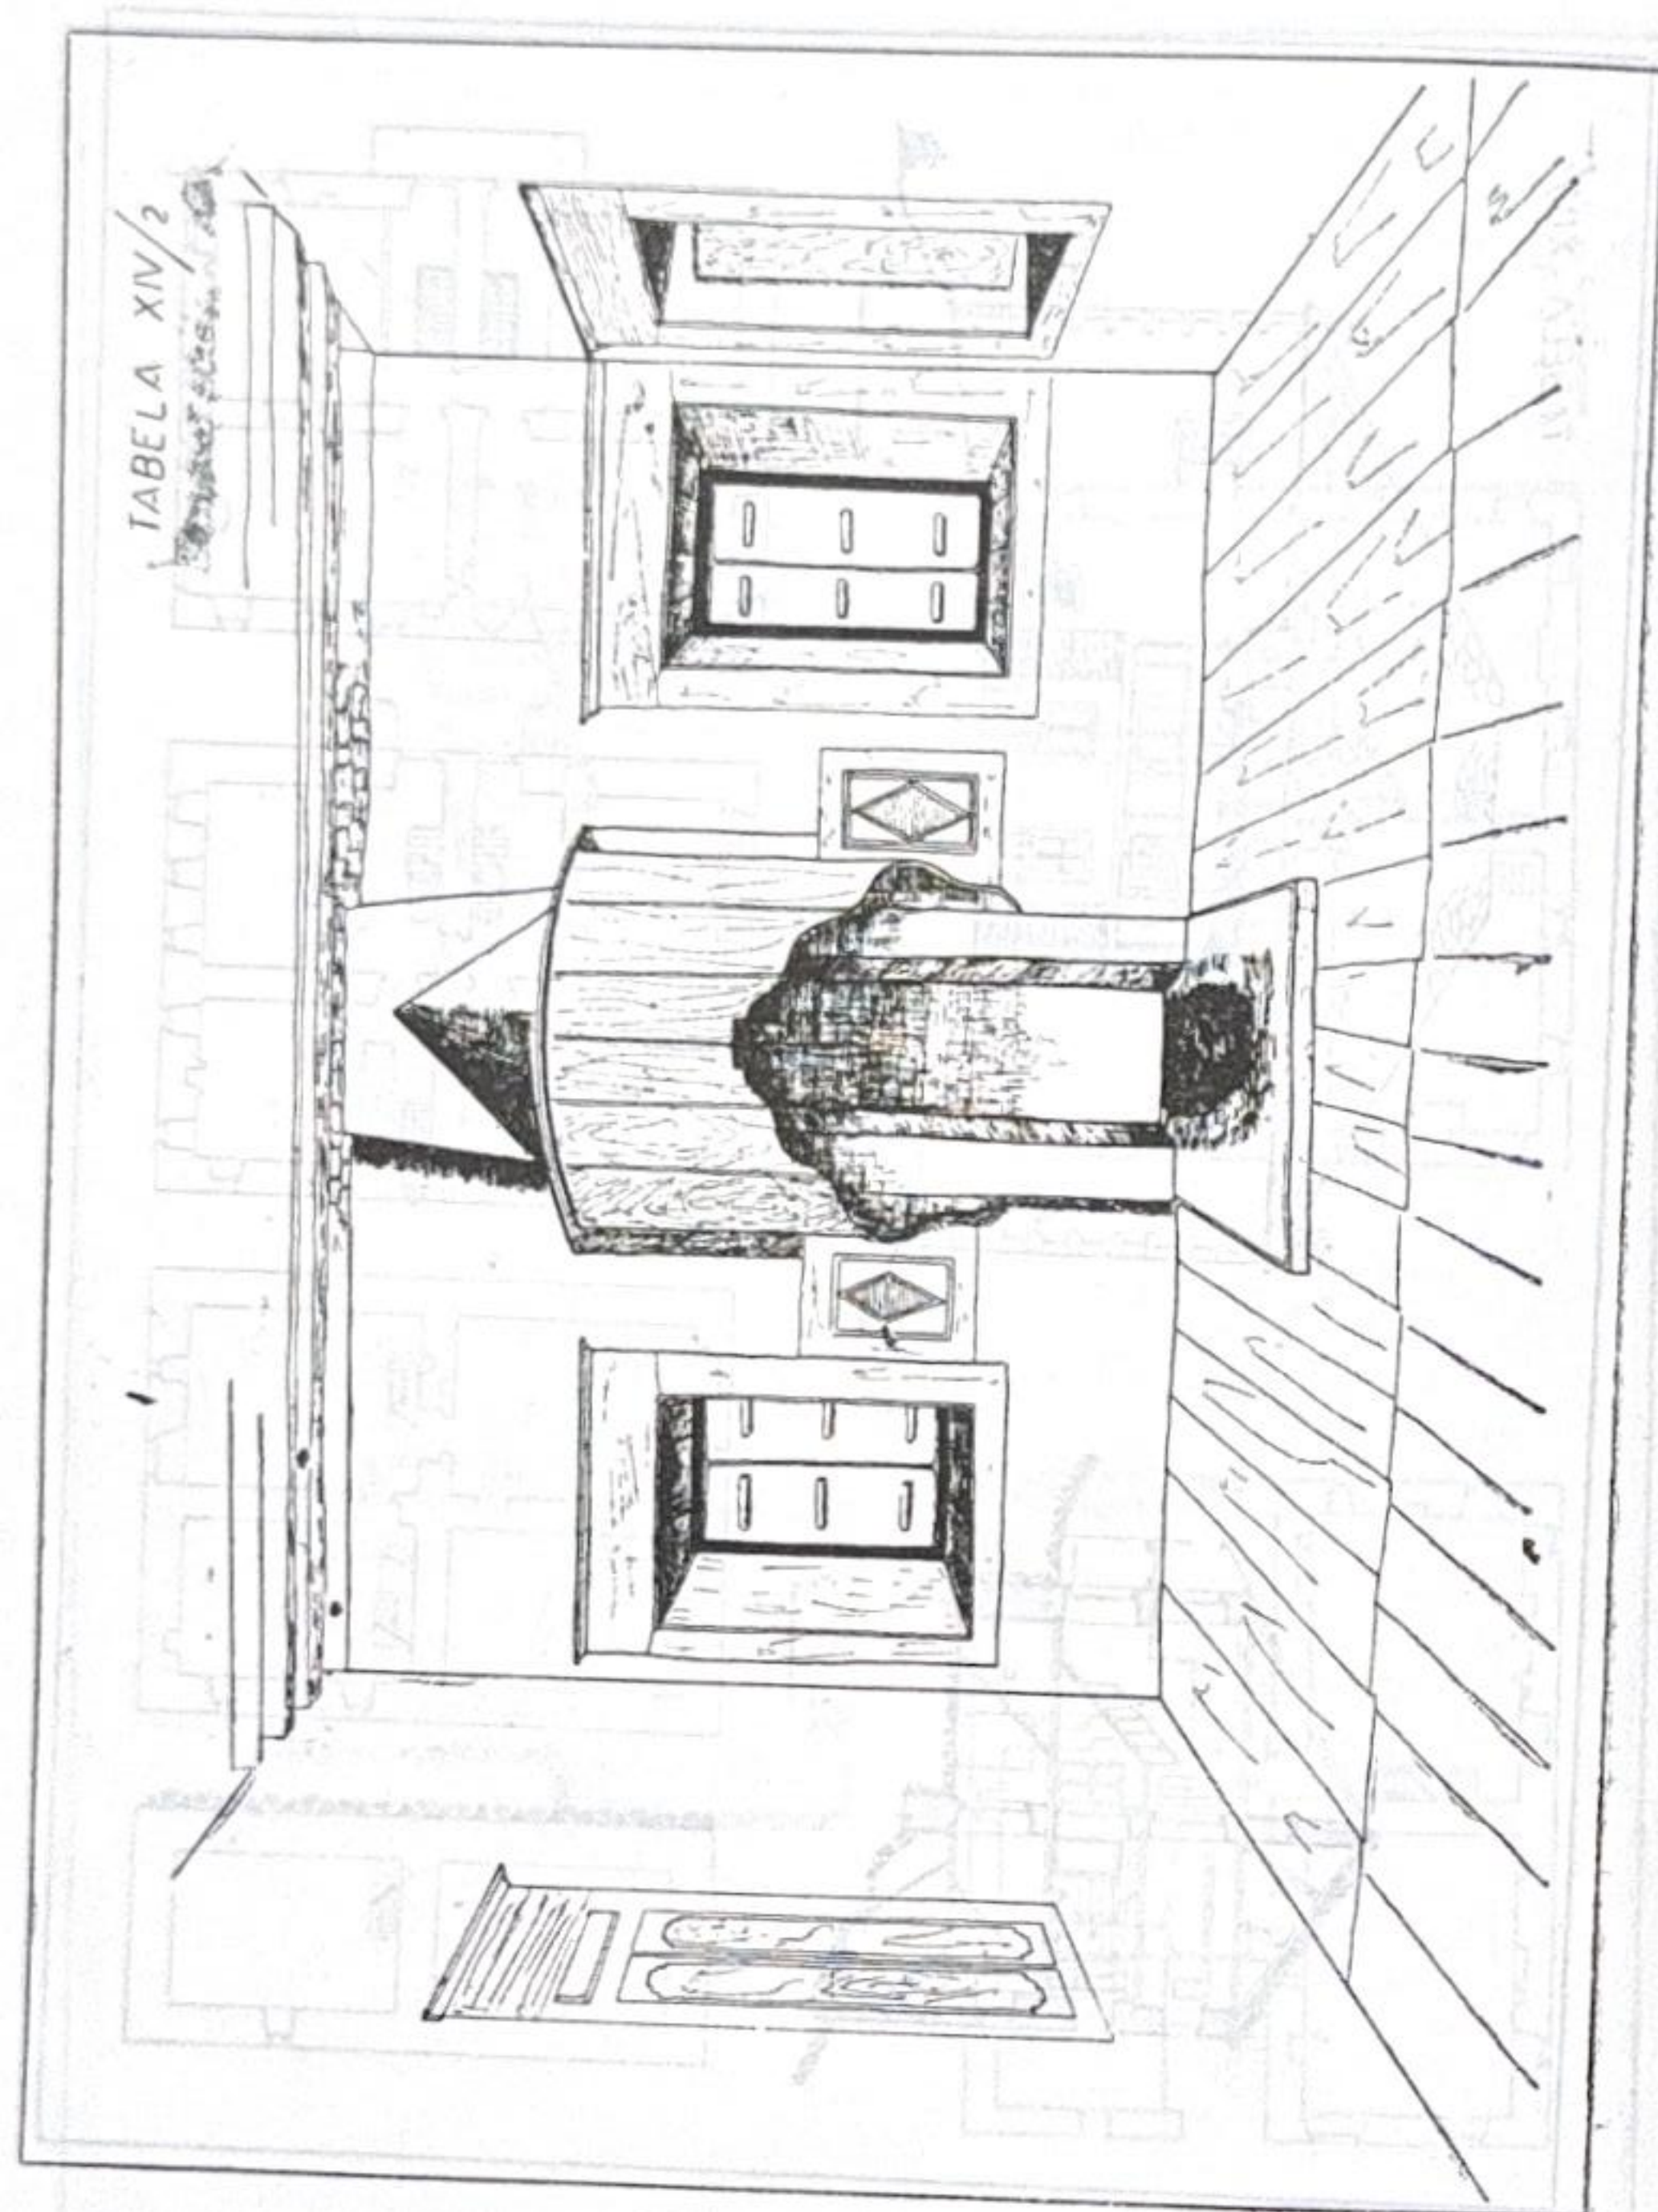


TABELA XV

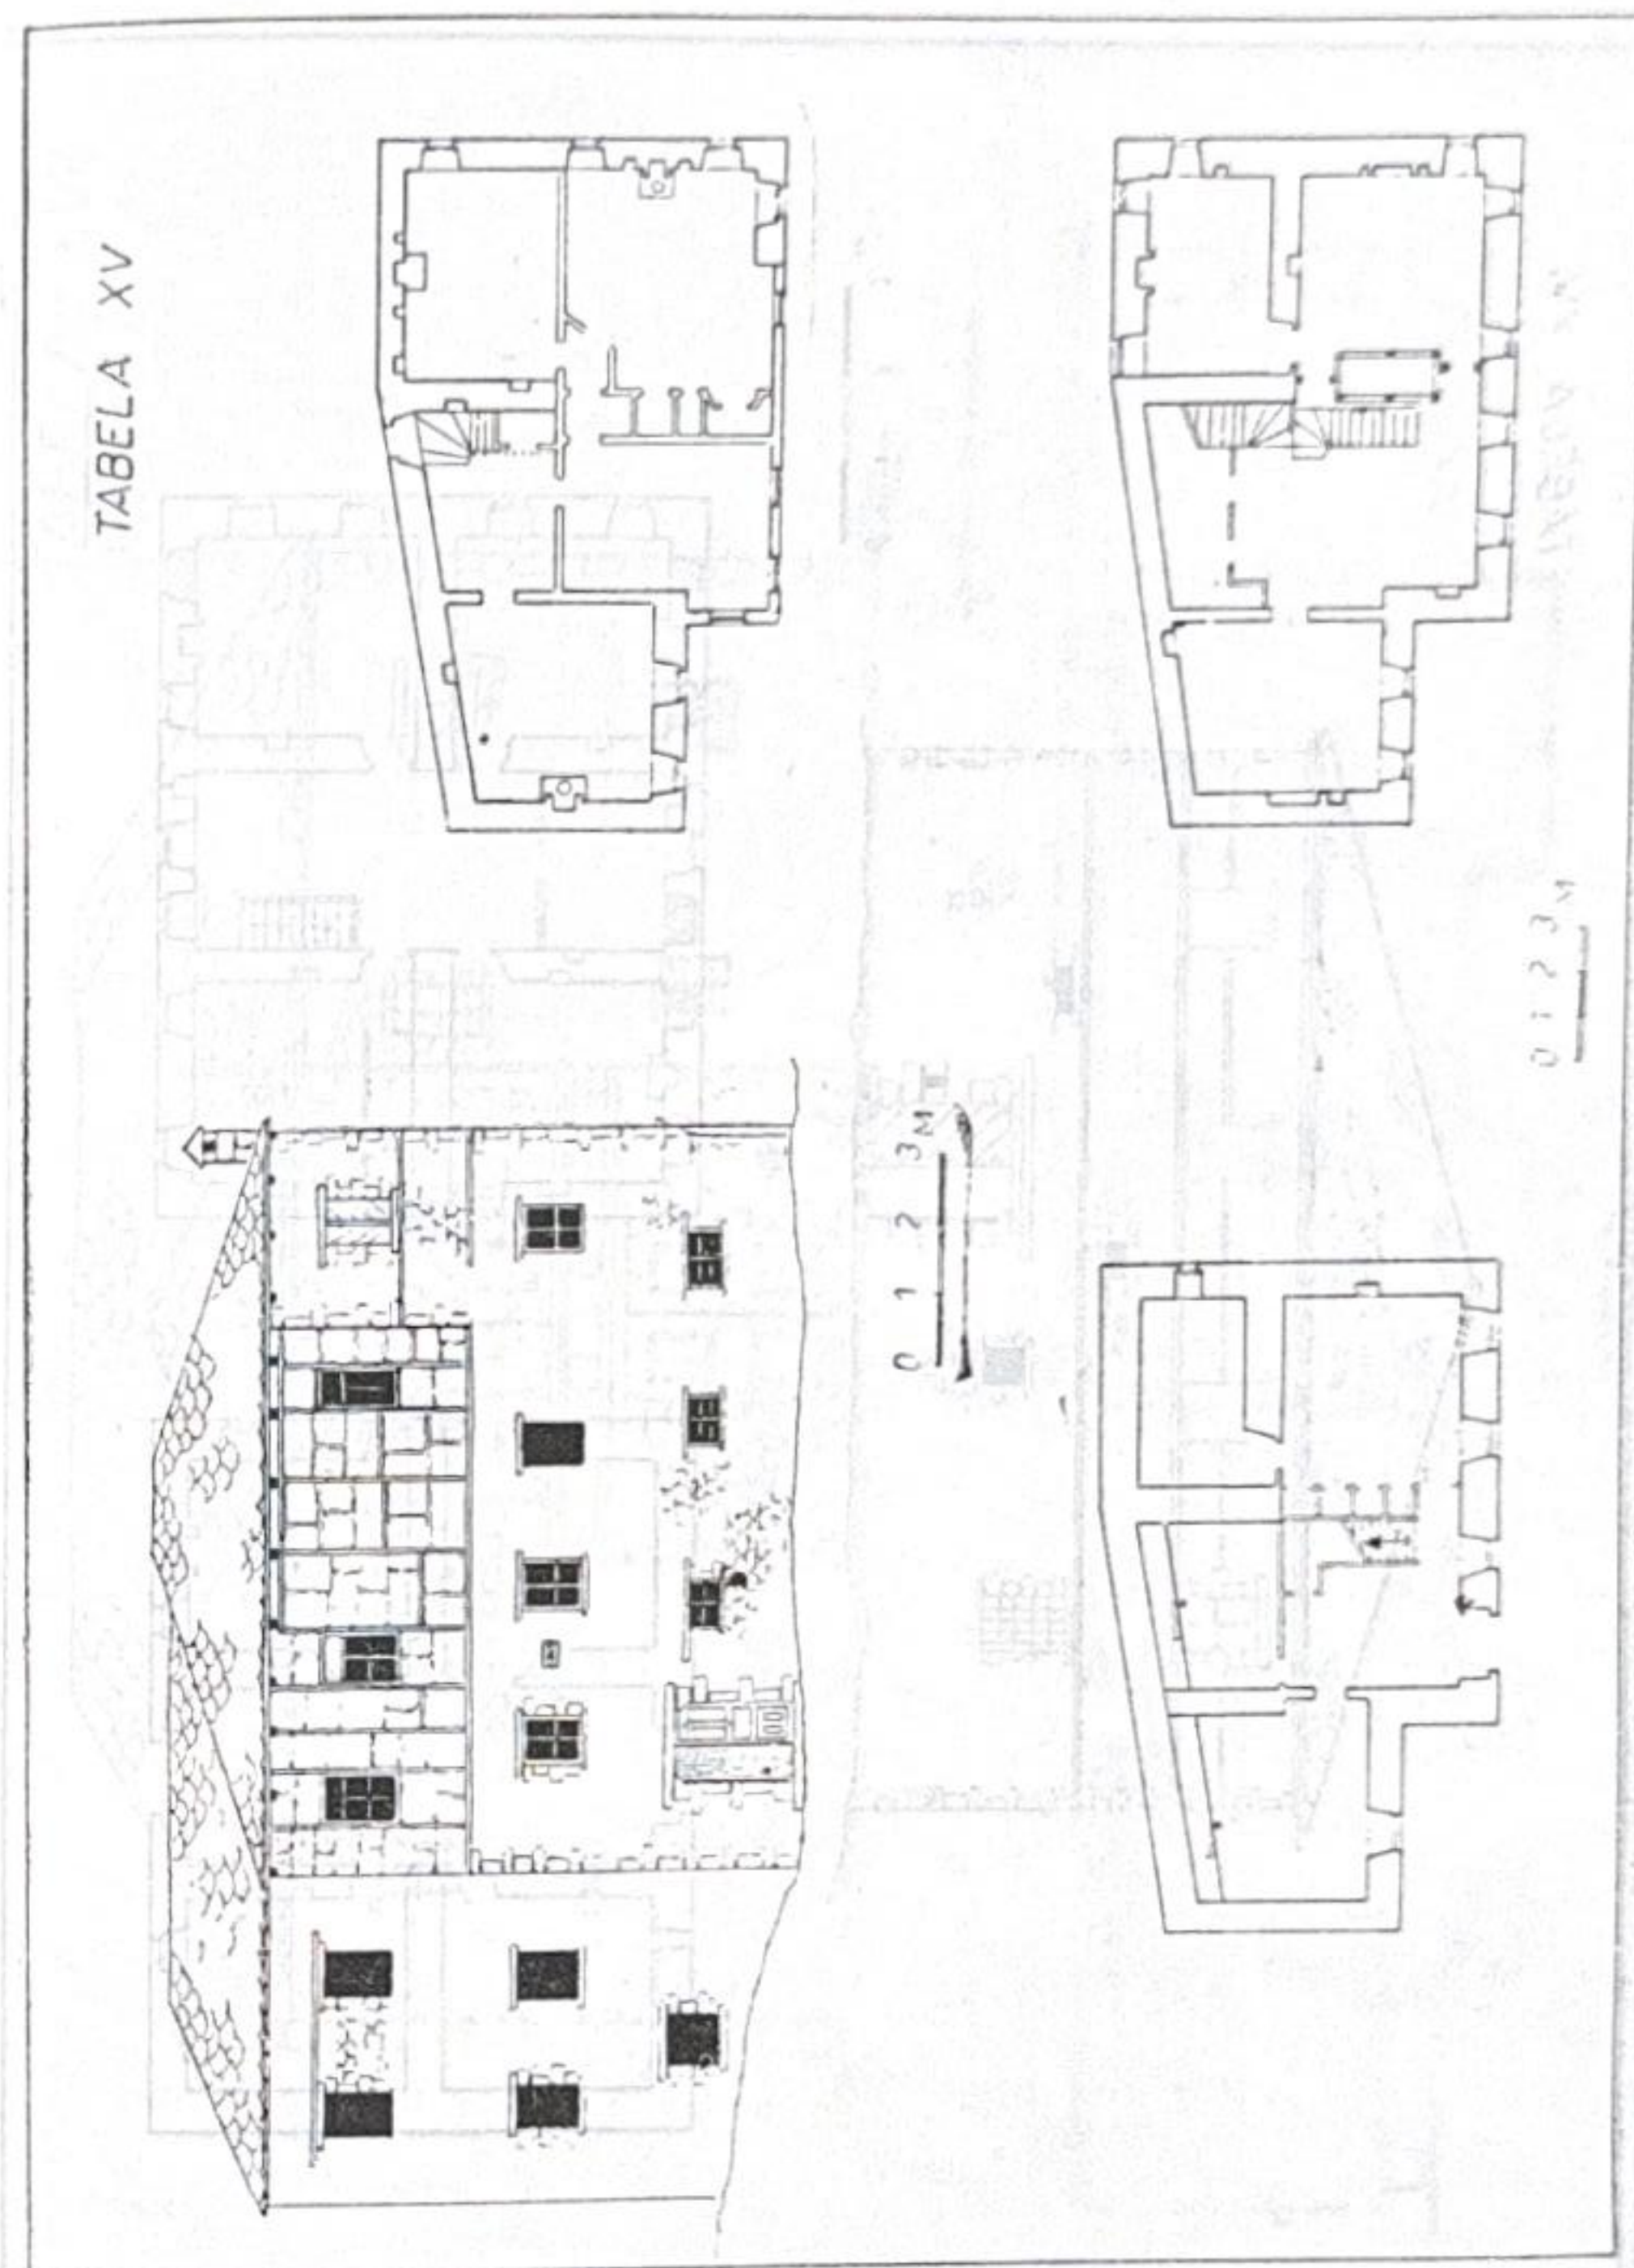

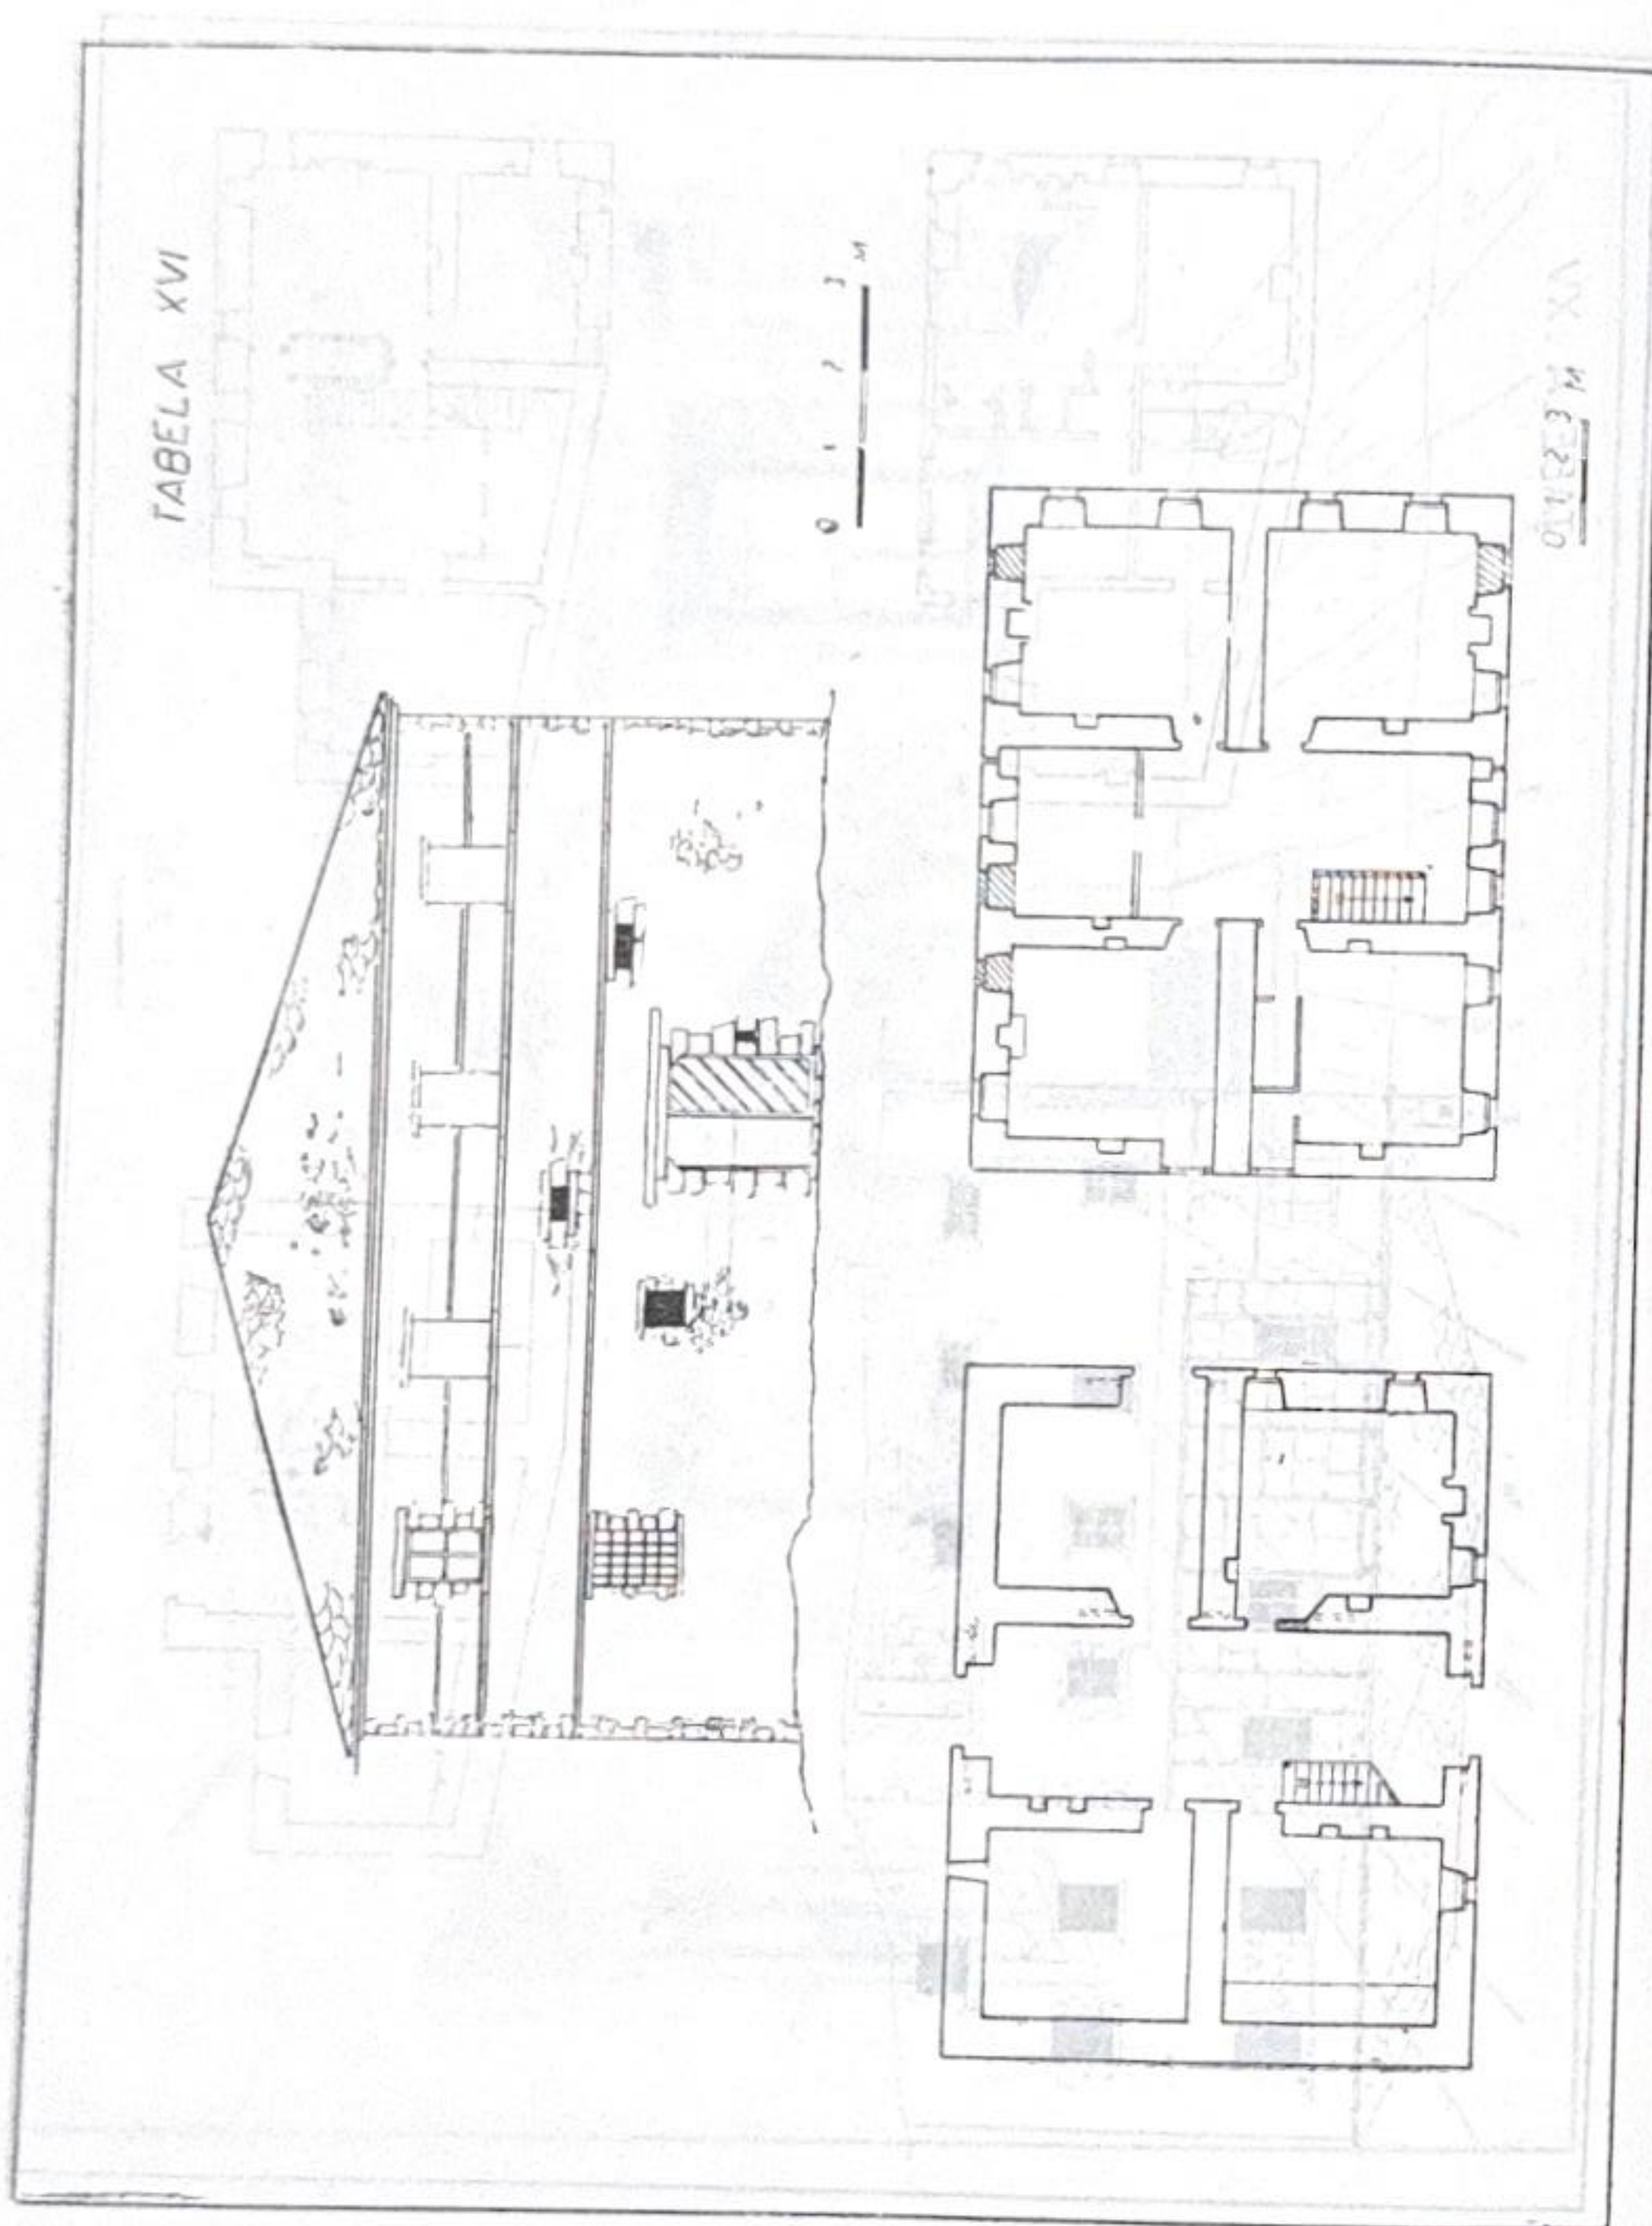

TAB. XVII

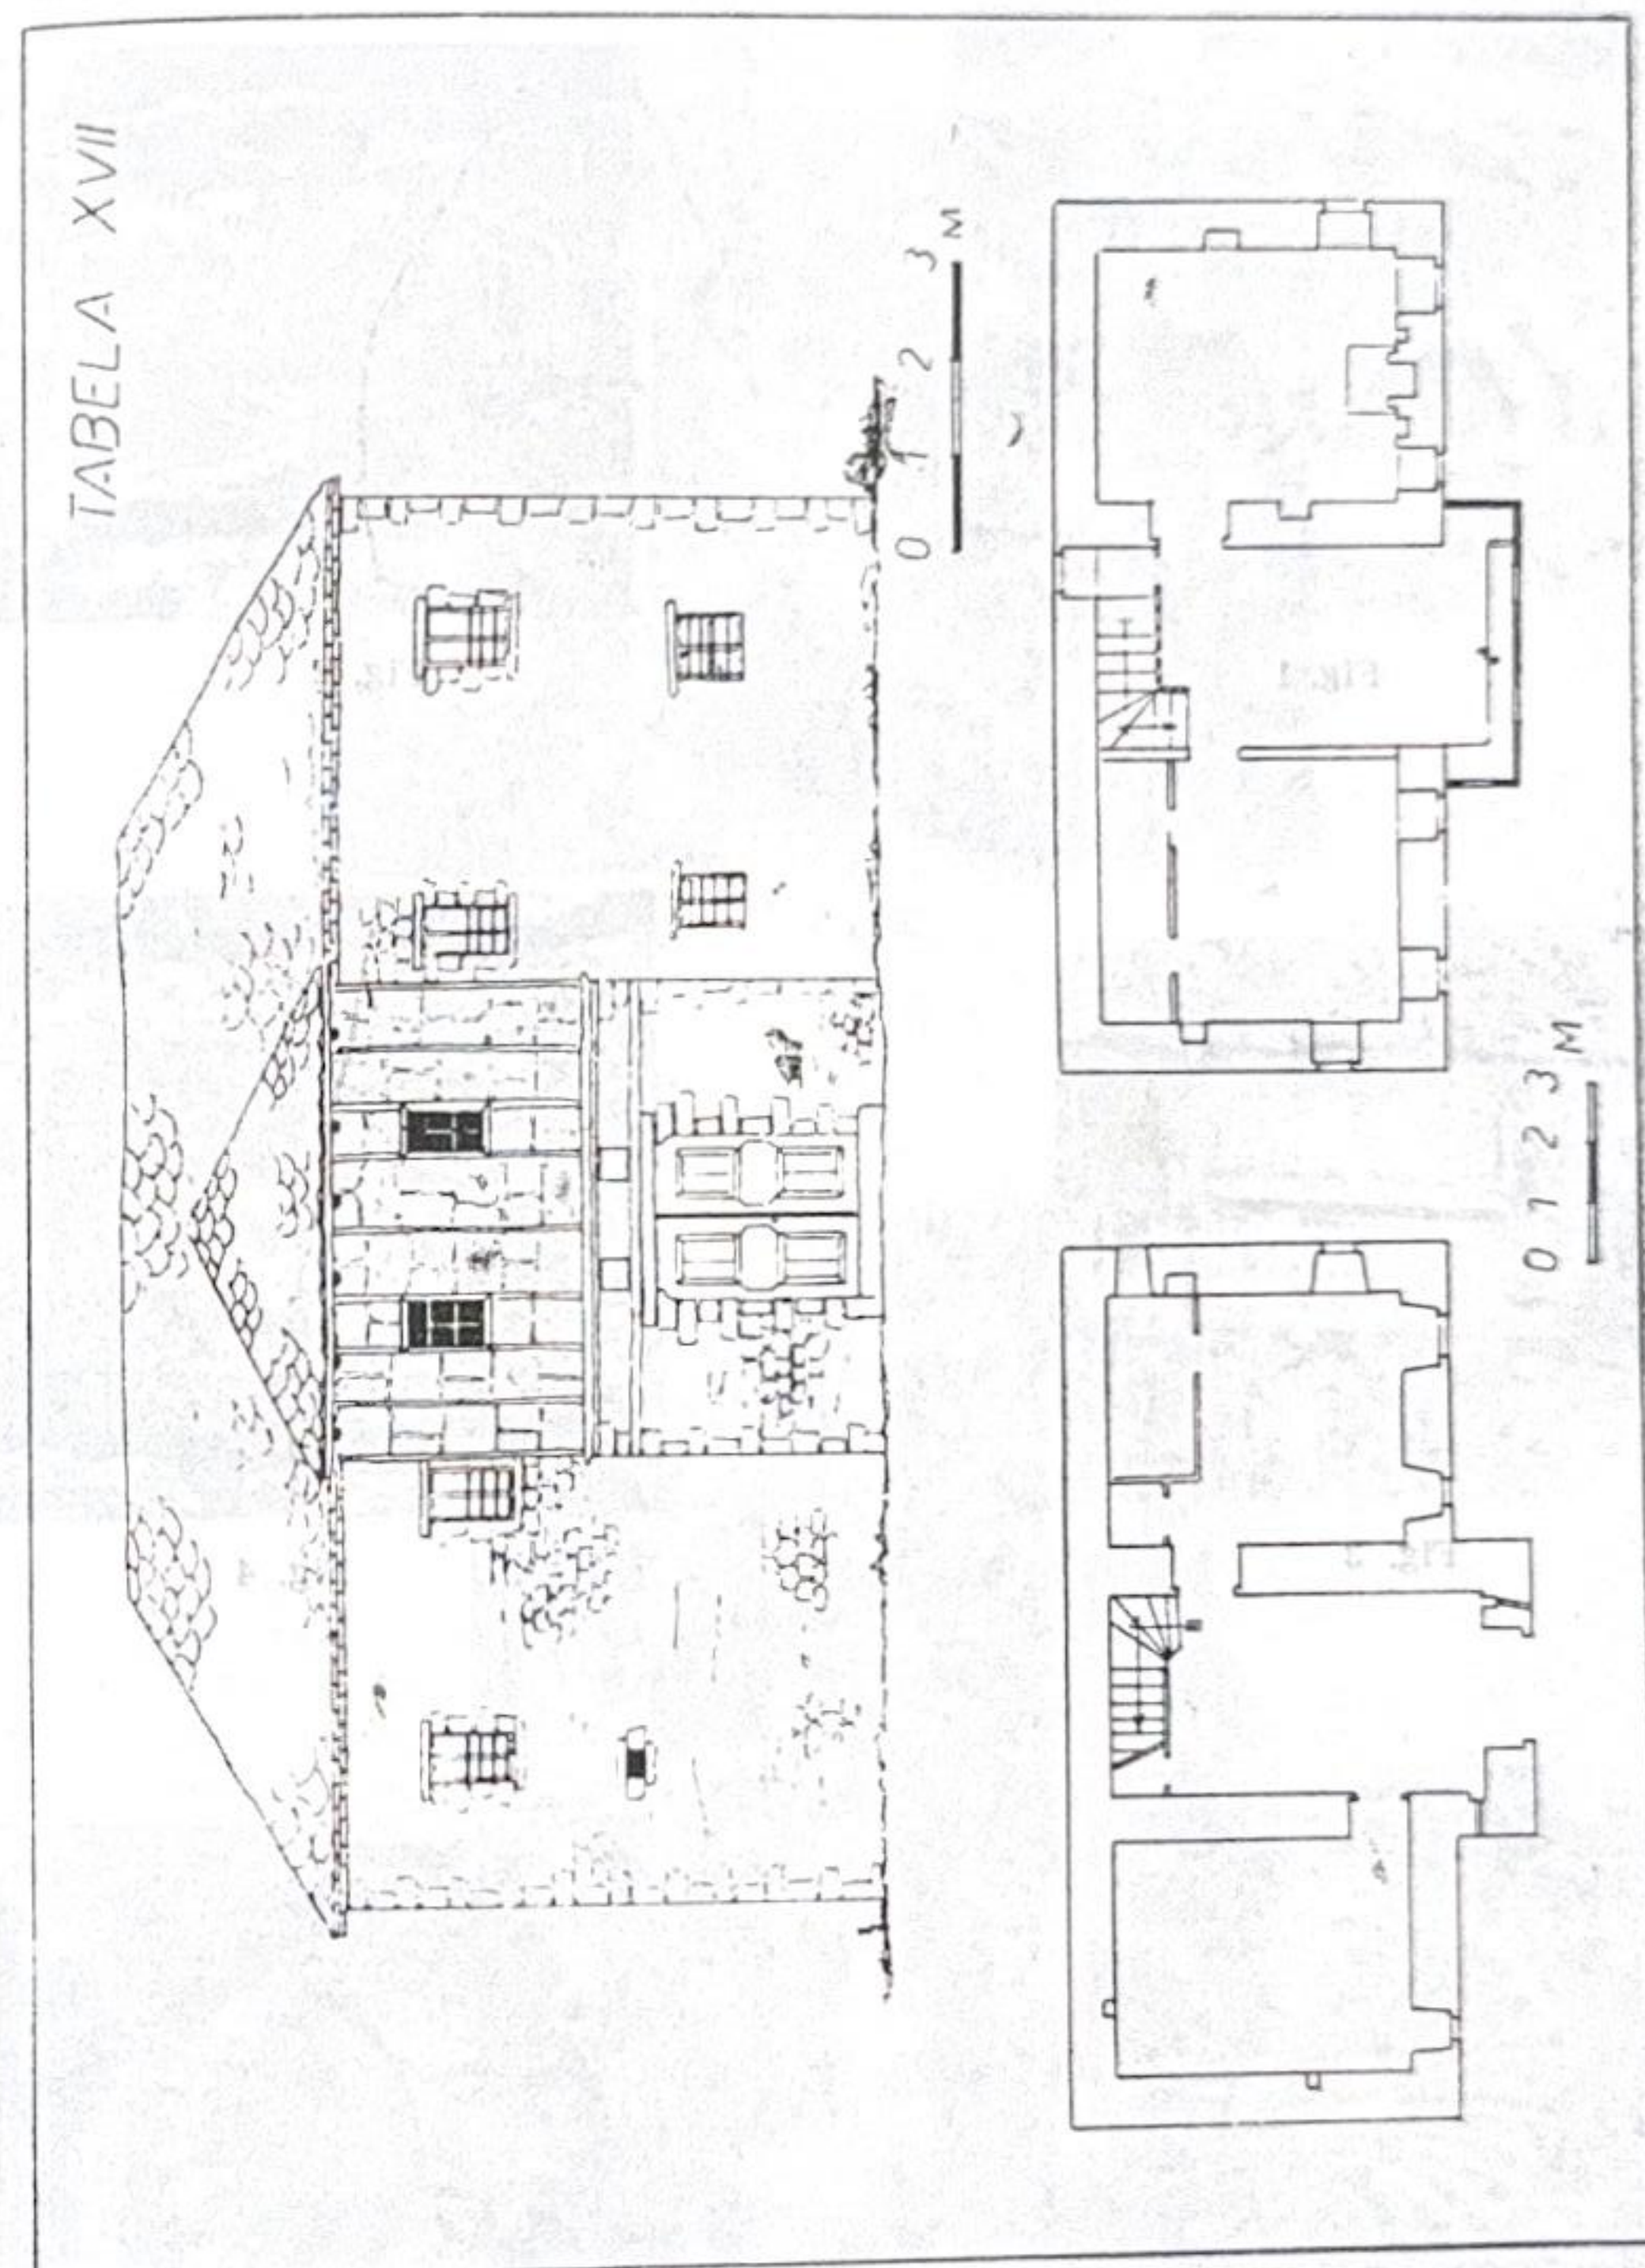

TAB. XVIII



Fig. 1



Fig. 2

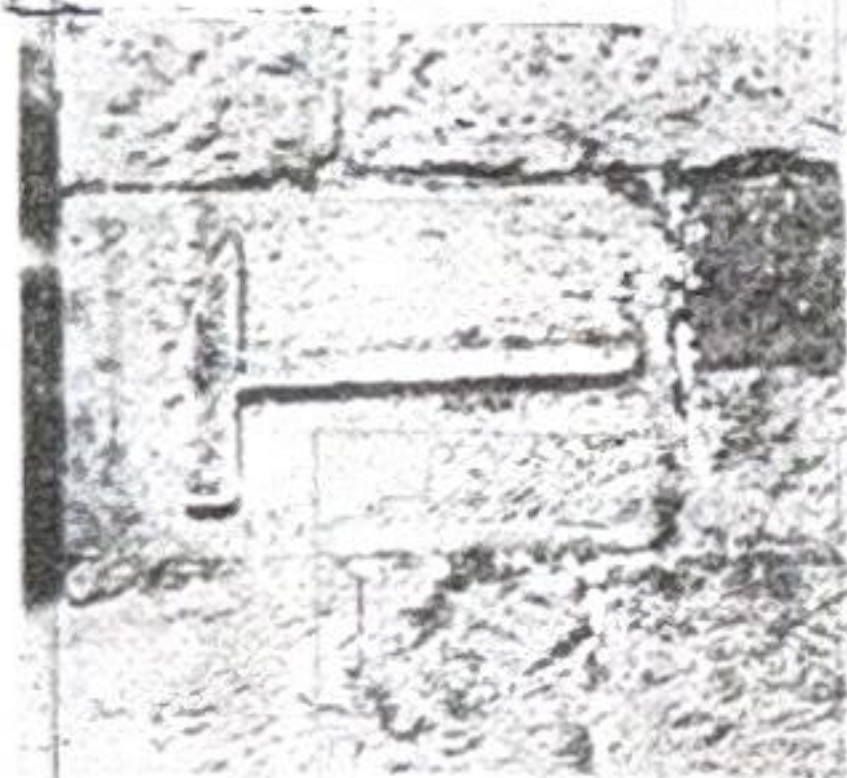


Fig. 3



Fig. 4



Fig. 5



Fig. 6

TAB. XIX



Fig. 1

Gjatë shekullit XIX dhe në fillim të shekullit XX, në fshatin Dardhë-Korçë, si edhe në pjesët e ndryshme të krahinës, veç pajtimit të krahut me lirin, u ndërtuan shtëpi të mëdha, të cilat u përdorën si shtëpi të banorëve të fshatit.

Masa e përdorur për ndërtimin e këtyre shtëpive ishte guri, ku si në të vjetër, as në të reja, në zonat rurale, ku ishin më të shpeshta, Krushë, Shkodër, për interiore banorë, të prapësishme jo vetëm, por edhe në pjesët e tjera të fshatit dhe të krahinës të gjerë.

Në ndërtimin e këtyre shtëpive, si dhe vazhdimi i ndërtimit të fshatit dhe në qytet, në krahinën e Zadrisë, ndonëse kanë qenë të ndryshme, kujtimet e vjetra.

Në këtë studim, si lidhur me zhvillimin e fshatit dhe në fund të shekullit XIX dhe në fillim të shekullit XX, punimi bazohet në të dhënat e vitit 1982 si në fshat dhe në qytet, por edhe në ndërtimin e këtyre shtëpive.

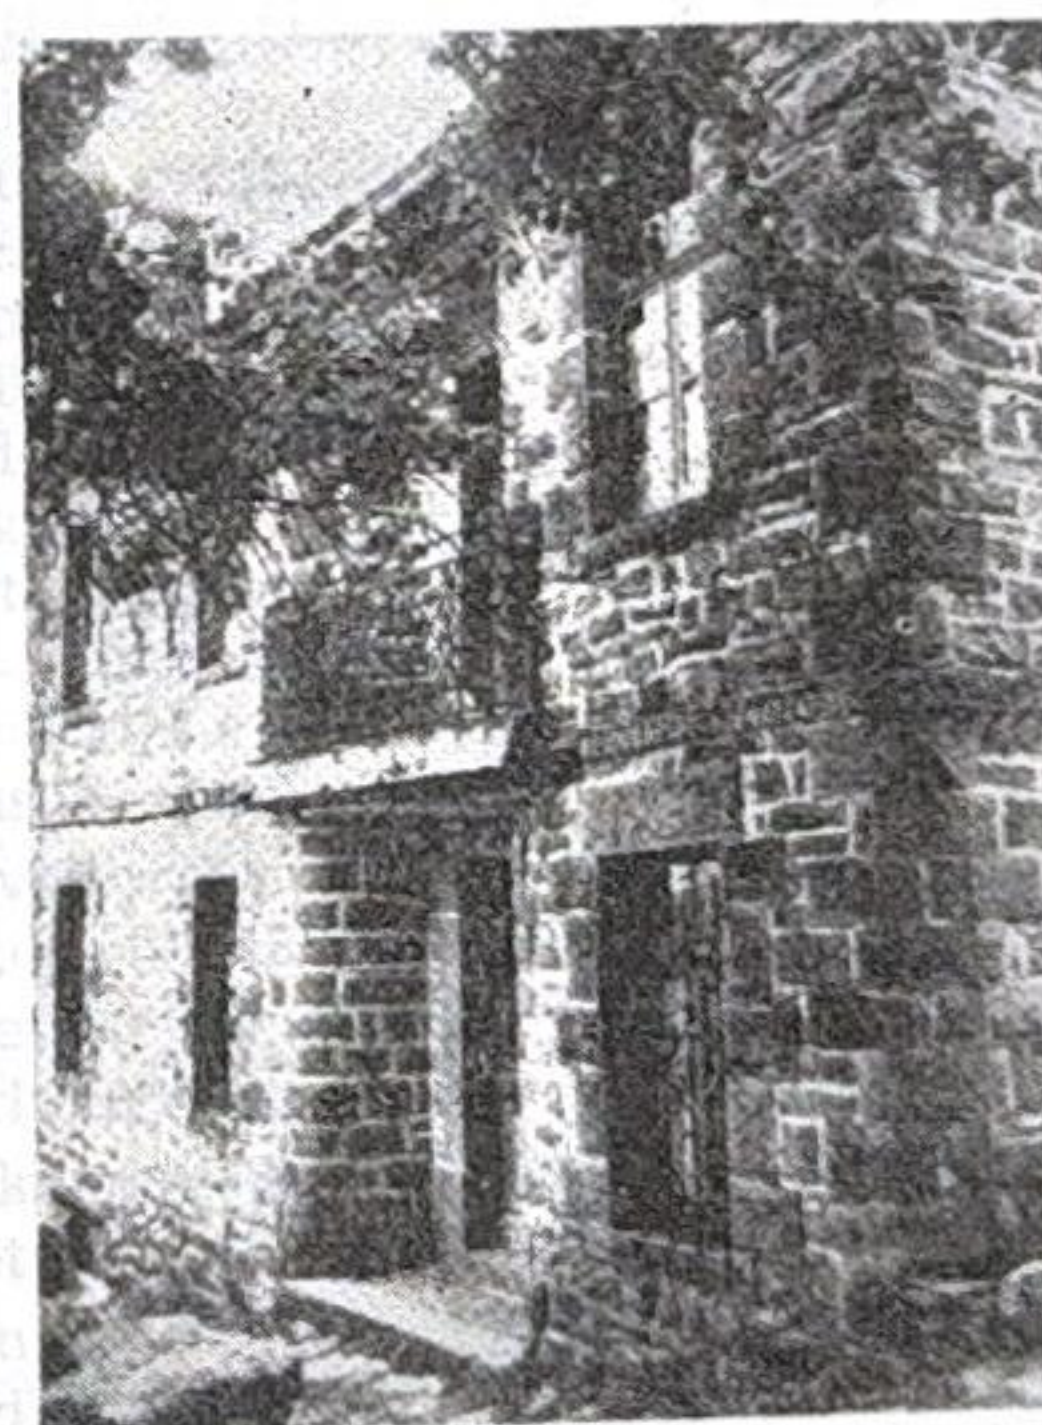


Fig. 2